

three inches = one foot
one and one half inches = one foot
one inch = one foot
three quarters inch = one foot
one half inch = one foot
three eighths inch = one foot
one quarter inch = one foot
one eighth inch = one foot




U.S. DEPARTMENT OF VETERANS AFFAIRS

REPLACE FINISHES B1AC D-WING ROSEBURG VA HEALTH CARE SYSTEM 913 NW GARDEN VALLEY BLVD., ROSEBURG, OR 97471 PROJECT NUMBER: 653-24-103 REPLACE FINISHES B1AC D-WING

GENERAL CONDITIONS:


- THE CONTRACTOR IS RESPONSIBLE FOR CHECKING THE SITE CONDITIONS AND THE PLANS, AND TO NOTIFY THE OWNER OF ANY ERRORS OR OMISSIONS PRIOR TO THE START OF CONSTRUCTION.
- DRAWINGS ARE NOT TO SCALE. CONTACT VA ENGINEER COR FOR CLARIFICATION IF NECESSARY.
- CONTRACTOR SHALL OBTAIN ALL PERMITS REQUIRED BY LOCAL STATE AND FEDERAL GOVERNING AUTHORITIES.
- ALL WORK SHALL MEET THE STANDARDS AND SPECIFICATIONS OF VETERAN AFFAIRS, THE GOVERNING AUTHORITY. REFERENCE CODES, STANDARDS AND AMENDMENTS SHALL BE THE EDITION MOST RECENTLY ADOPTED OR IN USE IN THE JURISDICTION.
- CONTRACTOR SHALL VERIFY ALL DIMENSIONS IN FIELD AND SHALL COORDINATE INSTALLATION OF ALL MATERIAL AND/OR EQUIPMENT WHOSE DIMENSIONS ARE FIXED. IN THE EVENT THAT EXISTING CONDITIONS ARE FOUND TO VARY FROM ASSUMED CONDITIONS, NOTIFY VA ENGINEER COR IMMEDIATELY FOR CLARIFICATION.
- CONTRACTOR SHALL COORDINATE THE WORK OF ALL TRADES REQUIRED TO PERFORM THE WORK WHERE INSTALLATION AND/OR CONNECTION OF EQUIPMENT IS NOT SPECIFIED AND WHERE SUCH CONNECTION AND/OR INSTALLATION IS REQUIRED. FOR A COMPLETE AND OPERABLE FACILITY, THE CONTRACTOR SHALL BE HELD RESPONSIBLE FOR SUCH INSTALLATION AND/OR CONNECTION.
- ALL WORK REQUIRED BY THESE CONTRACT DOCUMENTS SHALL BE FURNISHED AND INSTALLED COMPLETE AND IN OPERATING CONDITION. THE CONTRACTOR SHALL FURNISH AND INSTALL ANY ITEMS THAT MAY NOT BE COVERED IN THE PLANS, BUT ARE NECESSARY TO PROVIDE A COMPLETE AND WORKABLE PROJECT.
- REPETITIVE FEATURES NOT NOTED ON THE DRAWINGS SHALL BE COMPLETELY PROVIDED AS IS DRAWN IN FULL. IF CERTAIN FEATURES ARE NOT FULLY SHOWN OR CALLED FOR ON THE DRAWINGS, THE CONSTRUCTION SHALL BE OF THE SAME CHARACTER AS FOR SIMILAR CONDITIONS THAT ARE SHOWN OR CALLED FOR.
- CONTRACTOR IS RESPONSIBLE FOR ALL BRACING AND SHORING, ENVIRONMENTAL PROTECTIONS AND COMPLETION OF THE WORK.
- HAZARDOUS MATERIALS MAY EXIST ON THIS PROJECT. FOLLOW VA GUIDELINES.
- DIMENSIONS ARE TO THE FACE OF STUD AT WALLS, FACE OF CONCRETE AT FOUNDATION WALLS, TO THE CENTER OF COLUMNS AND OPENINGS AND TO THE TOP OF SLAB OR PLYWOOD SUB-FLOOR UNLESS OTHERWISE NOTED. DIMENSIONS OF DOOR AND WINDOW SIZES ARE APPROXIMATE. CONTRACTOR TO VERIFY ALL SUCH DIMENSIONS AND ROUGH OPENINGS WITH MANUFACTURERS.
- CONTRACTOR TO VERIFY ALL ELEVATIONS PRIOR TO STARTING WORK AND VERIFY SIZE, LOCATION AND MATERIAL REQUIRED. NOTIFY VA ENGINEER OF ANY VARIATIONS.
- NO PORTION OF THE WORK REQUIRING A SHOP DRAWING OR SAMPLE SUBMISSION SHALL BE COMMENCED UNTIL THE SUBMISSION HAS BEEN APPROVED BY THE OWNER'S REPRESENTATIVE. ALL SUCH PORTIONS OF THE WORK SHALL BE IN ACCORDANCE WITH APPROVED SHOP DRAWINGS AND SAMPLE.
- THE AREA NEARBY THE CONSTRUCTION SITE WILL REMAIN IN OPERATION. COORDINATE WITH THE COR TO SCHEDULE THE WORK, DEMOLITION WORK, AND NOISY WORK MAY NEED TO BE DONE AFTER NORMAL BUSINESS HOURS. THE SAFETY OF THE PUBLIC MUST BE GUARDED CAREFULLY AT ALL PHASES OF CONSTRUCTION.
- NO PARTICLE BOARD IS TO BE USED.
- ALL STRUCTURAL CONNECTIONS TO THE EXISTING CONCRETE SHALL BE MADE TO CONCRETE BEAM ELEMENTS. NO STRUCTURAL CONNECTIONS SHALL BE MADE TO THE EXISTING THIN CONCRETE SLAB OR TOPPING SLAB.
- PERIODIC SPECIAL INSPECTION SHALL BE REQUIRED FOR ALL MECHANICAL ANCHORS POST INSTALLED INTO HARDENED CONCRETE. SPECIFIC REQUIREMENTS FOR INSPECTION SHALL BE AS DESCRIBED IN THE ICC TESTING REPORT FOR THE ANCHOR.
- SPRINKLER SYSTEM TO REMAIN ACTIVE IN CONSTRUCTION AREA DURING CONSTRUCTION OR CONTRACTOR TO MEET NFPA 241 BY OTHER METHODS.
- IT IS THE CONTRACTORS RESPONSIBILITY TO MOVE FURNITURE FROM OFFICES FOR WORK TO BE ACCOMPLISHED AND TO MOVE FURNITURE BACK AFTER WORK IS COMPLETE.
- CONTRACTOR SHALL SUBMIT A PHASING PLAN TO BE APPROVED BY THE COR PRIOR TO STARTING WORK.

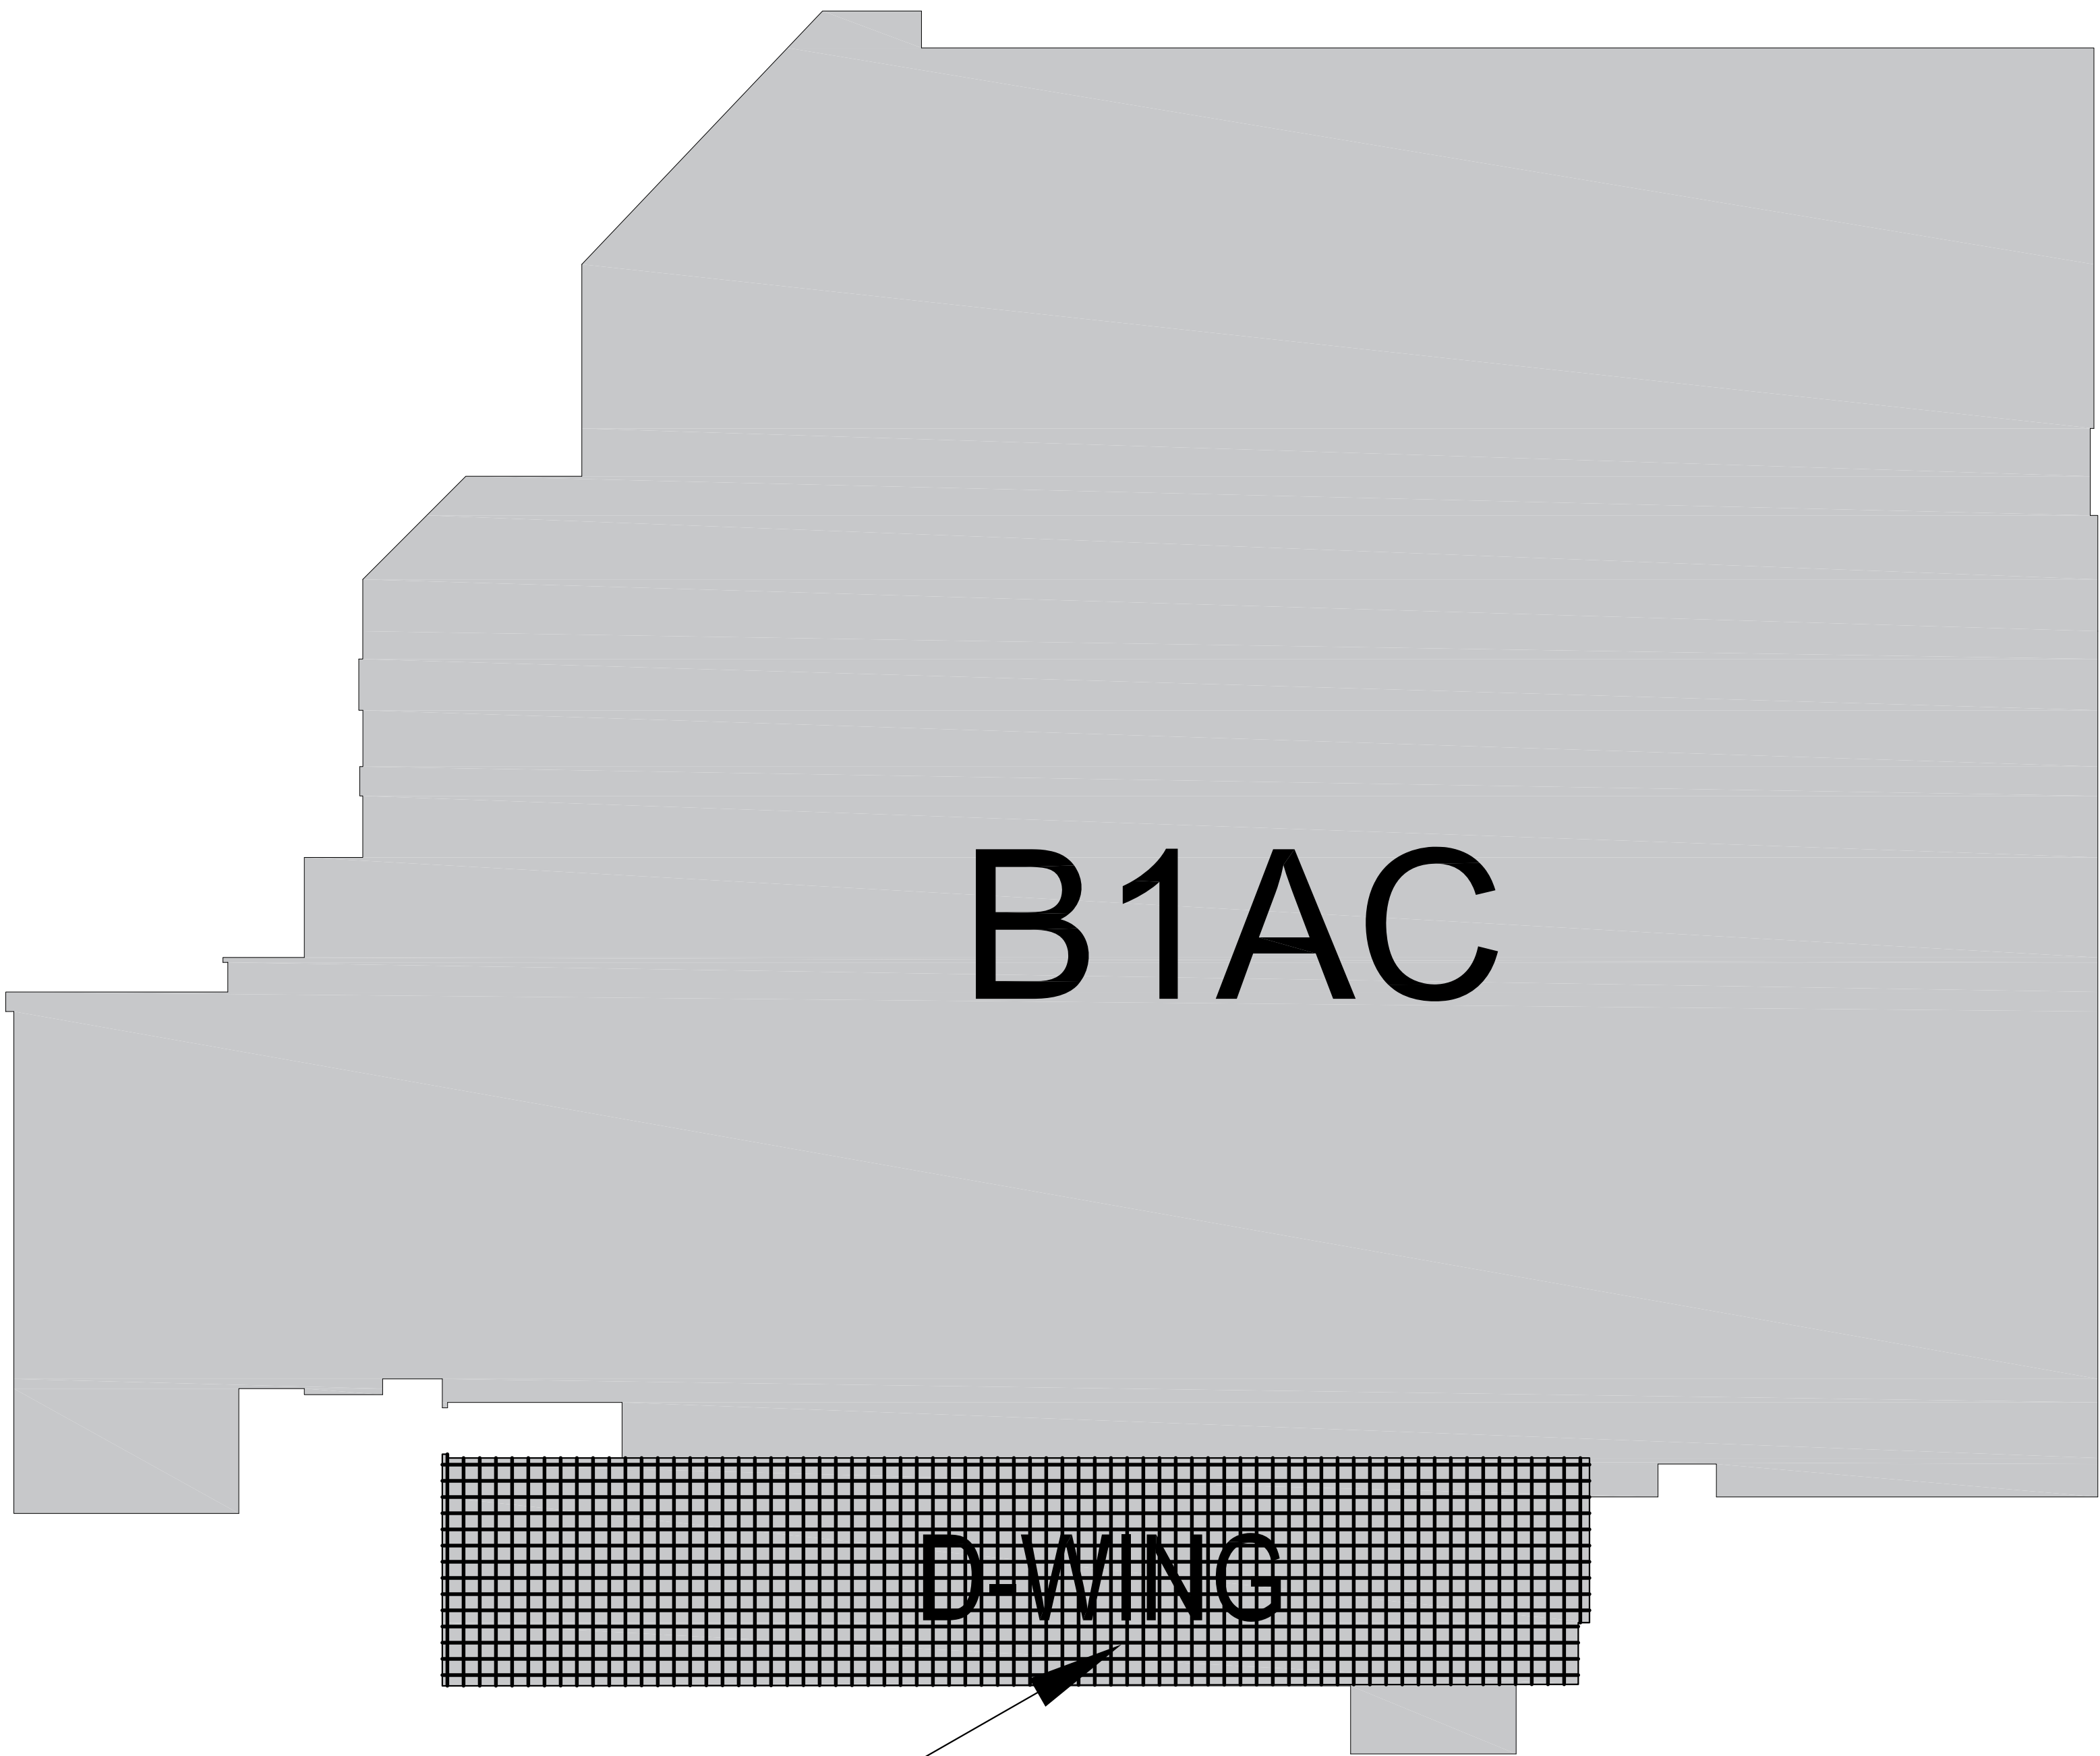

AREA OF WORK

EXISTING FLOOR PLAN
SCALE: NOT TO SCALE

DRAWING INDEX	
A-00	COVER, INDEX AND GENERAL NOTES
A-01A	DEMO FLOOR PLAN AREA A
A-01B	DEMO FLOOR PLAN AREA B
A-01C	DEMO FLOOR PLAN AREA C
A-02A	RCP DEMO PLAN AREA A
A-02B	RCP DEMO PLAN AREA B
A-02C	RCP DEMO PLAN AREA C
A-03A	FLOOR PLAN AREA A
A-03B	FLOOR PLAN AREA B
A-03C	FLOOR PLAN AREA C
A-04A	RCP PLAN AREA A
A-04B	RCP PLAN AREA B
A-04C	RCP PLAN AREA C
A-05	DETAILS AND FINISH SCHEDULE

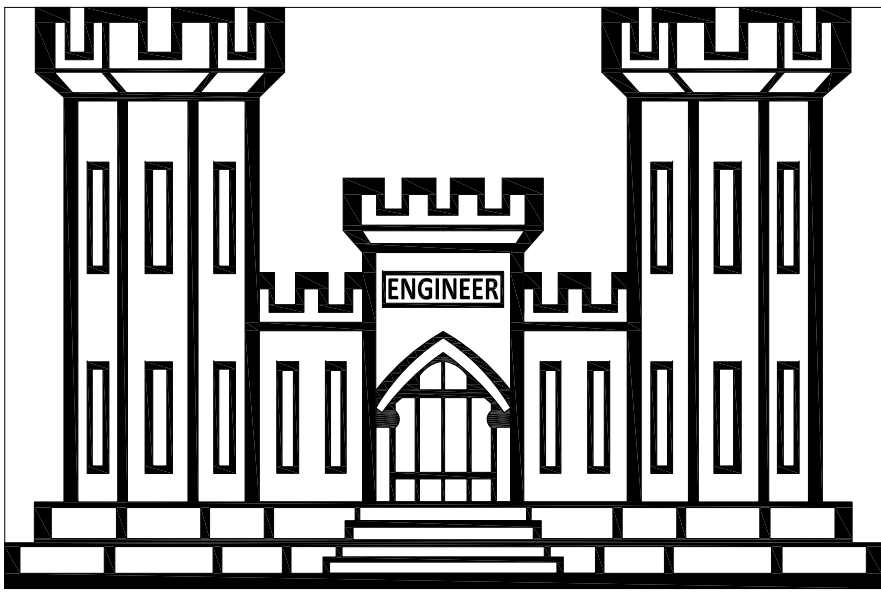

V.A. ROSEBURG
HEALTHCARE SYSTEM
VA
VISN20

U.S. DEPARTMENT OF VETERANS AFFAIRS
VA ROSEBURG HEALTHCARE SYSTEM
913 NW GARDEN VALLEY BLVD.
ROSEBURG, OR. 97471
(541) 440-1000

PROFESSIONAL SEAL

BUILDING NAME:
AMBULATORY CARE – D-WING

DRAWING SCALE:
SCALE: NTS

LOCATION:
ROSEBURG, OR

PROJECT TITLE:
REPLACE FINISHES B1AC D-WING

DESIGNED:
MWR

CHECKED:
–

REVIEWED:
–

DRAFTED:
MWR

DRAWING TITLE:
COVER PAGE


BUILDING NO:
1AC

FLOOR NO:
1

PROJECT NO:
653-24-103
DATE:
5/18/2023
SHEET NO:
A-00

OFFICE OF
FACILITIES

three inches = one foot
one and one half inches = one foot
one inch = one foot
three quarters inch = one foot
one half inch = one foot
three eighths inch = one foot
one quarter inch = one foot
one eighth inch = one foot

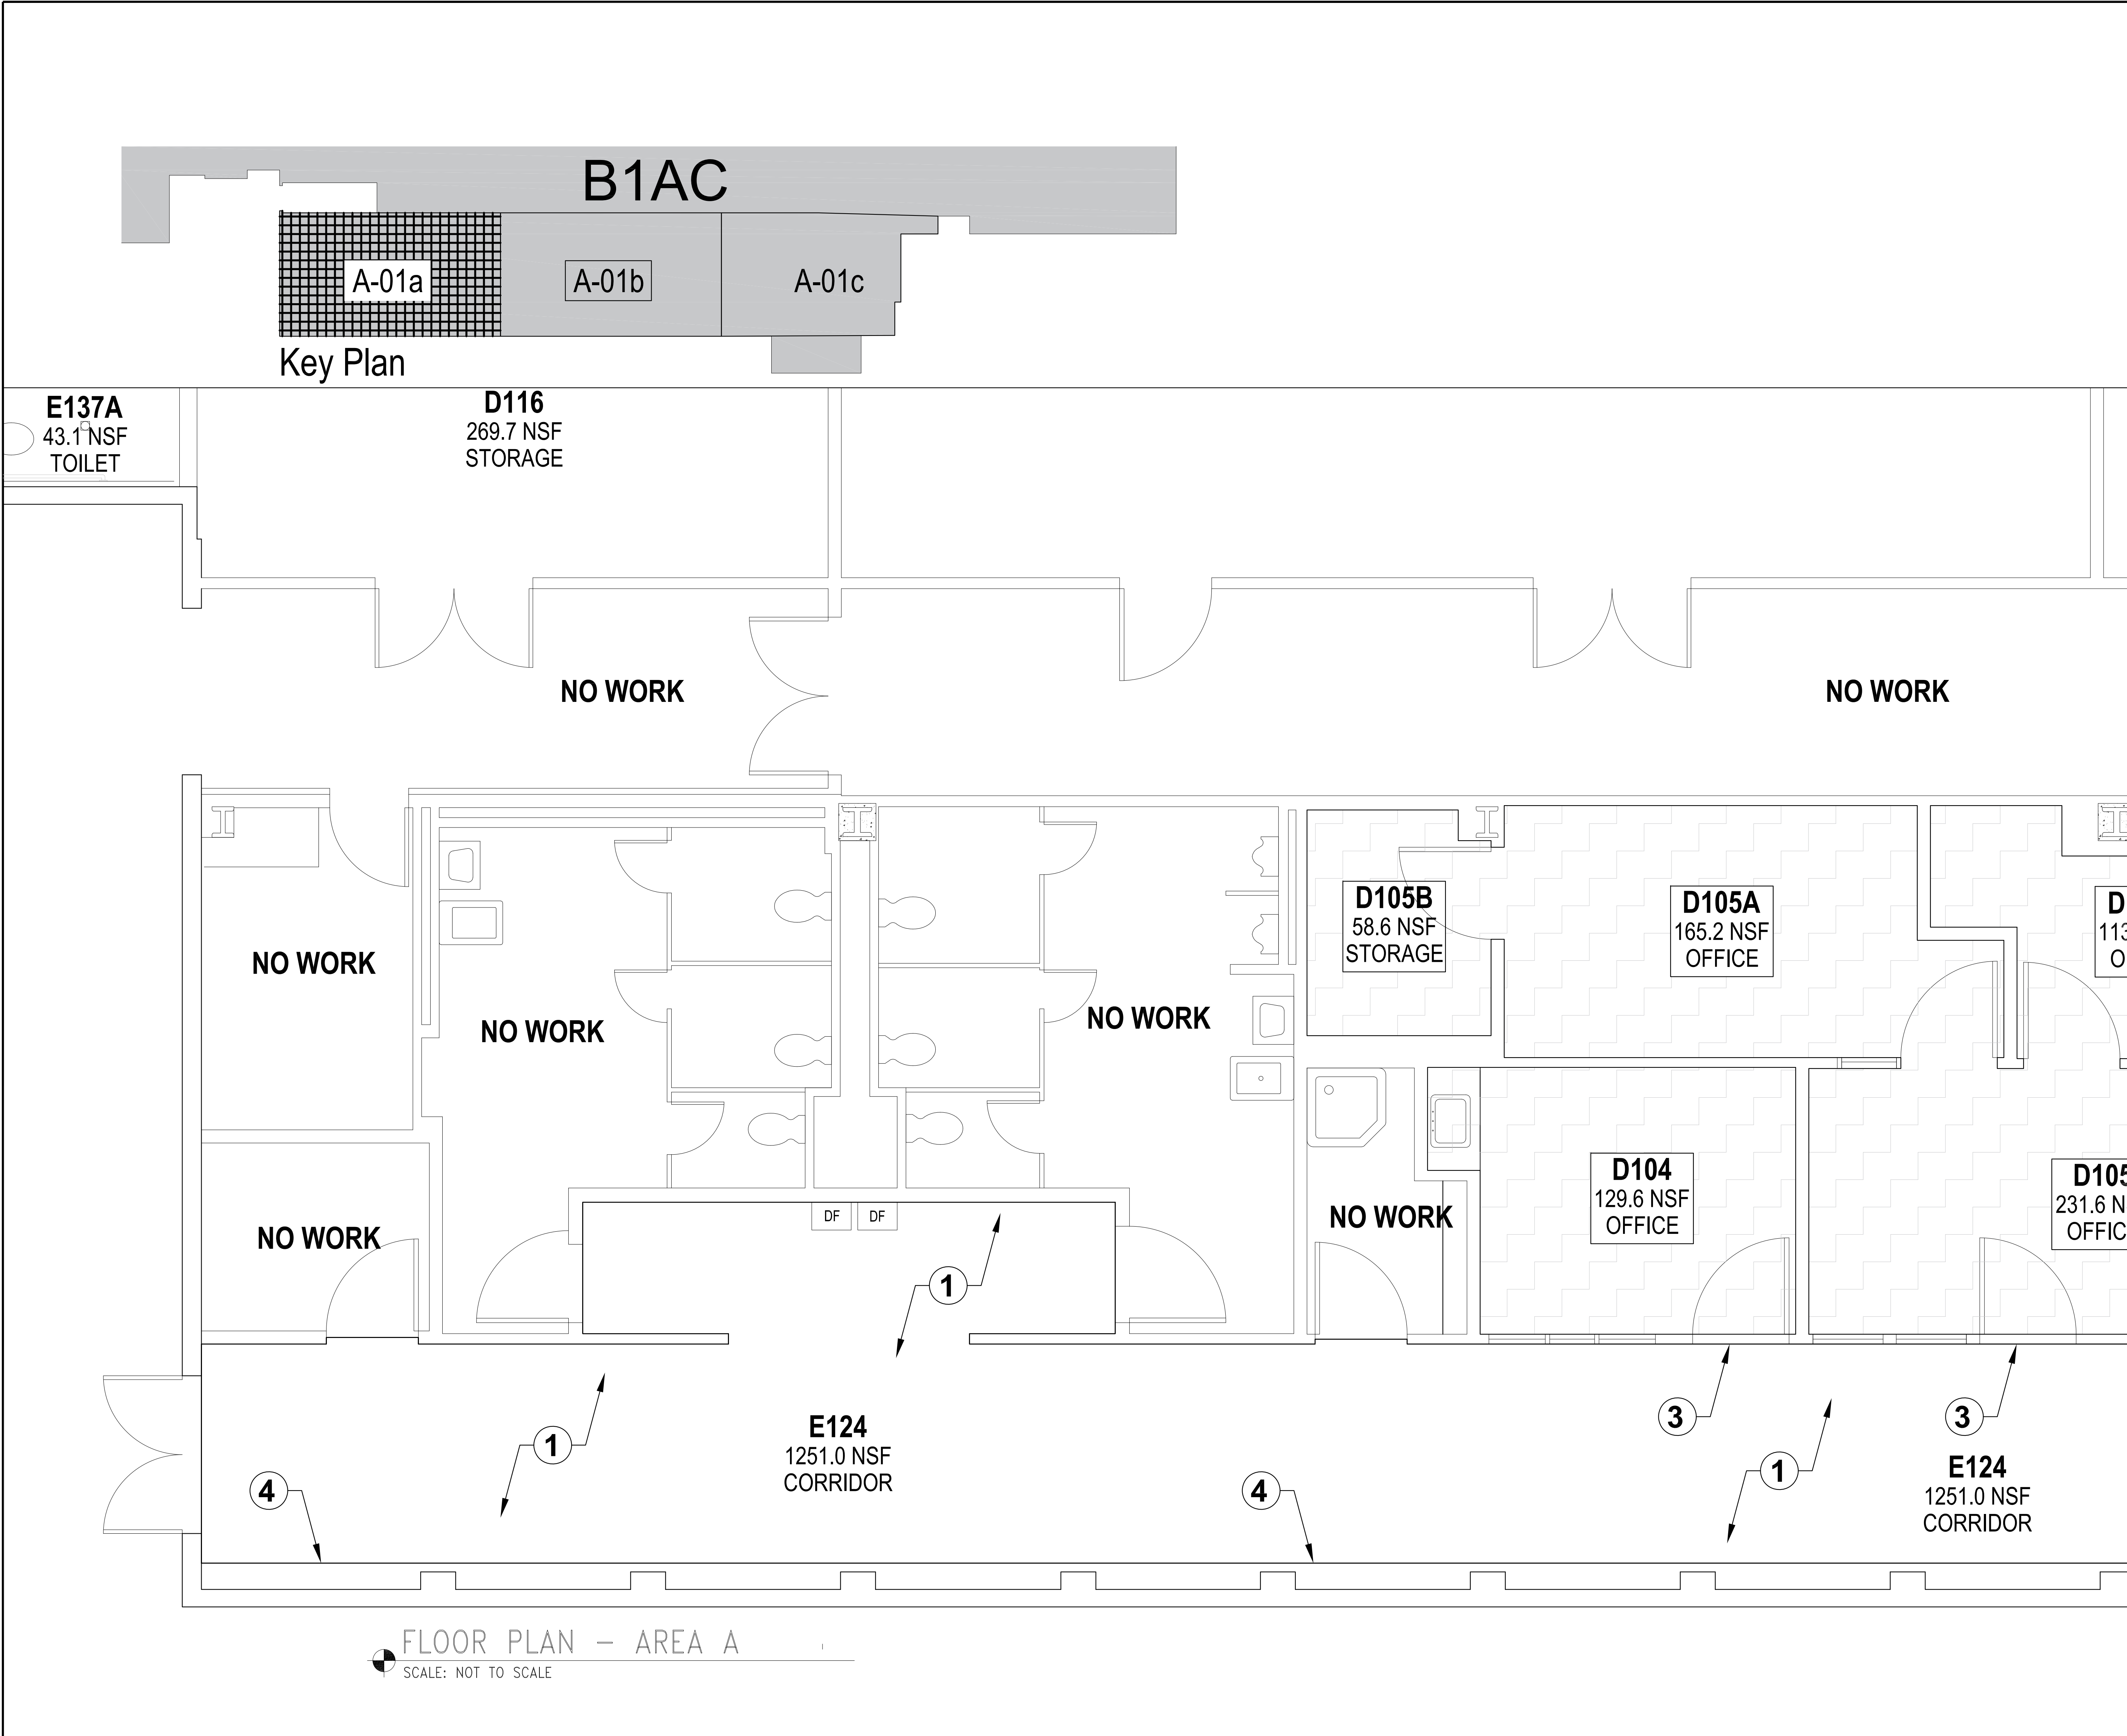


- GENERAL NOTES:
- THESE PLANS DELINEATE THE BASIC SCOPE OF WORK FOR THE REMOVAL OF EXISTING MATERIAL. THE DRAWINGS AND NOTES ARE PROVIDED WITH THE INTENT TO GENERALLY DESCRIBE AREAS AND LIMITS OF WORK. THE CONTRACTOR SHALL BE FAMILIAR WITH THE SITE AND CONDITIONS THERE ON; AND SHALL NOT RELY SOLELY ON REVIEW OF THE BIDDING DOCUMENTS IN DETERMINING THE EXTENT OF WORK REQUIRED. COORDINATION OF THESE DRAWINGS WITH REQUIREMENTS FOR CONTRACT WORK IS THE RESPONSIBILITY OF THE CONTRACTOR. DISCREPANCIES BETWEEN OR WITHIN THE CONTRACT DOCUMENTS SHALL BE REPORTED TO THE CONTRACTING OFFICER IMMEDIATELY. THE CONTRACTOR SHALL PROVIDE CLARITY SKETCHES, DIAGRAMS, AND FIELD DIMENSIONS OF EXISTING CONDITIONS AT THE REQUEST OF THE CONTRACTING OFFICER IF/WHEN CONFLICTS ARE IDENTIFIED.
 - REMOVE ALL PIPES, VALVES, CONTROLS, WIRES, AND CABLES AND APPURTENANCES WHICH SERVE DEVICES BEING REMOVED BACK TO THEIR SOURCE
 - CONTRACTOR SHALL REVIEW ALL CONTRACT DOCUMENTS AND COORDINATE FOR ALL CUTTING, PATCHING AND FINISH WORK.
 - IT IS THE CONTRACTORS RESPONSIBILITY TO FIELD VERIFY ALL EXISTING CONDITIONS.
 - CONTRACTOR TO PATCH AND CAULK ALL PENETRATIONS FROM DEMOLITION WORK WITHIN THE PROJECT SCOPE.
 - UNO, DISCONNECT AND REMOVE ALL EXISTING DEVICES, MAINTAIN CONTINUITY OF ALL REMAINING DEVICES AND EQUIPMENT. PROVIDE JUNCTION BOXES, CONDUIT AND WIRE TO EXTEND EXISTING CIRCUITS AS REQUIRED.
 - CONTRACTOR IS RESPONSIBLE FOR MOVING, REMOVING AND REINSTALLING ITEMS AGAINST AND ON WALLS.
 - NO PORTION OF THE WORK REQUIRING A SHOP DRAWING OR SAMPLE SUBMISSION SHALL BE COMMENCED UNTIL THE SUBMISSION HAS BEEN APPROVED BY THE OWNER'S REPRESENTATIVE. ALL SUCH PORTIONS OF THE WORK SHALL BE IN ACCORDANCE WITH APPROVED SHOP DRAWINGS AND SAMPLE.
 - THE AREA NEARBY THE CONSTRUCTION SITE WILL REMAIN IN OPERATION. COORDINATE WITH THE COR TO SCHEDULE THE WORK. DEMOLITION WORK, AND NOISY WORK MAY NEED TO BE DONE AFTER NORMAL BUSINESS HOURS. THE SAFETY OF THE PUBLIC MUST BE GUARDED CAREFULLY AT ALL PHASES OF CONSTRUCTION.
 - SPRINKLER SYSTEM TO REMAIN ACTIVE IN CONSTRUCTION AREA DURING CONSTRUCTION OR CONTRACTOR TO MEET NFPA 241 BY OTHER METHODS.
 - IT IS THE CONTRACTORS RESPONSIBILITY TO MOVE FURNITURE FROM OFFICES FOR WORK TO BE ACCOMPLISHED AND TO MOVE FURNITURE BACK AFTER WORK IS COMPLETE.
 - CONTRACTOR SHALL SUBMIT A PHASING PLAN TO BE APPROVED BY THE COR PRIOR TO STARTING WORK.
 - REFER TO SPECIFICATIONS AND A-05 FOR ROOM FINISH SCHEDULE


- KEYED NOTES**
- NO FLOORING DEMO IN E124 – CORRIDOR. DEMO BASE.
 - PATTERN MATCH FLOORING AT NEW/EXISTING FLOORING TRANSITION.
 - FLOORING SEAM SHALL LAND IN THE MIDDLE OF THE DOOR IN THE CLOSED POSITION.
 - REMOVE WALL PAPER THIS WALL. SKIM COAT WALL TO RECEIVE NEW PAINT FINISH.

Legend

REMOVE FLOORING AND BASE IN AREAS INDICATED BY HATCH. PREP FLOORING AS PER SPECIFICATIONS TO RECIEVE NEW FLOORING AND BASE.

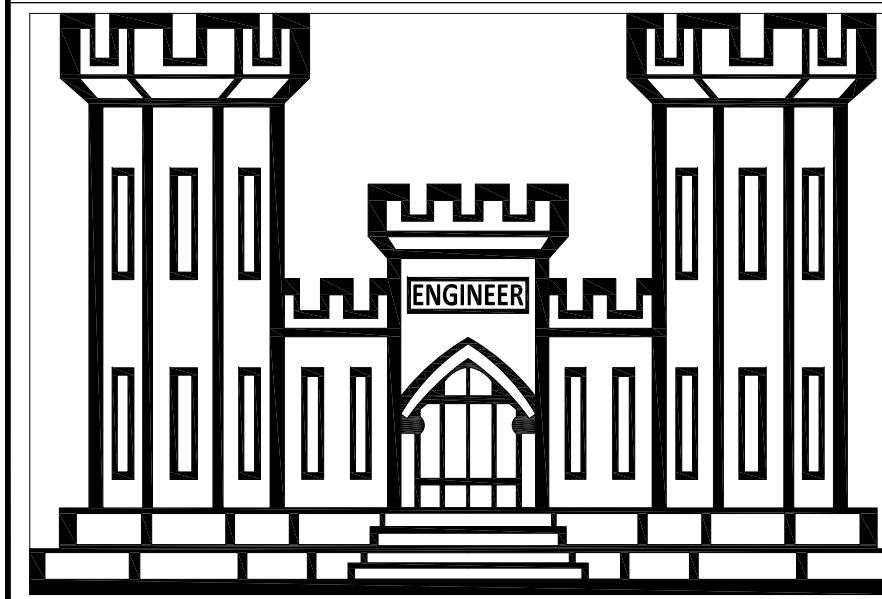	V.A. ROSEBURG HEALTHCARE SYSTEM VA VISN20	U.S. DEPARTMENT OF VETERANS AFFAIRS VA ROSEBURG HEALTHCARE SYSTEM 913 NW GARDEN VALLEY BLVD. ROSEBURG, OR. 97471 (541) 440-1000	PROFESSIONAL SEAL	BUILDING NAME: AM. CARE CLINIC – "D-WING"		PROJECT TITLE: REPLACE FINISHES B1AC "D-WING"				DRAWING TITLE: DEMO FLOOR PLAN AREA A		PROJECT NO: 653-24-103	OFFICE OF FACILITIES
				DRAWING SCALE: SCALE: NTS	LOCATION: ROSEBURG, OR	DESIGNED: MWR	CHECKED: -	REVIEWED: -	DRAFTED: MWR	BUILDING NO: 1AC	FLOOR NO: 1	SHEET NO: A-01a	


three inches = one foot
one and one half inches = one foot
one inch = one foot
three quarters inch = one foot
one half inch = one foot
three eighths inch = one foot
one quarter inch = one foot
one eighth inch = one foot

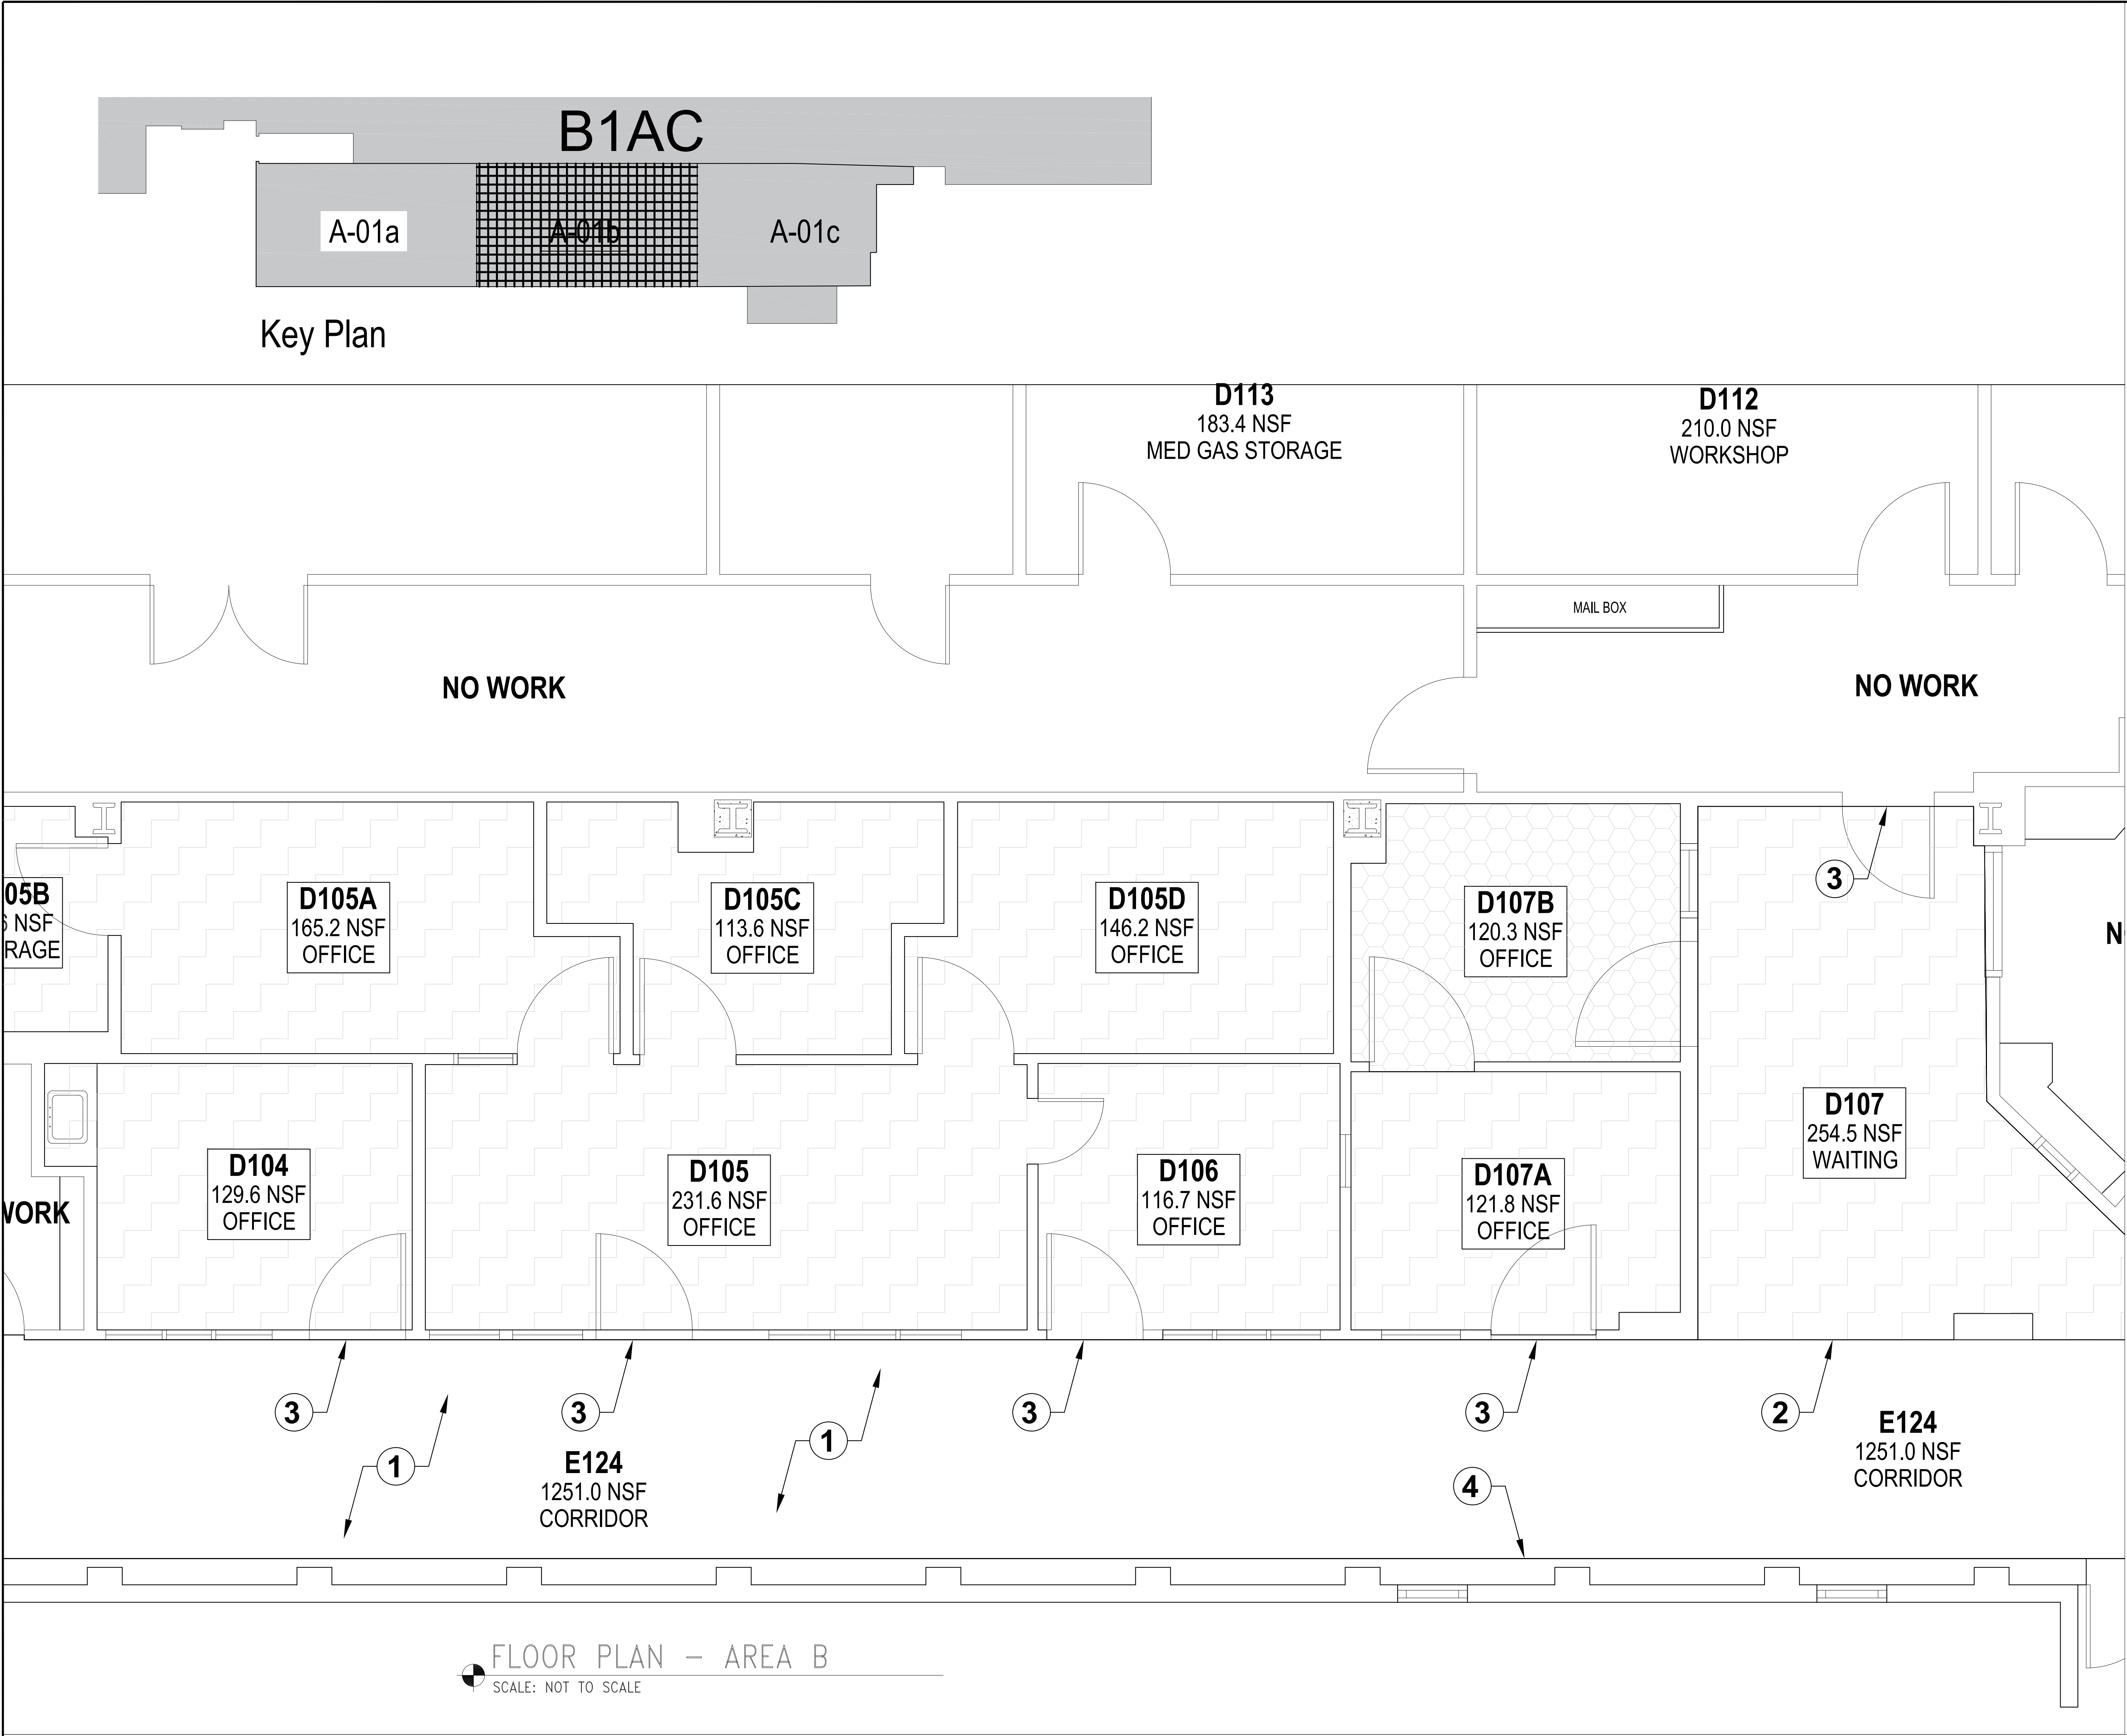


- GENERAL NOTES:
- THESE PLANS DELINEATE THE BASIC SCOPE OF WORK FOR THE REMOVAL OF EXISTING MATERIAL. THE DRAWINGS AND NOTES ARE PROVIDED WITH THE INTENT TO GENERALLY DESCRIBE AREAS AND LIMITS OF WORK. THE CONTRACTOR SHALL BE FAMILIAR WITH THE SITE AND CONDITIONS THERE ON; AND SHALL NOT RELY SOLELY ON REVIEW OF THE BIDDING DOCUMENTS IN DETERMINING THE EXTENT OF WORK REQUIRED. COORDINATION OF THESE DRAWINGS WITH REQUIREMENTS FOR CONTRACT WORK IS THE RESPONSIBILITY OF THE CONTRACTOR. DISCREPANCIES BETWEEN OR WITHIN THE CONTRACT DOCUMENTS SHALL BE REPORTED TO THE CONTRACTING OFFICER IMMEDIATELY. THE CONTRACTOR SHALL PROVIDE CLARITY SKETCHES, DIAGRAMS, AND FIELD DIMENSIONS OF EXISTING CONDITIONS AT THE REQUEST OF THE CONTRACTING OFFICER IF/WHEN CONFLICTS ARE IDENTIFIED.
 - REMOVE ALL PIPES, VALVES, CONTROLS, WIRES, AND CABLES AND APPURTENANCES WHICH SERVE DEVICES BEING REMOVED BACK TO THEIR SOURCE
 - CONTRACTOR SHALL REVIEW ALL CONTRACT DOCUMENTS AND COORDINATE FOR ALL CUTTING, PATCHING AND FINISH WORK.
 - IT IS THE CONTRACTORS RESPONSIBILITY TO FIELD VERIFY ALL EXISTING CONDITIONS.
 - CONTRACTOR TO PATCH AND CAULK ALL PENETRATIONS FROM DEMOLITION WORK WITHIN THE PROJECT SCOPE.
 - UNO, DISCONNECT AND REMOVE ALL EXISTING DEVICES, MAINTAIN CONTINUITY OF ALL REMAINING DEVICES AND EQUIPMENT. PROVIDE JUNCTION BOXES, CONDUIT AND WIRE TO EXTEND EXISTING CIRCUITS AS REQUIRED.
 - CONTRACTOR IS RESPONSIBLE FOR MOVING, REMOVING AND REINSTALLING ITEMS AGAINST AND ON WALLS.
 - NO PORTION OF THE WORK REQUIRING A SHOP DRAWING OR SAMPLE SUBMISSION SHALL BE COMMENCED UNTIL THE SUBMISSION HAS BEEN APPROVED BY THE OWNER'S REPRESENTATIVE. ALL SUCH PORTIONS OF THE WORK SHALL BE IN ACCORDANCE WITH APPROVED SHOP DRAWINGS AND SAMPLE.
 - THE AREA NEARBY THE CONSTRUCTION SITE WILL REMAIN IN OPERATION. COORDINATE WITH THE COR TO SCHEDULE THE WORK. DEMOLITION WORK, AND NOISY WORK MAY NEED TO BE DONE AFTER NORMAL BUSINESS HOURS. THE SAFETY OF THE PUBLIC MUST BE GUARDED CAREFULLY AT ALL PHASES OF CONSTRUCTION.
 - SPRINKLER SYSTEM TO REMAIN ACTIVE IN CONSTRUCTION AREA DURING CONSTRUCTION OR CONTRACTOR TO MEET NFPA 241 BY OTHER METHODS.
 - IT IS THE CONTRACTORS RESPONSIBILITY TO MOVE FURNITURE FROM OFFICES FOR WORK TO BE ACCOMPLISHED AND TO MOVE FURNITURE BACK AFTER WORK IS COMPLETE.
 - CONTRACTOR SHALL SUBMIT A PHASING PLAN TO BE APPROVED BY THE COR PRIOR TO STARTING WORK.
 - REFER TO SPECIFICATIONS AND A-05 FOR ROOM FINISH SCHEDULE.

- KEYED NOTES
- NO FLOORING DEMO IN E124 - CORRIDOR. DEMO BASE.
 - PATTERN MATCH FLOORING AT NEW/EXISTING FLOORING TRANSITION.
 - FLOORING SEAM SHALL LAND IN THE MIDDLE OF THE DOOR IN THE CLOSED POSITION.
 - REMOVE WALL PAPER THIS WALL. SKIM COAT WALL TO RECEIVE NEW PAINT FINISH.

- Legend
- REMOVE FLOORING AND BASE IN AREAS INDICATED BY HATCH. PREP FLOORING AS PER SPECIFICATIONS TO RECIEVE NEW FLOORING AND BASE.
 - REMOVE FLOORING AND BASE IN AREAS INDICATED BY HATCH. PREP FLOORING AS PER SPECIFICATIONS TO RECEIVE NEW FLOORING AND BASE. EXTENSIVE FLOOR REPAIR AND LEVELING EXPECTED IN THIS AREA.

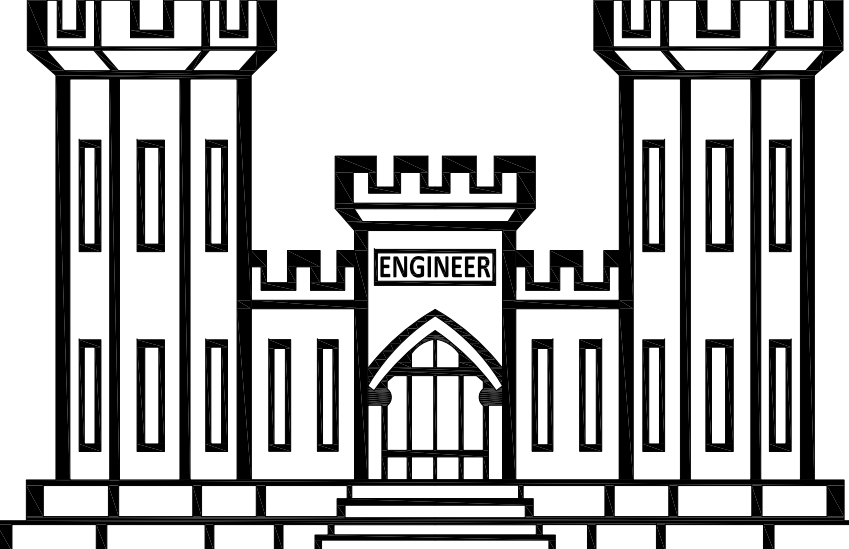 V.A. ROSEBURG HEALTHCARE SYSTEM VA VISN20	U.S. DEPARTMENT OF VETERANS AFFAIRS VA ROSEBURG HEALTHCARE SYSTEM 913 NW GARDEN VALLEY BLVD. ROSEBURG, OR. 97471 (541) 440-1000	PROFESSIONAL SEAL	BUILDING NAME: AM. CARE CLINIC - "D-WING"		PROJECT TITLE: REPLACE FINISHES B1AC "D-WING"				DRAWING TITLE: DEMO FLOOR PLAN AREA B		PROJECT NO: 653-24-103
			DRAWING SCALE: SCALE: NTS	LOCATION: ROSEBURG, OR	DESIGNED: MWR	CHECKED: -	REVIEWED: -	DRAFTED: MWR	BUILDING NO:	FLOOR NO: 1	SHEET NO: A-01b

three inches = one foot
one and one half inches = one foot
one inch = one foot
three quarters inch = one foot
one half inch = one foot
three eighths inch = one foot
one quarter inch = one foot
one eighth inch = one foot

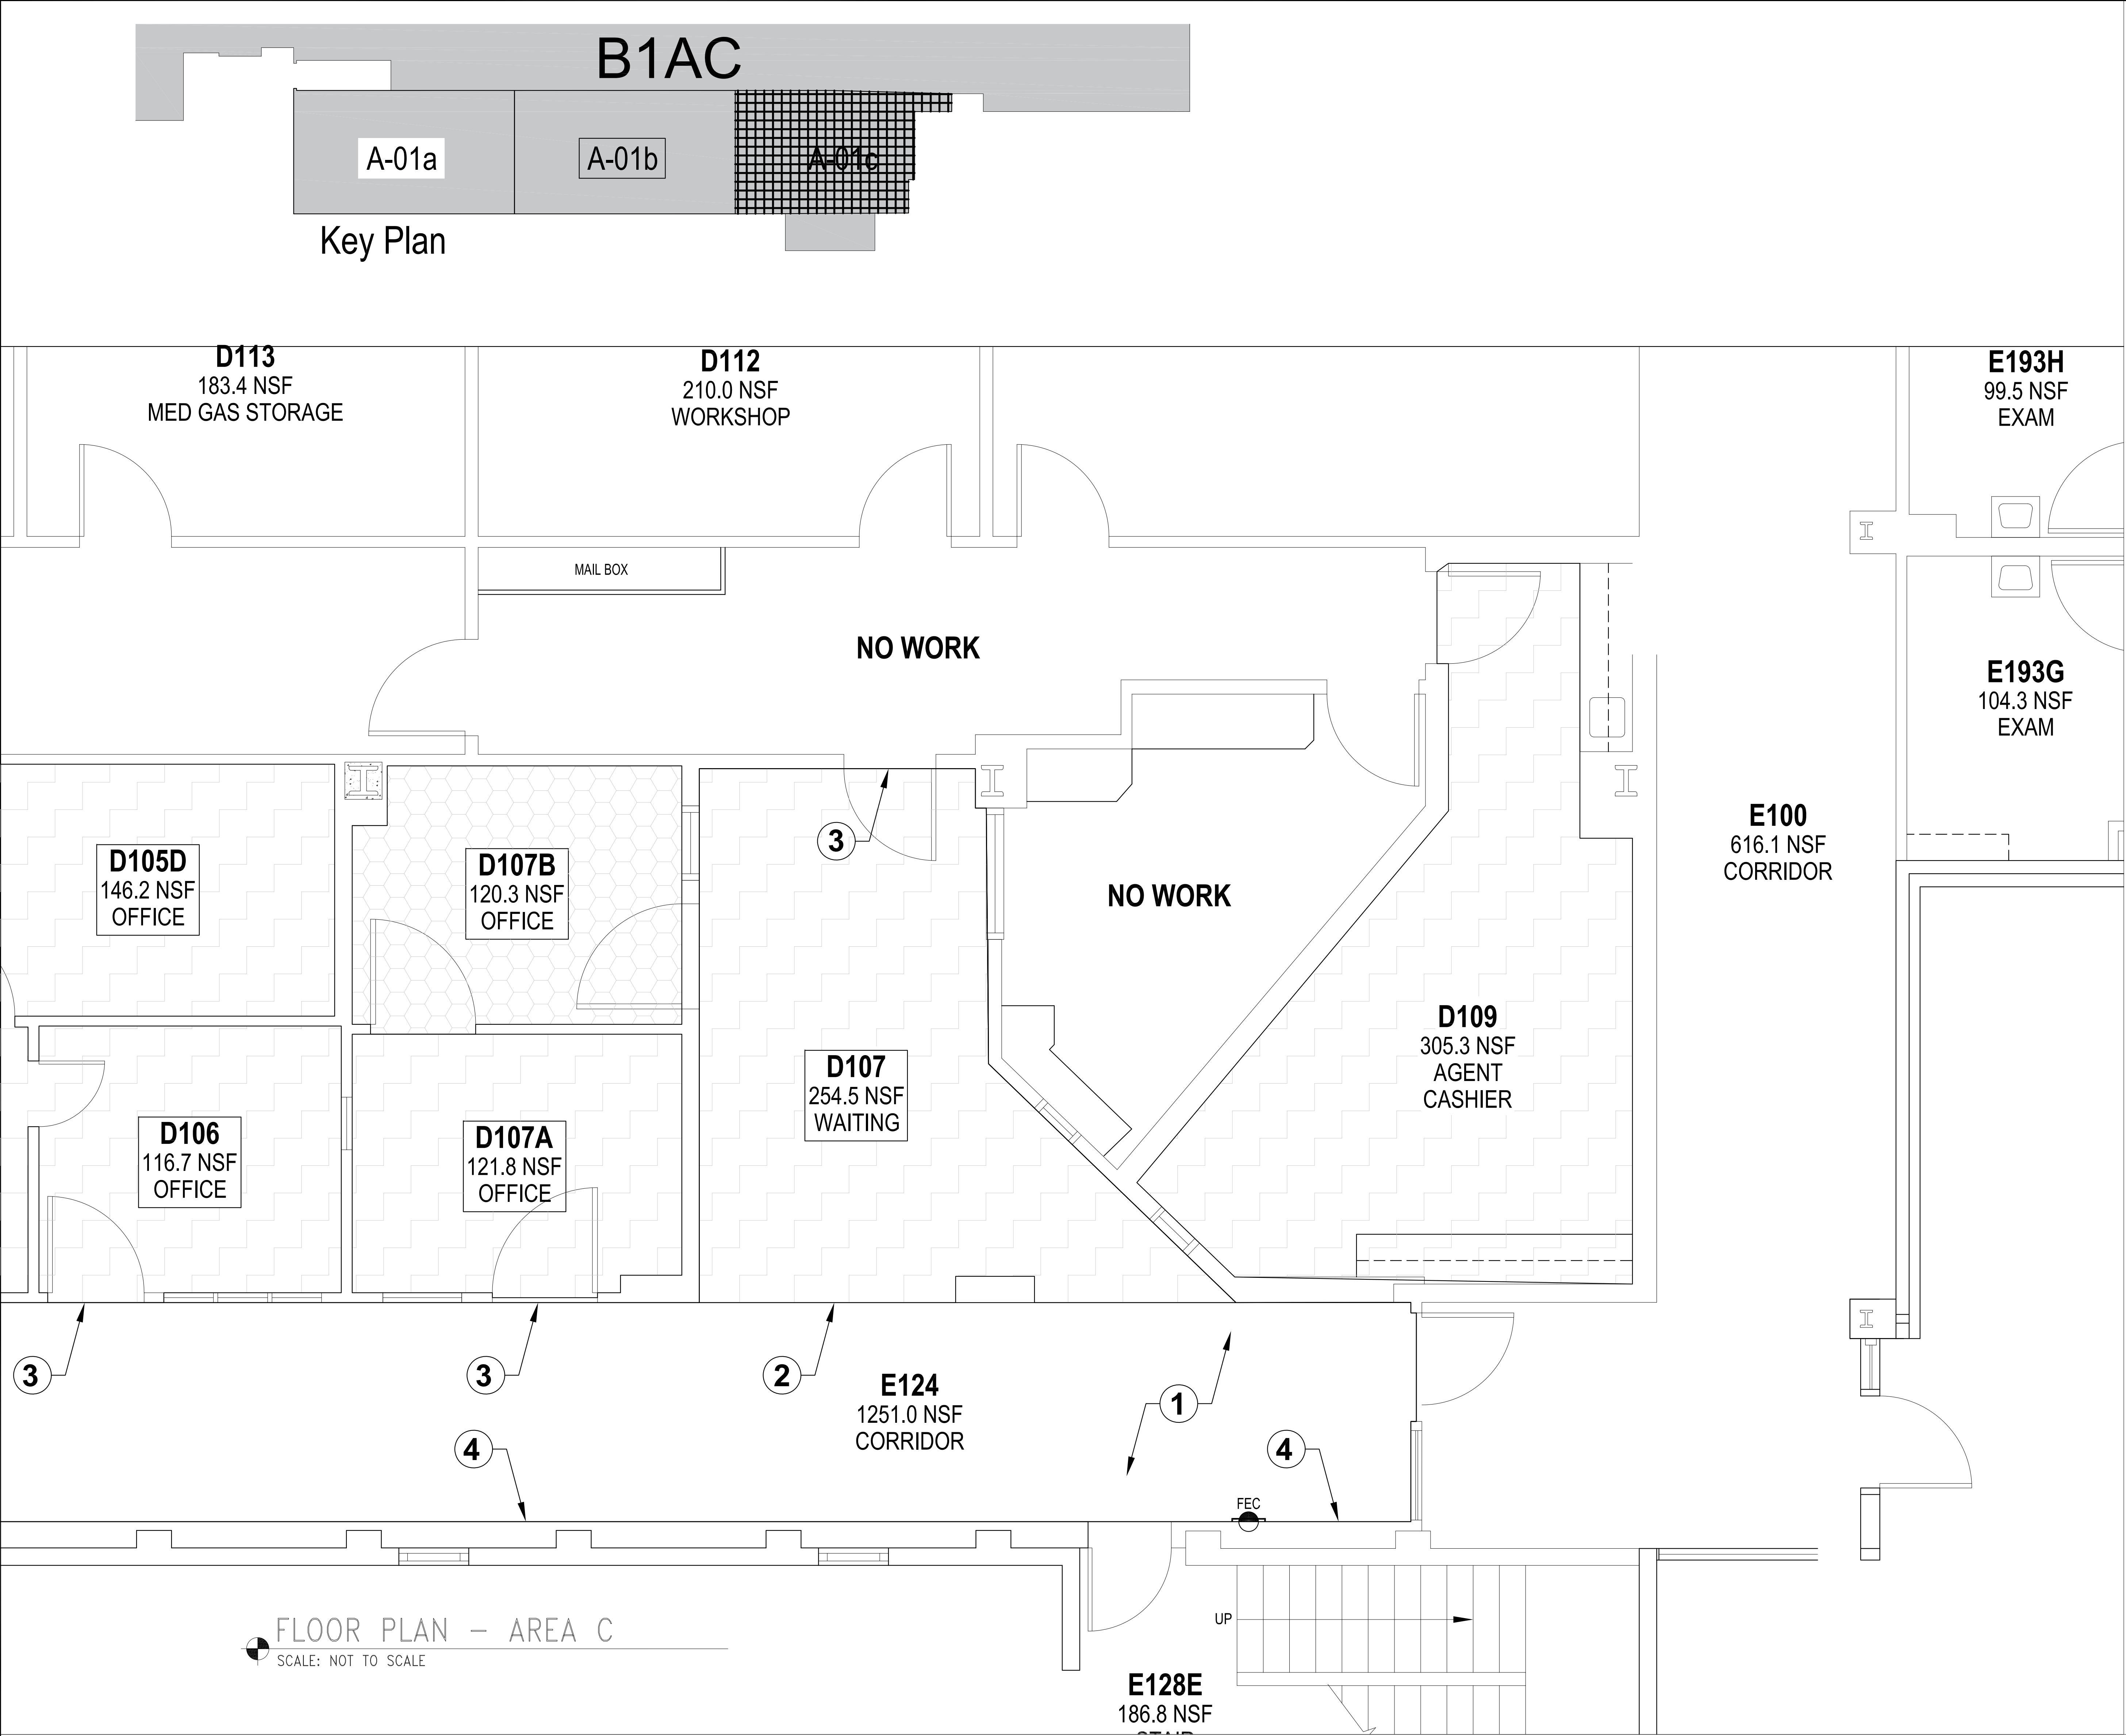

- GENERAL NOTES:
- THESE PLANS DELINEATE THE BASIC SCOPE OF WORK FOR THE REMOVAL OF EXISTING MATERIAL. THE DRAWINGS AND NOTES ARE PROVIDED WITH THE INTENT TO GENERALLY DESCRIBE AREAS AND LIMITS OF WORK. THE CONTRACTOR SHALL BE FAMILIAR WITH THE SITE AND CONDITIONS THERE ON; AND SHALL NOT RELY SOLELY ON REVIEW OF THE BIDDING DOCUMENTS IN DETERMINING THE EXTENT OF WORK REQUIRED. COORDINATION OF THESE DRAWINGS WITH REQUIREMENTS FOR CONTRACT WORK IS THE RESPONSIBILITY OF THE CONTRACTOR. DISCREPANCIES BETWEEN OR WITHIN THE CONTRACT DOCUMENTS SHALL BE REPORTED TO THE CONTRACTING OFFICER IMMEDIATELY. THE CONTRACTOR SHALL PROVIDE CLARITY SKETCHES, DIAGRAMS, AND FIELD DIMENSIONS OF EXISTING CONDITIONS AT THE REQUEST OF THE CONTRACTING OFFICER IF/WHEN CONFLICTS ARE IDENTIFIED.
 - REMOVE ALL PIPES, VALVES, CONTROLS, WIRES, AND CABLES AND APPURTENANCES WHICH SERVE DEVICES BEING REMOVED BACK TO THEIR SOURCE
 - CONTRACTOR SHALL REVIEW ALL CONTRACT DOCUMENTS AND COORDINATE FOR ALL CUTTING, PATCHING AND FINISH WORK.
 - IT IS THE CONTRACTORS RESPONSIBILITY TO FIELD VERIFY ALL EXISTING CONDITIONS.
 - CONTRACTOR TO PATCH AND CAULK ALL PENETRATIONS FROM DEMOLITION WORK WITHIN THE PROJECT SCOPE.
 - UNO, DISCONNECT AND REMOVE ALL EXISTING DEVICES, MAINTAIN CONTINUITY OF ALL REMAINING DEVICES AND EQUIPMENT. PROVIDE JUNCTION BOXES, CONDUIT AND WIRE TO EXTEND EXISTING CIRCUITS AS REQUIRED.
 - CONTRACTOR IS RESPONSIBLE FOR MOVING, REMOVING AND REINSTALLING ITEMS AGAINST AND ON WALLS.
 - NO PORTION OF THE WORK REQUIRING A SHOP DRAWING OR SAMPLE SUBMISSION SHALL BE COMMENCED UNTIL THE SUBMISSION HAS BEEN APPROVED BY THE OWNER'S REPRESENTATIVE. ALL SUCH PORTIONS OF THE WORK SHALL BE IN ACCORDANCE WITH APPROVED SHOP DRAWINGS AND SAMPLE.
 - THE AREA NEARBY THE CONSTRUCTION SITE WILL REMAIN IN OPERATION. COORDINATE WITH THE COR TO SCHEDULE THE WORK. DEMOLITION WORK, AND NOISY WORK MAY NEED TO BE DONE AFTER NORMAL BUSINESS HOURS. THE SAFETY OF THE PUBLIC MUST BE GUARDED CAREFULLY AT ALL PHASES OF CONSTRUCTION.
 - SPRINKLER SYSTEM TO REMAIN ACTIVE IN CONSTRUCTION AREA DURING CONSTRUCTION OR CONTRACTOR TO MEET NFPA 241 BY OTHER METHODS.
 - IT IS THE CONTRACTORS RESPONSIBILITY TO MOVE FURNITURE FROM OFFICES FOR WORK TO BE ACCOMPLISHED AND TO MOVE FURNITURE BACK AFTER WORK IS COMPLETE.
 - CONTRACTOR SHALL SUBMIT A PHASING PLAN TO BE APPROVED BY THE COR PRIOR TO STARTING WORK.
 - REFER TO SPECIFICATIONS AND A-05 FOR ROOM FINISH SCHEDULE.

- KEYED NOTES
- NO FLOORING DEMO IN E124 - CORRIDOR. DEMO BASE
 - PATTERN MATCH FLOORING AT NEW/EXISTING FLOORING TRANSITION.
 - FLOORING SEAM SHALL LAND IN THE MIDDLE OF THE DOOR IN THE CLOSED POSITION.
 - REMOVE WALL PAPER THIS WALL. SKIM COAT WALL TO RECEIVE NEW PAINT FINISH.

Legend

REMOVE FLOORING AND BASE IN AREAS INDICATED BY HATCH. PREP FLOORING AS PER SPECIFICATIONS TO RECIEVE NEW FLOORING AND BASE.

V.A. ROSEBURG
HEALTHCARE SYSTEM

VA

VISN20

U.S. DEPARTMENT OF VETERANS AFFAIRS
VA ROSEBURG HEALTHCARE SYSTEM
913 NW GARDEN VALLEY BLVD.
ROSEBURG, OR. 97471
(541) 440-1000

PROFESSIONAL SEAL

BUILDING NAME:
AM. CARE CLINIC - "D-WING"

DRAWING SCALE:
SCALE: NTS

LOCATION:
ROSEBURG, OR

PROJECT TITLE:
REPLACE FINISHES B1AC
"D-WING"

DESIGNED: MWR
CHECKED: -
REVIEWED: -
DRAFTED: MWR

DRAWING TITLE:
DEMO FLOOR PLAN
AREA C

BUILDING NO: 86
FLOOR NO: 1


PROJECT NO:
653-24-103

DATE:
5/18/2022

SHEET NO:
A-01c

OFFICE OF
FACILITIES


three inches = one foot
one and one half inches = one foot
one inch = one foot
three quarters inch = one foot
one half inch = one foot
three eighths inch = one foot
one quarter inch = one foot
one eighth inch = one foot

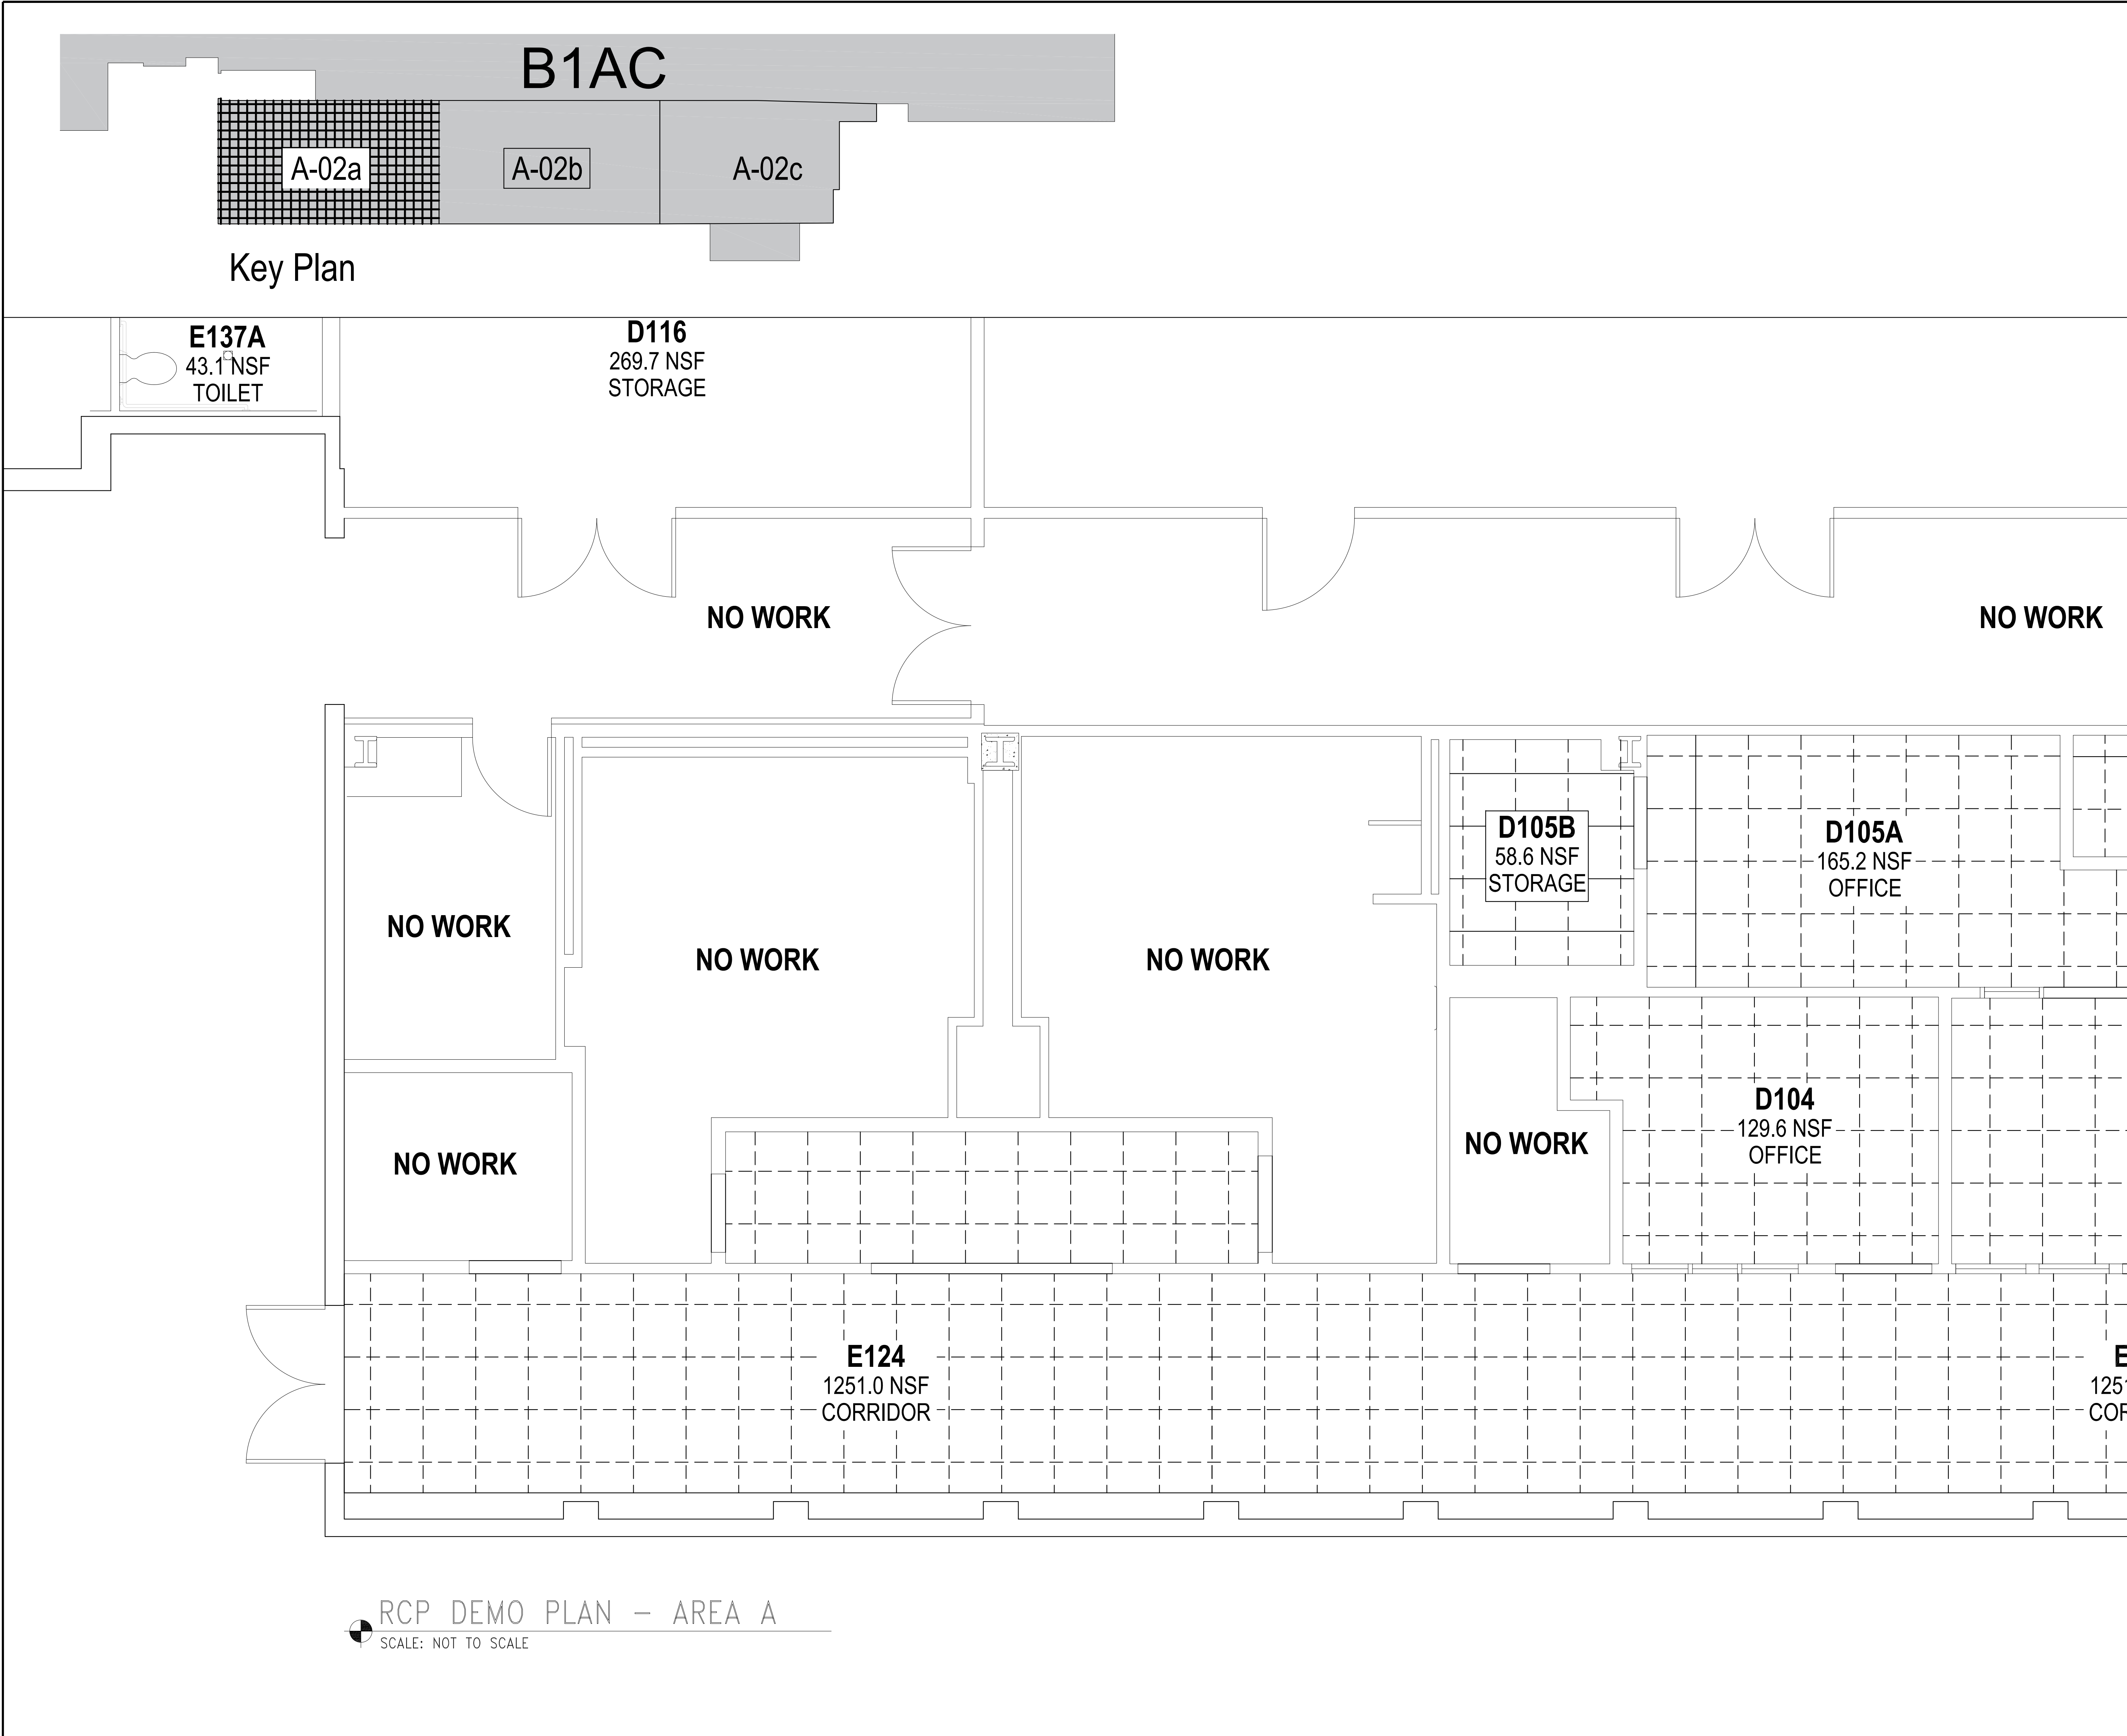


- GENERAL NOTES:
- THESE PLANS DELINEATE THE BASIC SCOPE OF WORK FOR THE REMOVAL OF EXISTING MATERIAL. THE DRAWINGS AND NOTES ARE PROVIDED WITH THE INTENT TO GENERALLY DESCRIBE AREAS AND LIMITS OF WORK. THE CONTRACTOR SHALL BE FAMILIAR WITH THE SITE AND CONDITIONS THERE ON; AND SHALL NOT RELY SOLELY ON REVIEW OF THE BIDDING DOCUMENTS IN DETERMINING THE EXTENT OF WORK REQUIRED. COORDINATION OF THESE DRAWINGS WITH REQUIREMENTS FOR CONTRACT WORK IS THE RESPONSIBILITY OF THE CONTRACTOR. DISCREPANCIES BETWEEN OR WITHIN THE CONTRACT DOCUMENTS SHALL BE REPORTED TO THE CONTRACTING OFFICER IMMEDIATELY. THE CONTRACTOR SHALL PROVIDE CLARITY SKETCHES, DIAGRAMS, AND FIELD DIMENSIONS OF EXISTING CONDITIONS AT THE REQUEST OF THE CONTRACTING OFFICER IF/WHEN CONFLICTS ARE IDENTIFIED.
 - REMOVE ALL PIPES, VALVES, CONTROLS, WIRES, AND CABLES AND APPURTENANCES WHICH SERVE DEVICES BEING REMOVED BACK TO THEIR SOURCE
 - CONTRACTOR SHALL REVIEW ALL CONTRACT DOCUMENTS AND COORDINATE FOR ALL CUTTING, PATCHING AND FINISH WORK.
 - IT IS THE CONTRACTORS RESPONSIBILITY TO FIELD VERIFY ALL EXISTING CONDITIONS.
 - CONTRACTOR TO PATCH AND CAULK ALL PENETRATIONS FROM DEMOLITION WORK WITHIN THE PROJECT SCOPE.
 - UNO, DISCONNECT AND REMOVE ALL EXISTING DEVICES, MAINTAIN CONTINUITY OF ALL REMAINING DEVICES AND EQUIPMENT. PROVIDE JUNCTION BOXES, CONDUIT AND WIRE TO EXTEND EXISTING CIRCUITS AS REQUIRED.
 - CONTRACTOR IS RESPONSIBLE FOR MOVING, REMOVING AND REINSTALLING ITEMS AGAINST AND ON WALLS.
 - NO PORTION OF THE WORK REQUIRING A SHOP DRAWING OR SAMPLE SUBMISSION SHALL BE COMMENCED UNTIL THE SUBMISSION HAS BEEN APPROVED BY THE OWNER'S REPRESENTATIVE. ALL SUCH PORTIONS OF THE WORK SHALL BE IN ACCORDANCE WITH APPROVED SHOP DRAWINGS AND SAMPLE.
 - THE AREA NEARBY THE CONSTRUCTION SITE WILL REMAIN IN OPERATION. COORDINATE WITH THE COR TO SCHEDULE THE WORK. DEMOLITION WORK, AND NOISY WORK MAY NEED TO BE DONE AFTER NORMAL BUSINESS HOURS. THE SAFETY OF THE PUBLIC MUST BE GUARDED CAREFULLY AT ALL PHASES OF CONSTRUCTION.
 - SPRINKLER SYSTEM TO REMAIN ACTIVE IN CONSTRUCTION AREA DURING CONSTRUCTION OR CONTRACTOR TO MEET NFPA 241 BY OTHER METHODS.
 - REFER TO SPECIFICATIONS AND A-05 FOR ROOM FINISH SCHEDULE.

Legend

	DEMO ACT CEILING AND GRID. LIGHTS, HVAC SUPPLY AND RETURN REGISTERS AND ALL OTHER CEILING MOUNTED ACCESSORIES SHALL REMAIN TO BE REINSTALLED IN NEW CEILING GRID.
--	---

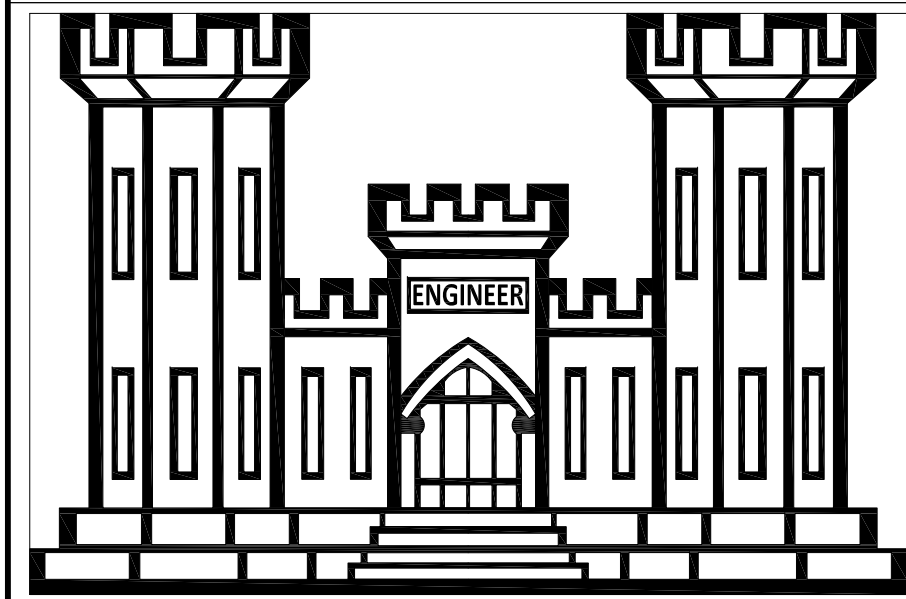	V.A. ROSEBURG HEALTHCARE SYSTEM VA VISN20	U.S. DEPARTMENT OF VETERANS AFFAIRS VA ROSEBURG HEALTHCARE SYSTEM 913 NW GARDEN VALLEY BLVD. ROSEBURG, OR. 97471 (541) 440-1000	PROFESSIONAL SEAL	BUILDING NAME: AM. CARE CLINIC - "D-WING"		PROJECT TITLE: REPLACE FINISHES B1AC "D-WING"				DRAWING TITLE: RCP DEMO PLAN AREA A		PROJECT NO: 653-24-103	OFFICE OF FACILITIES
				DRAWING SCALE: SCALE: NTS	LOCATION: ROSEBURG, OR	DESIGNED: MWR	CHECKED: -	REVIEWED: -	DRAFTED: MWR	BUILDING NO: 1AC	FLOOR NO: 1	SHEET NO: A-02a	


three inches = one foot
one and one half inches = one foot
one inch = one foot
three quarters inch = one foot
one half inch = one foot
one quarter inch = one foot
one eighth inch = one foot
one eighth inch = one foot

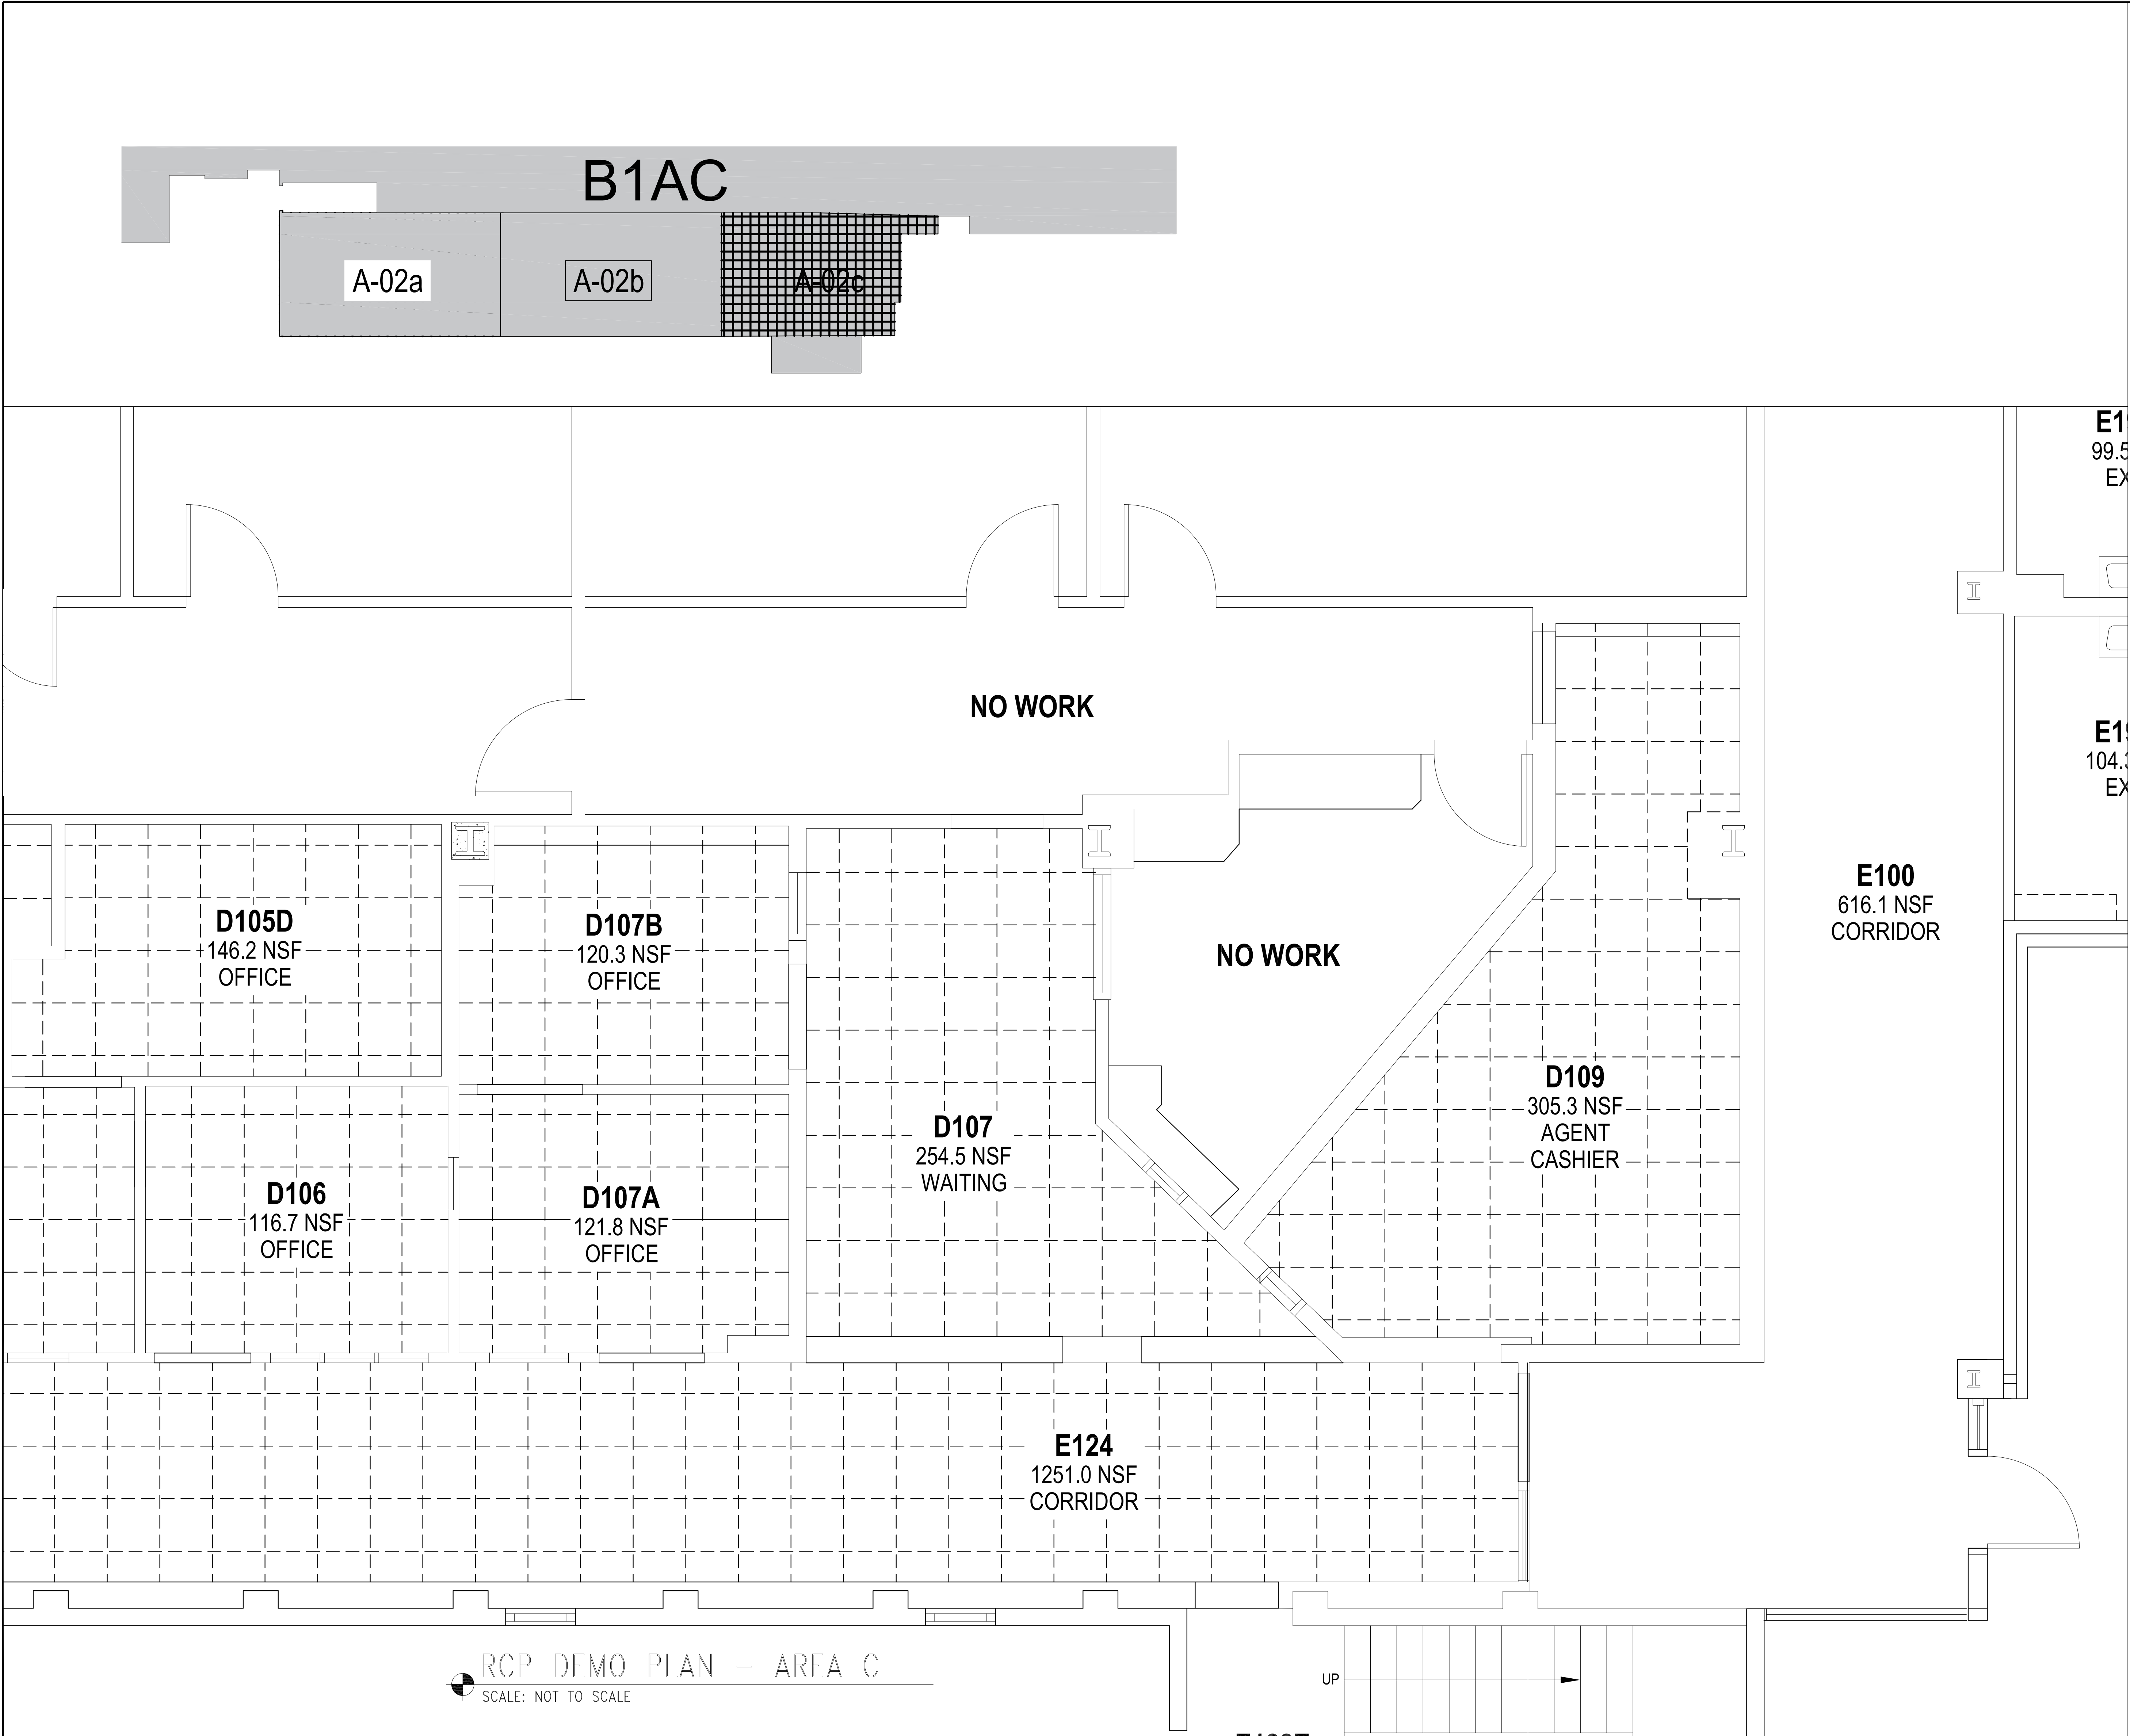

- GENERAL NOTES:
- THESE PLANS DELINEATE THE BASIC SCOPE OF WORK FOR THE REMOVAL OF EXISTING MATERIAL. THE DRAWINGS AND NOTES ARE PROVIDED WITH THE INTENT TO GENERALLY DESCRIBE AREAS AND LIMITS OF WORK. THE CONTRACTOR SHALL BE FAMILIAR WITH THE SITE AND CONDITIONS THERE ON; AND SHALL NOT RELY SOLELY ON REVIEW OF THE BIDDING DOCUMENTS IN DETERMINING THE EXTENT OF WORK REQUIRED. COORDINATION OF THESE DRAWINGS WITH REQUIREMENTS FOR CONTRACT WORK IS THE RESPONSIBILITY OF THE CONTRACTOR. DISCREPANCIES BETWEEN OR WITHIN THE CONTRACT DOCUMENTS SHALL BE REPORTED TO THE CONTRACTING OFFICER IMMEDIATELY. THE CONTRACTOR SHALL PROVIDE CLARITY SKETCHES, DIAGRAMS, AND FIELD DIMENSIONS OF EXISTING CONDITIONS AT THE REQUEST OF THE CONTRACTING OFFICER IF/WHEN CONFLICTS ARE IDENTIFIED.
 - REMOVE ALL PIPES, VALVES, CONTROLS, WIRES, AND CABLES AND APPURTENANCES WHICH SERVE DEVICES BEING REMOVED BACK TO THEIR SOURCE
 - CONTRACTOR SHALL REVIEW ALL CONTRACT DOCUMENTS AND COORDINATE FOR ALL CUTTING, PATCHING AND FINISH WORK.
 - IT IS THE CONTRACTORS RESPONSIBILITY TO FIELD VERIFY ALL EXISTING CONDITIONS.
 - CONTRACTOR TO PATCH AND CAULK ALL PENETRATIONS FROM DEMOLITION WORK WITHIN THE PROJECT SCOPE.
 - UNO, DISCONNECT AND REMOVE ALL EXISTING DEVICES, MAINTAIN CONTINUITY OF ALL REMAINING DEVICES AND EQUIPMENT. PROVIDE JUNCTION BOXES, CONDUIT AND WIRE TO EXTEND EXISTING CIRCUITS AS REQUIRED.
 - CONTRACTOR IS RESPONSIBLE FOR MOVING, REMOVING AND REINSTALLING ITEMS AGAINST AND ON WALLS.
 - NO PORTION OF THE WORK REQUIRING A SHOP DRAWING OR SAMPLE SUBMISSION SHALL BE COMMENCED UNTIL THE SUBMISSION HAS BEEN APPROVED BY THE OWNER'S REPRESENTATIVE. ALL SUCH PORTIONS OF THE WORK SHALL BE IN ACCORDANCE WITH APPROVED SHOP DRAWINGS AND SAMPLE.
 - THE AREA NEARBY THE CONSTRUCTION SITE WILL REMAIN IN OPERATION. COORDINATE WITH THE COR TO SCHEDULE THE WORK. DEMOLITION WORK, AND NOISY WORK MAY NEED TO BE DONE AFTER NORMAL BUSINESS HOURS. THE SAFETY OF THE PUBLIC MUST BE GUARDED CAREFULLY AT ALL PHASES OF CONSTRUCTION.
 - SPRINKLER SYSTEM TO REMAIN ACTIVE IN CONSTRUCTION AREA DURING CONSTRUCTION OR CONTRACTOR TO MEET NFPA 241 BY OTHER METHODS.
 - REFER TO SPECIFICATIONS AND A-05 FOR ROOM FINISH SCHEDULE.

Legend

	DEMO ACT CEILING AND GRID. LIGHTS, HVAC SUPPLY AND RETURN REGISTERS AND ALL OTHER CEILING MOUNTED ACCESSORIES SHALL REMAIN TO BE REINSTALLED IN NEW CEILING GRID.
--	---

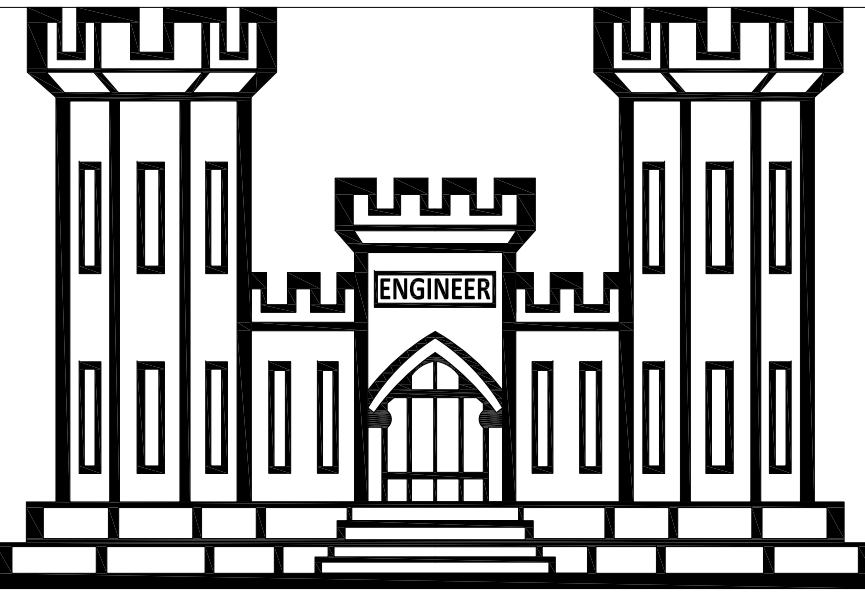

V.A. ROSEBURG
HEALTHCARE SYSTEM

VA

VISN20

U.S. DEPARTMENT OF VETERANS AFFAIRS
VA ROSEBURG HEALTHCARE SYSTEM
913 NW GARDEN VALLEY BLVD.
ROSEBURG, OR. 97471
(541) 440-1000

PROFESSIONAL SEAL

BUILDING NAME:
AM. CARE CLINIC - "D-WING"

DRAWING SCALE:
SCALE: NTS

LOCATION:
ROSEBURG, OR

PROJECT TITLE:
REPLACE FINISHES B1AC
"D-WING"

DESIGNED:
MWR

CHECKED:
-

REVIEWED:
-

DRAFTED:
MWR

DRAWING TITLE:
RCP DEMO PLAN
AREA A

BUILDING NO:
1AC

FLOOR NO:
1

PROJECT NO:
653-24-103


DATE:
5/18/2023

SHEET NO:
A-02c

OFFICE OF
FACILITIES

VA FORM 08-6231, OCT 1978

three inches = one foot
one and one half inches = one foot
one inch = one foot
three quarters inch = one foot
one half inch = one foot
three eighths inch = one foot
one quarter inch = one foot
one eighth inch = one foot

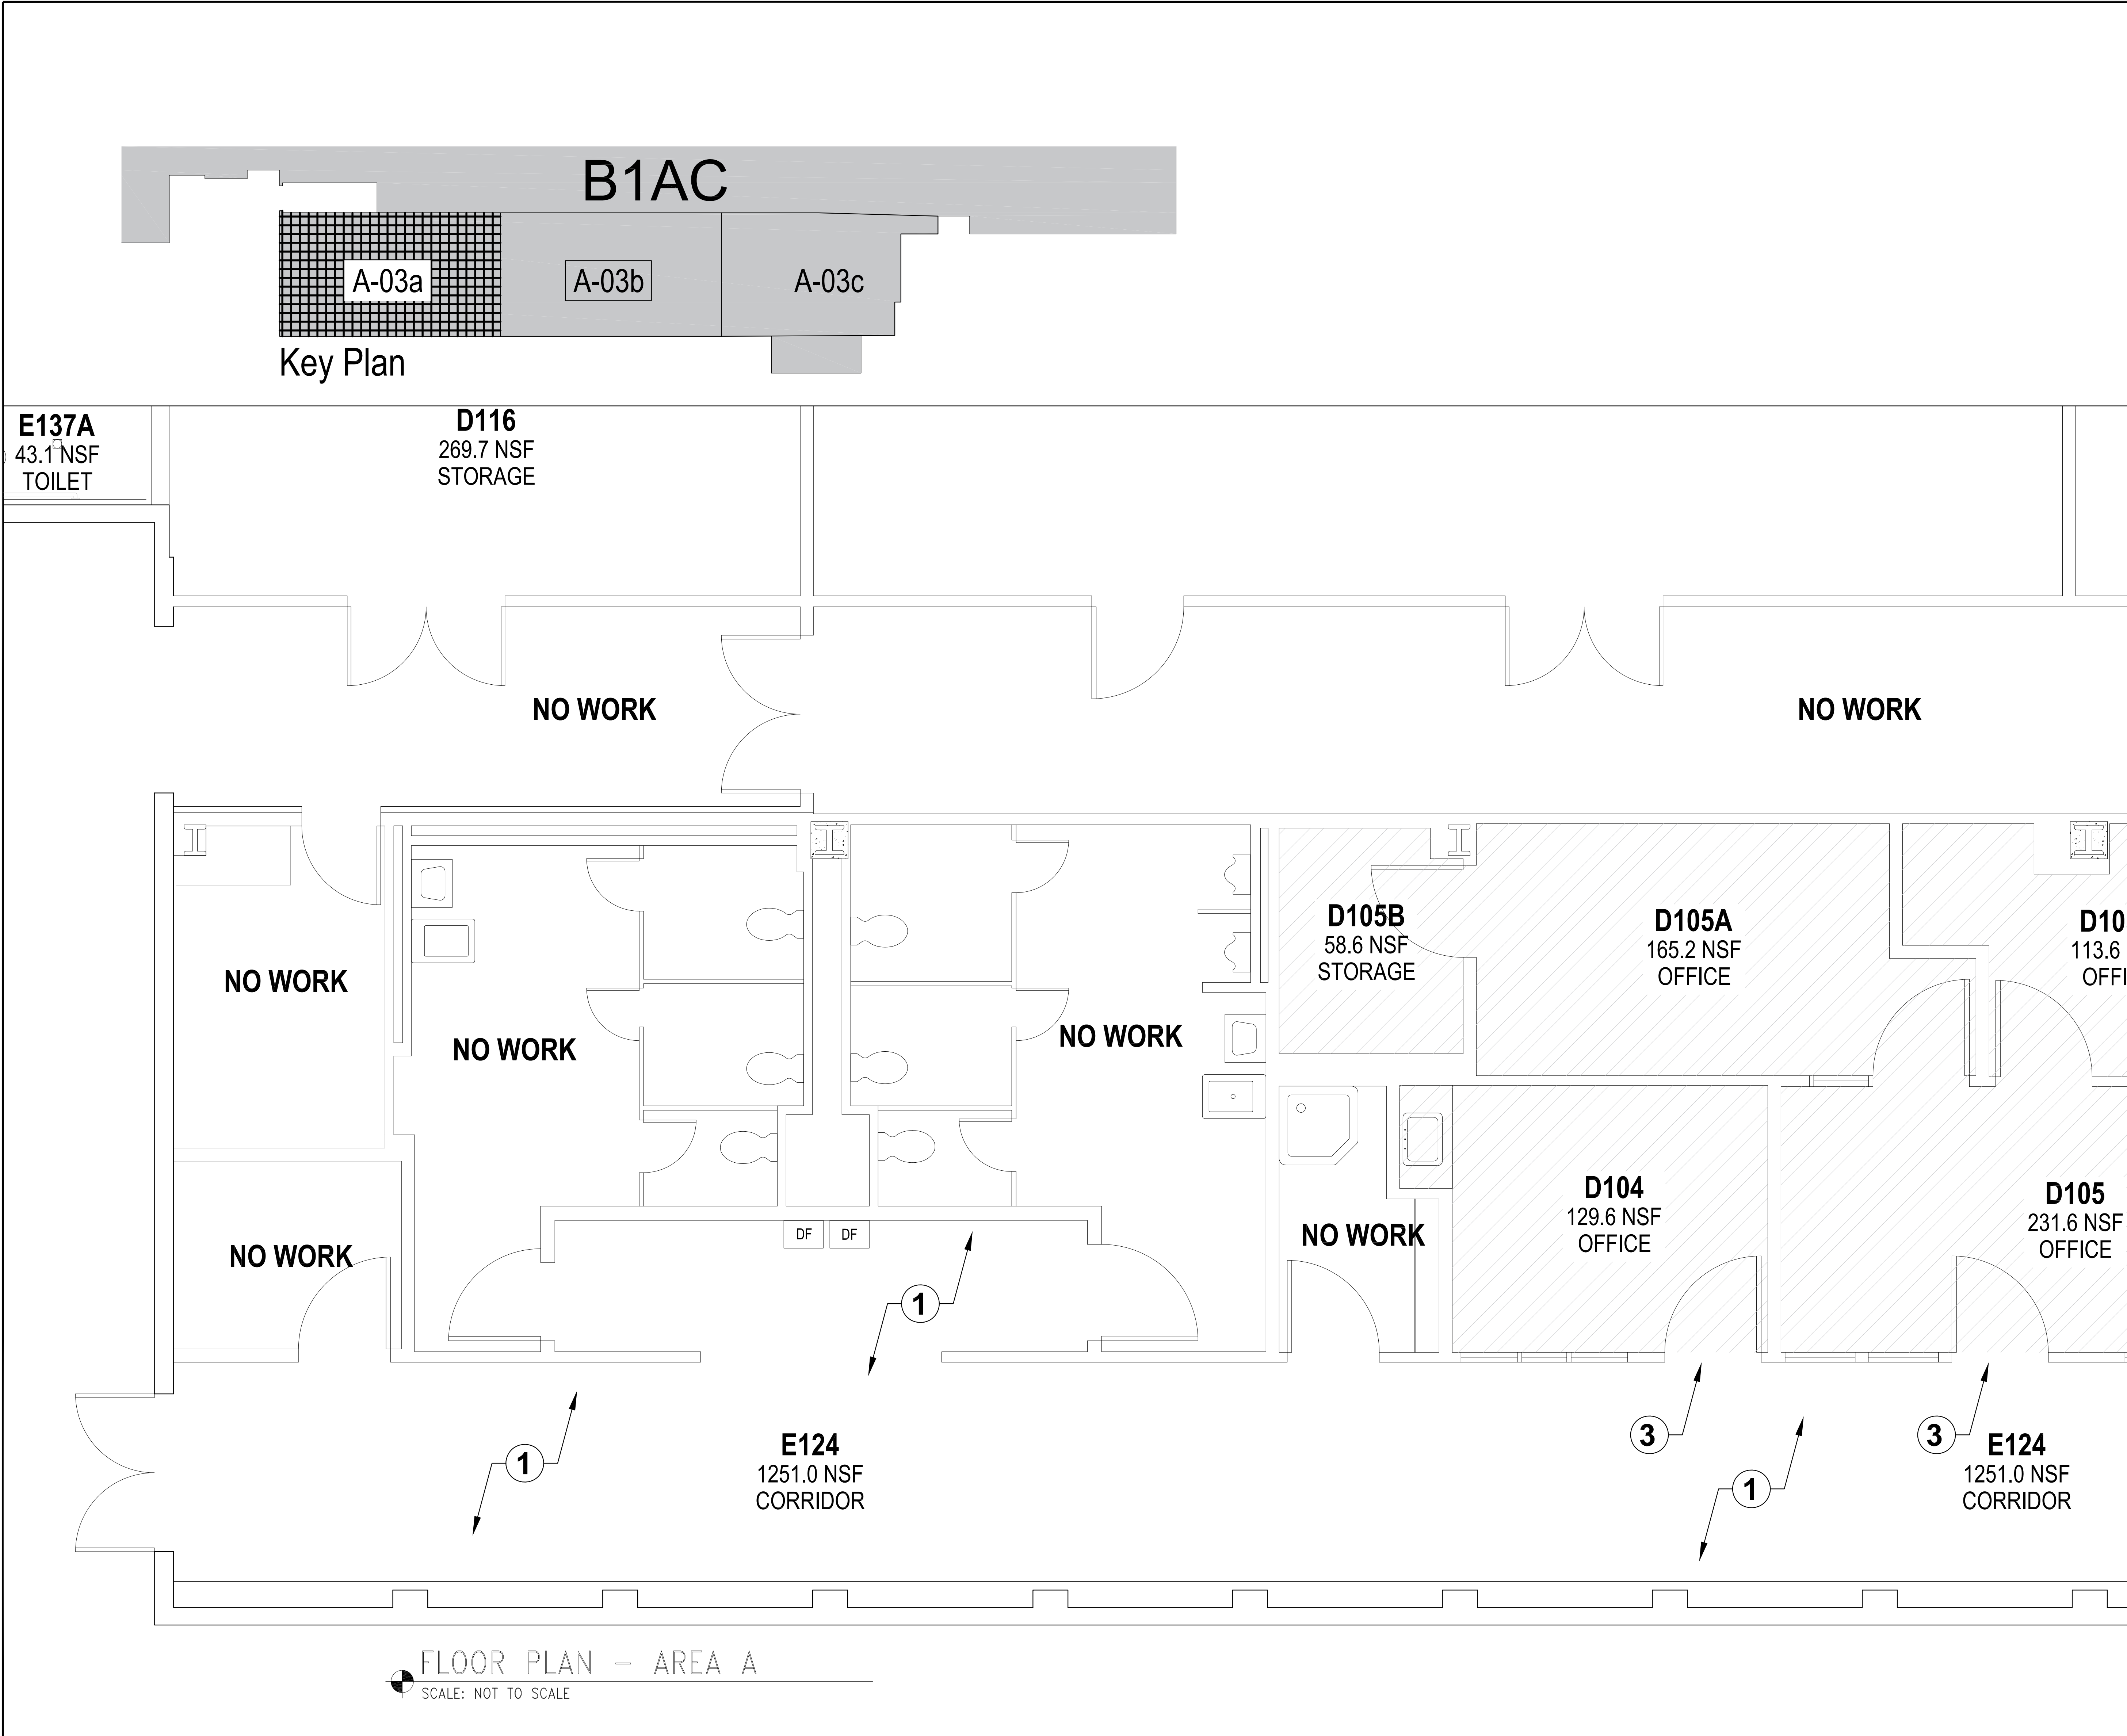


- GENERAL NOTES:
- THESE PLANS DELINEATE THE BASIC SCOPE OF WORK FOR THE REMOVAL OF EXISTING MATERIAL. THE DRAWINGS AND NOTES ARE PROVIDED WITH THE INTENT TO GENERALLY DESCRIBE AREAS AND LIMITS OF WORK. THE CONTRACTOR SHALL BE FAMILIAR WITH THE SITE AND CONDITIONS THERE ON; AND SHALL NOT RELY SOLELY ON REVIEW OF THE BIDDING DOCUMENTS IN DETERMINING THE EXTENT OF WORK REQUIRED. COORDINATION OF THESE DRAWINGS WITH REQUIREMENTS FOR CONTRACT WORK IS THE RESPONSIBILITY OF THE CONTRACTOR. DISCREPANCIES BETWEEN OR WITHIN THE CONTRACT DOCUMENTS SHALL BE REPORTED TO THE CONTRACTING OFFICER IMMEDIATELY. THE CONTRACTOR SHALL PROVIDE CLARITY SKETCHES, DIAGRAMS, AND FIELD DIMENSIONS OF EXISTING CONDITIONS AT THE REQUEST OF THE CONTRACTING OFFICER IF/WHEN CONFLICTS ARE IDENTIFIED.
 - REMOVE ALL PIPES, VALVES, CONTROLS, WIRES, AND CABLES AND APPURTENANCES WHICH SERVE DEVICES BEING REMOVED BACK TO THEIR SOURCE
 - CONTRACTOR SHALL REVIEW ALL CONTRACT DOCUMENTS AND COORDINATE FOR ALL CUTTING, PATCHING AND FINISH WORK.
 - IT IS THE CONTRACTORS RESPONSIBILITY TO FIELD VERIFY ALL EXISTING CONDITIONS.
 - CONTRACTOR TO PATCH AND CAULK ALL PENETRATIONS FROM DEMOLITION WORK WITHIN THE PROJECT SCOPE.
 - UNO, DISCONNECT AND REMOVE ALL EXISTING DEVICES, MAINTAIN CONTINUITY OF ALL REMAINING DEVICES AND EQUIPMENT. PROVIDE JUNCTION BOXES, CONDUIT AND WIRE TO EXTEND EXISTING CIRCUITS AS REQUIRED.
 - CONTRACTOR IS RESPONSIBLE FOR MOVING, REMOVING AND REINSTALLING ITEMS AGAINST AND ON WALLS.
 - NO PORTION OF THE WORK REQUIRING A SHOP DRAWING OR SAMPLE SUBMISSION SHALL BE COMMENCED UNTIL THE SUBMISSION HAS BEEN APPROVED BY THE OWNER'S REPRESENTATIVE. ALL SUCH PORTIONS OF THE WORK SHALL BE IN ACCORDANCE WITH APPROVED SHOP DRAWINGS AND SAMPLE.
 - THE AREA NEARBY THE CONSTRUCTION SITE WILL REMAIN IN OPERATION. COORDINATE WITH THE COR TO SCHEDULE THE WORK. DEMOLITION WORK, AND NOISY WORK MAY NEED TO BE DONE AFTER NORMAL BUSINESS HOURS. THE SAFETY OF THE PUBLIC MUST BE GUARDED CAREFULLY AT ALL PHASES OF CONSTRUCTION.
 - SPRINKLER SYSTEM TO REMAIN ACTIVE IN CONSTRUCTION AREA DURING CONSTRUCTION OR CONTRACTOR TO MEET NFPA 241 BY OTHER METHODS.
 - IT IS THE CONTRACTORS RESPONSIBILITY TO MOVE FURNITURE FROM OFFICES FOR WORK TO BE ACCOMPLISHED AND TO MOVE FURNITURE BACK AFTER WORK IS COMPLETE.
 - CONTRACTOR SHALL SUBMIT A PHASING PLAN TO BE APPROVED BY THE COR PRIOR TO STARTING WORK.
 - REFER TO SPECIFICATIONS AND A-05 FOR ROOM FINISH SCHEDULE.

KEYED NOTES


- NO NEW FLOORING IN E124 - CORRIDOR. PROVIDE NEW RESILIENT BASE.
- PATTERN MATCH FLOORING AT NEW/EXISTING FLOORING TRANSITION.
- FLOORING SEAM SHALL LAND IN THE MIDDLE OF THE DOOR IN THE CLOSED POSITION.

Legend

	PROVIDE NEW FLOORING AND BASE IN THESE LOCATIONS. SEE A05 AND SPECIFICATIONS FOR FINISH SCHEDULE.
--	---

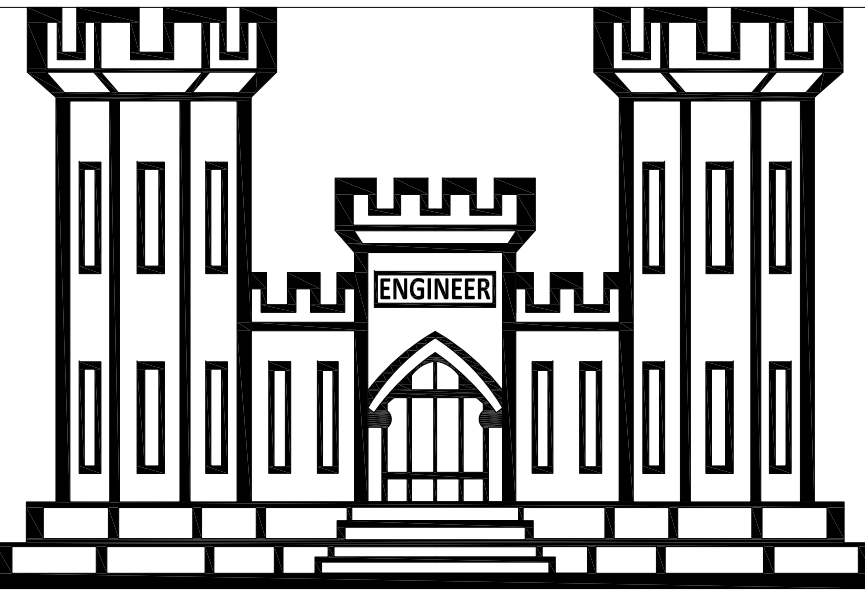 V.A. ROSEBURG HEALTHCARE SYSTEM VA VISN20	U.S. DEPARTMENT OF VETERANS AFFAIRS VA ROSEBURG HEALTHCARE SYSTEM 913 NW GARDEN VALLEY BLVD. ROSEBURG, OR. 97471 (541) 440-1000	PROFESSIONAL SEAL	BUILDING NAME: AM. CARE CLINIC - "D-WING"		PROJECT TITLE: REPLACE FINISHES B1AC "D-WING"				DRAWING TITLE: FLOOR PLAN AREA A		PROJECT NO: 653-24-103	OFFICE OF FACILITIES
			DRAWING SCALE: SCALE: NTS	LOCATION: ROSEBURG, OR	DESIGNED: MWR	CHECKED: -	REVIEWED: -	DRAFTED: MWR	BUILDING NO: 1AC	FLOOR NO: 1	SHEET NO: A-03a	

three inches = one foot
one and one half inches = one foot
one inch = one foot
three quarters inch = one foot
one half inch = one foot
one eighth inch = one foot
one quarter inch = one foot
one eighth inch = one foot

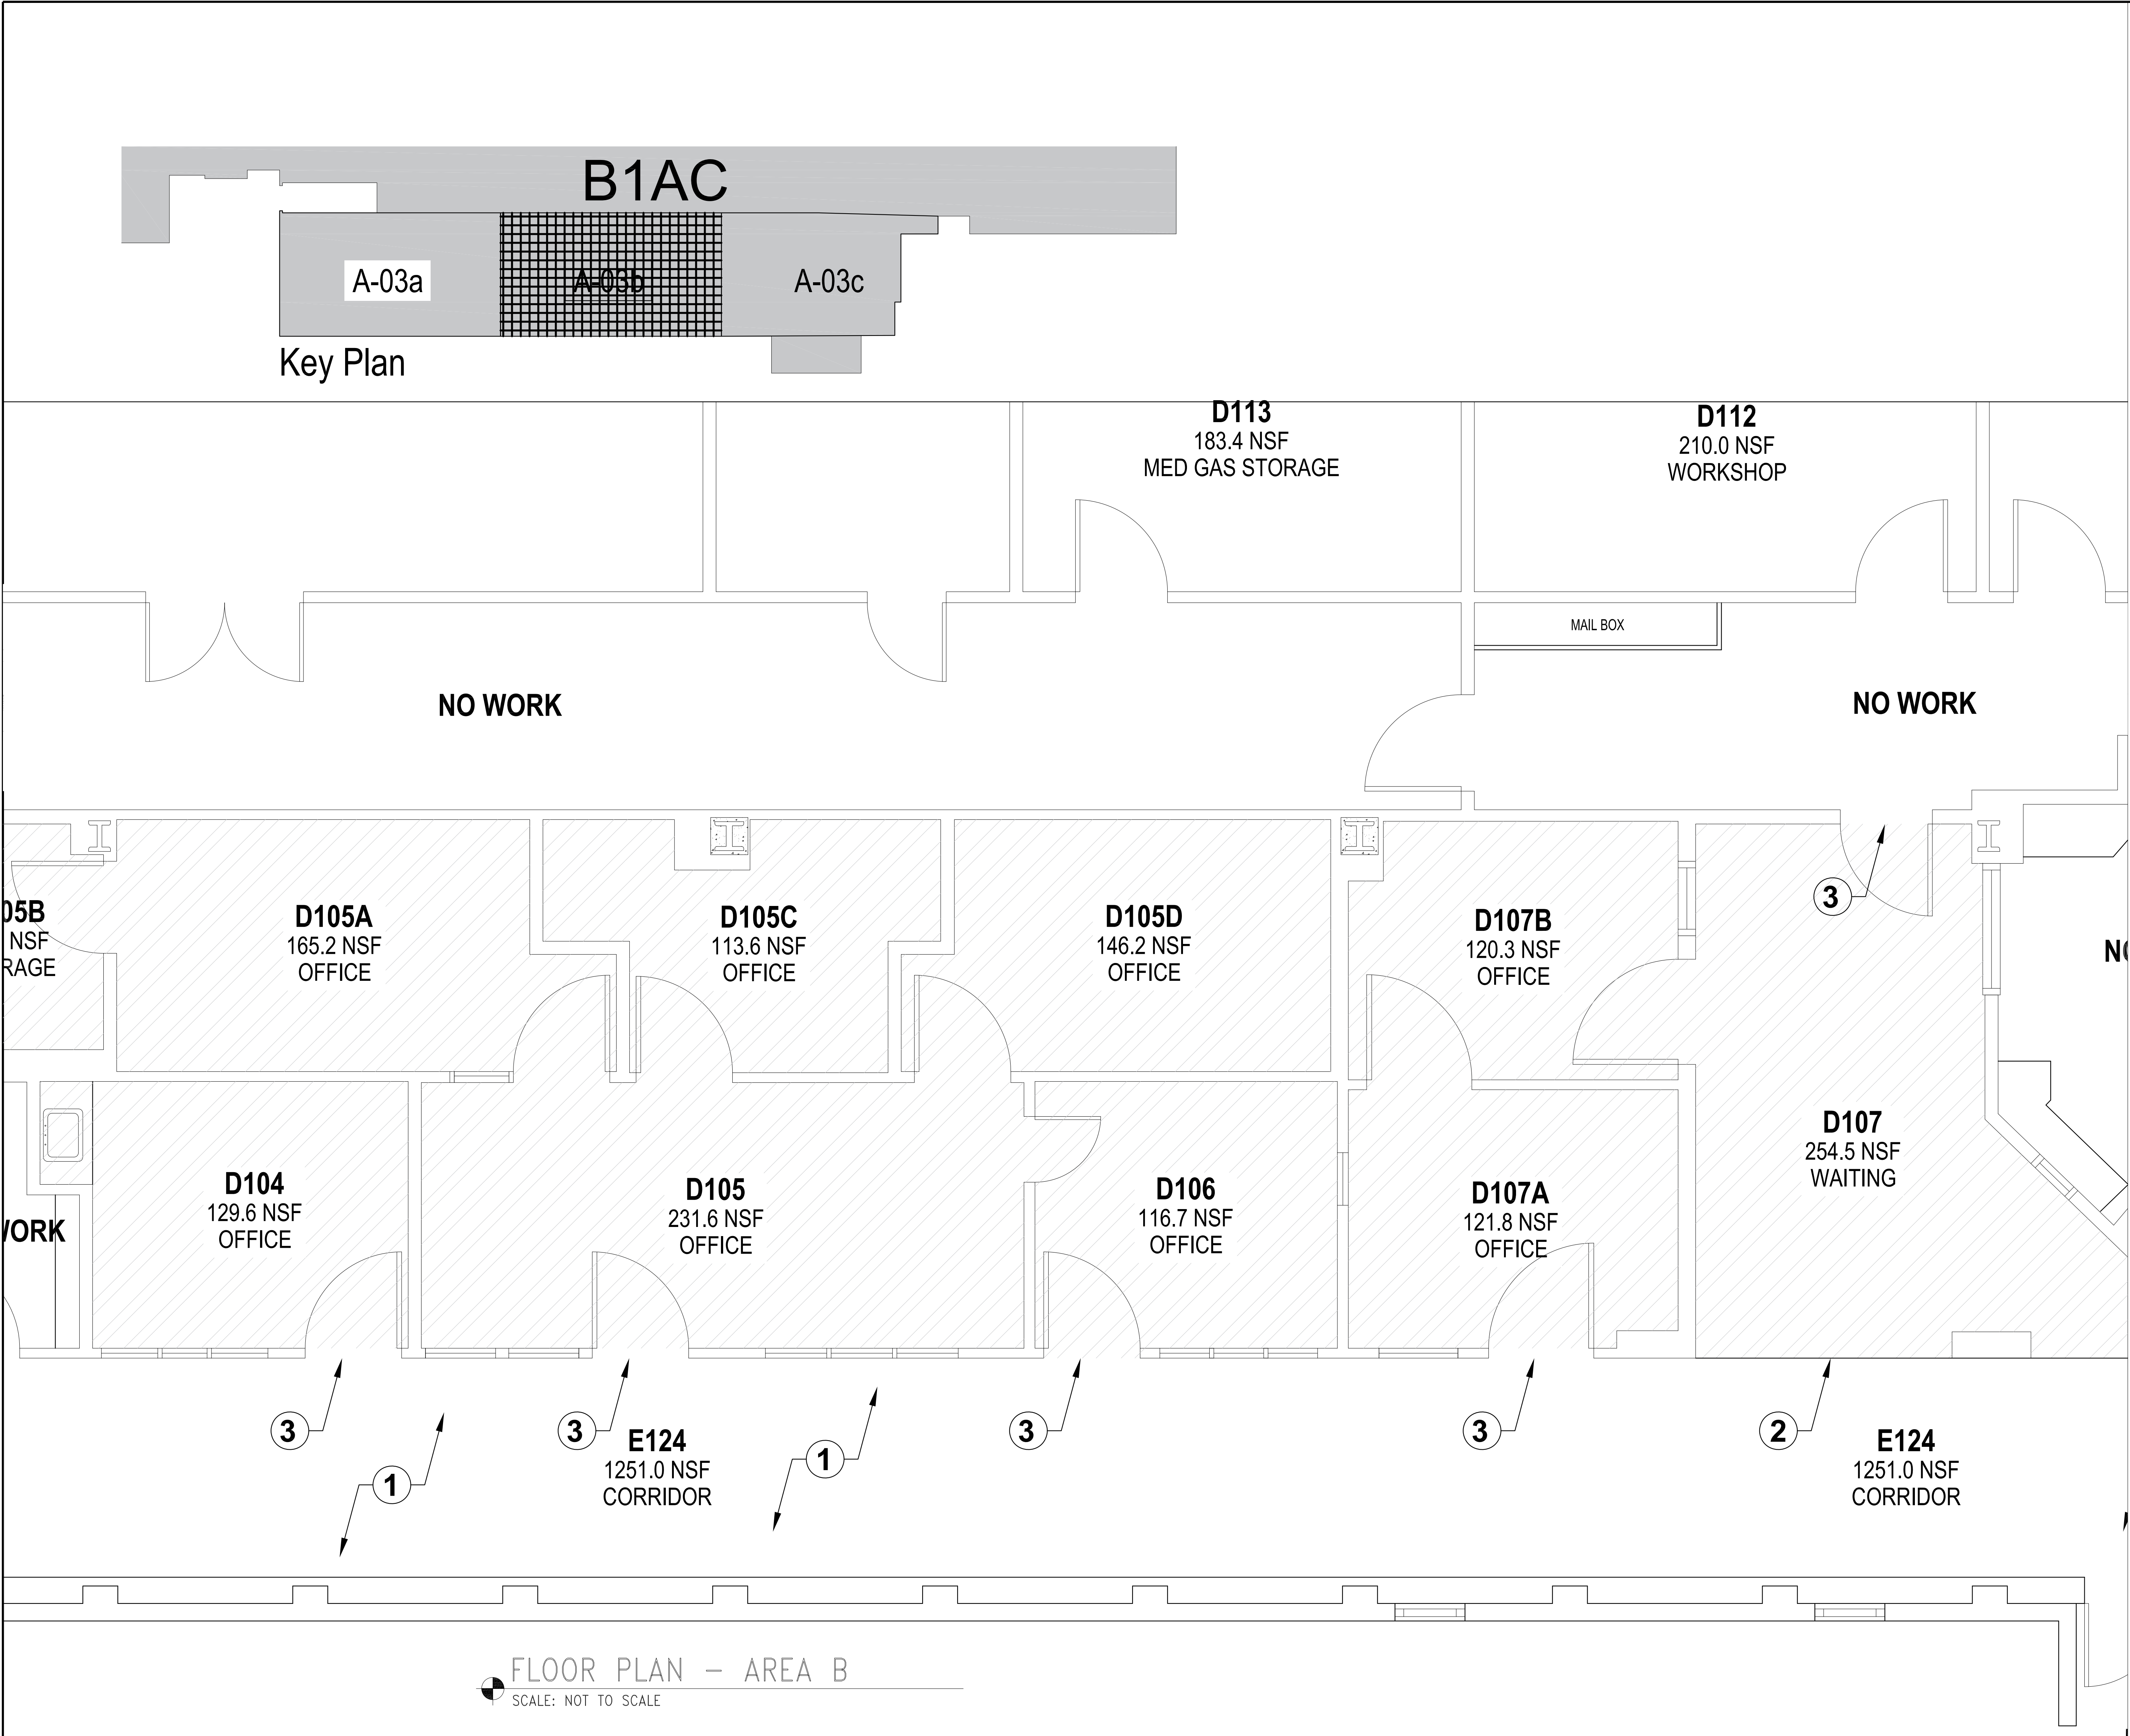

- GENERAL NOTES:
- THESE PLANS DELINEATE THE BASIC SCOPE OF WORK FOR THE REMOVAL OF EXISTING MATERIAL. THE DRAWINGS AND NOTES ARE PROVIDED WITH THE INTENT TO GENERALLY DESCRIBE AREAS AND LIMITS OF WORK. THE CONTRACTOR SHALL BE FAMILIAR WITH THE SITE AND CONDITIONS THERE ON; AND SHALL NOT RELY SOLELY ON REVIEW OF THE BIDDING DOCUMENTS IN DETERMINING THE EXTENT OF WORK REQUIRED. COORDINATION OF THESE DRAWINGS WITH REQUIREMENTS FOR CONTRACT WORK IS THE RESPONSIBILITY OF THE CONTRACTOR. DISCREPANCIES BETWEEN OR WITHIN THE CONTRACT DOCUMENTS SHALL BE REPORTED TO THE CONTRACTING OFFICER IMMEDIATELY. THE CONTRACTOR SHALL PROVIDE CLARITY SKETCHES, DIAGRAMS, AND FIELD DIMENSIONS OF EXISTING CONDITIONS AT THE REQUEST OF THE CONTRACTING OFFICER IF/WHEN CONFLICTS ARE IDENTIFIED.
 - REMOVE ALL PIPES, VALVES, CONTROLS, WIRES, AND CABLES AND APPURTENANCES WHICH SERVE DEVICES BEING REMOVED BACK TO THEIR SOURCE
 - CONTRACTOR SHALL REVIEW ALL CONTRACT DOCUMENTS AND COORDINATE FOR ALL CUTTING, PATCHING AND FINISH WORK.
 - IT IS THE CONTRACTORS RESPONSIBILITY TO FIELD VERIFY ALL EXISTING CONDITIONS.
 - CONTRACTOR TO PATCH AND CAULK ALL PENETRATIONS FROM DEMOLITION WORK WITHIN THE PROJECT SCOPE.
 - UNO, DISCONNECT AND REMOVE ALL EXISTING DEVICES, MAINTAIN CONTINUITY OF ALL REMAINING DEVICES AND EQUIPMENT. PROVIDE JUNCTION BOXES, CONDUIT AND WIRE TO EXTEND EXISTING CIRCUITS AS REQUIRED.
 - CONTRACTOR IS RESPONSIBLE FOR MOVING, REMOVING AND REINSTALLING ITEMS AGAINST AND ON WALLS.
 - NO PORTION OF THE WORK REQUIRING A SHOP DRAWING OR SAMPLE SUBMISSION SHALL BE COMMENCED UNTIL THE SUBMISSION HAS BEEN APPROVED BY THE OWNER'S REPRESENTATIVE. ALL SUCH PORTIONS OF THE WORK SHALL BE IN ACCORDANCE WITH APPROVED SHOP DRAWINGS AND SAMPLE.
 - THE AREA NEARBY THE CONSTRUCTION SITE WILL REMAIN IN OPERATION. COORDINATE WITH THE COR TO SCHEDULE THE WORK. DEMOLITION WORK, AND NOISY WORK MAY NEED TO BE DONE AFTER NORMAL BUSINESS HOURS. THE SAFETY OF THE PUBLIC MUST BE GUARDED CAREFULLY AT ALL PHASES OF CONSTRUCTION.
 - SPRINKLER SYSTEM TO REMAIN ACTIVE IN CONSTRUCTION AREA DURING CONSTRUCTION OR CONTRACTOR TO MEET NFPA 241 BY OTHER METHODS.
 - IT IS THE CONTRACTORS RESPONSIBILITY TO MOVE FURNITURE FROM OFFICES FOR WORK TO BE ACCOMPLISHED AND TO MOVE FURNITURE BACK AFTER WORK IS COMPLETE.
 - CONTRACTOR SHALL SUBMIT A PHASING PLAN TO BE APPROVED BY THE COR PRIOR TO STARTING WORK.
 - REFER TO SPECIFICATIONS AND A-05 FOR ROOM FINISH SCHEDULE.


- KEYED NOTES
- NO NEW FLOORING IN E124 – CORRIDOR. PROVIDE NEW RESILIENT BASE.
 - PATTERN MATCH FLOORING AT NEW/EXISTING FLOORING TRANSITION.
 - FLOORING SEAM SHALL LAND IN THE MIDDLE OF THE DOOR IN THE CLOSED POSITION.

Legend

	PROVIDE NEW FLOORING AND BASE IN THESE LOCATIONS. SEE A05 AND SPECIFICATIONS FOR FINISH SCHEDULE.
--	---

 V.A. ROSEBURG HEALTHCARE SYSTEM VISN20	U.S. DEPARTMENT OF VETERANS AFFAIRS VA ROSEBURG HEALTHCARE SYSTEM 913 NW GARDEN VALLEY BLVD. ROSEBURG, OR. 97471 (541) 440-1000	PROFESSIONAL SEAL	BUILDING NAME: AM. CARE CLINIC – "D-WING"		PROJECT TITLE: REPLACE FINISHES B1AC "D-WING"				DRAWING TITLE: FLOOR PLAN AREA B		PROJECT NO: 653-24-103	OFFICE OF FACILITIES
			DRAWING SCALE: SCALE: NTS	LOCATION: ROSEBURG, OR	DESIGNED: MWR	CHECKED: —	REVIEWED: —	DRAFTED: MWR	BUILDING NO: 1AC	FLOOR NO: 1	SHEET NO: A-03b	

three inches = one foot
one and one half inches = one foot
one inch = one foot
three quarters inch = one foot
one half inch = one foot
three eighths inch = one foot
one quarter inch = one foot
one eighth inch = one foot

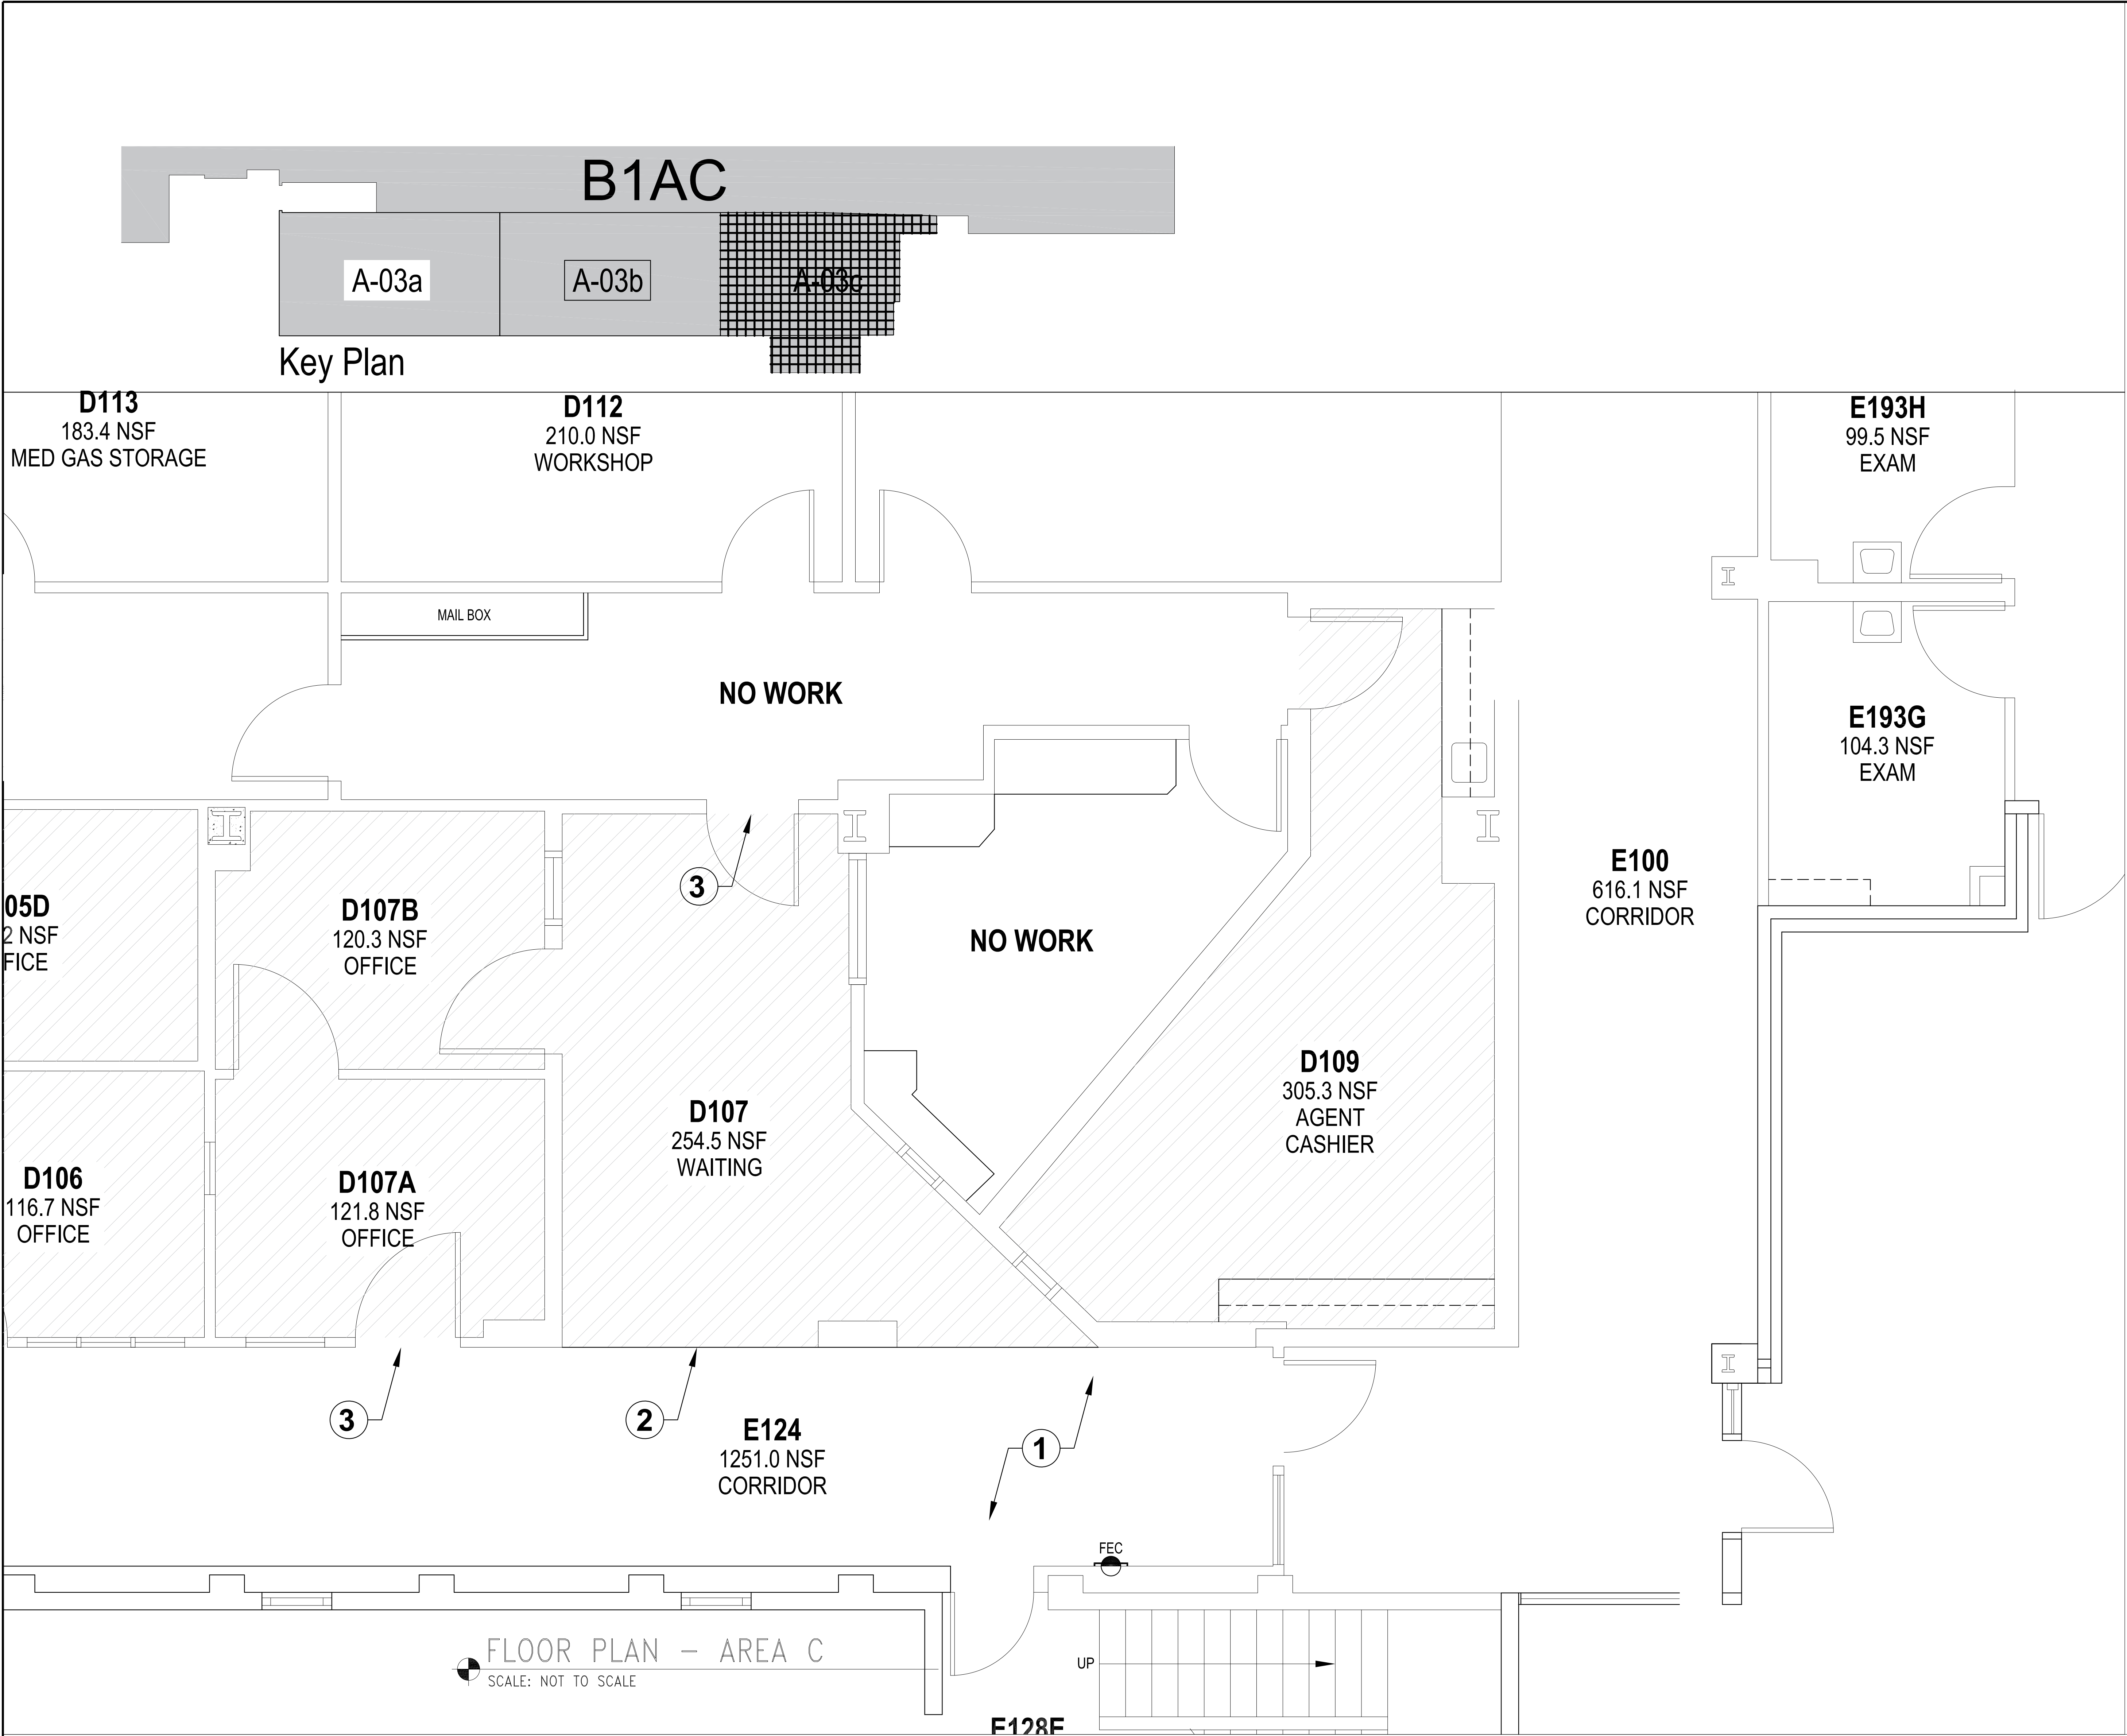


- GENERAL NOTES:
- THESE PLANS DELINEATE THE BASIC SCOPE OF WORK FOR THE REMOVAL OF EXISTING MATERIAL. THE DRAWINGS AND NOTES ARE PROVIDED WITH THE INTENT TO GENERALLY DESCRIBE AREAS AND LIMITS OF WORK. THE CONTRACTOR SHALL BE FAMILIAR WITH THE SITE AND CONDITIONS THERE ON; AND SHALL NOT RELY SOLELY ON REVIEW OF THE BIDDING DOCUMENTS IN DETERMINING THE EXTENT OF WORK REQUIRED. COORDINATION OF THESE DRAWINGS WITH REQUIREMENTS FOR CONTRACT WORK IS THE RESPONSIBILITY OF THE CONTRACTOR. DISCREPANCIES BETWEEN OR WITHIN THE CONTRACT DOCUMENTS SHALL BE REPORTED TO THE CONTRACTING OFFICER IMMEDIATELY. THE CONTRACTOR SHALL PROVIDE CLARITY SKETCHES, DIAGRAMS, AND FIELD DIMENSIONS OF EXISTING CONDITIONS AT THE REQUEST OF THE CONTRACTING OFFICER IF/WHEN CONFLICTS ARE IDENTIFIED.
 - REMOVE ALL PIPES, VALVES, CONTROLS, WIRES, AND CABLES AND APPURTENANCES WHICH SERVE DEVICES BEING REMOVED BACK TO THEIR SOURCE
 - CONTRACTOR SHALL REVIEW ALL CONTRACT DOCUMENTS AND COORDINATE FOR ALL CUTTING, PATCHING AND FINISH WORK.
 - IT IS THE CONTRACTORS RESPONSIBILITY TO FIELD VERIFY ALL EXISTING CONDITIONS.
 - CONTRACTOR TO PATCH AND CAULK ALL PENETRATIONS FROM DEMOLITION WORK WITHIN THE PROJECT SCOPE.
 - UNO, DISCONNECT AND REMOVE ALL EXISTING DEVICES, MAINTAIN CONTINUITY OF ALL REMAINING DEVICES AND EQUIPMENT. PROVIDE JUNCTION BOXES, CONDUIT AND WIRE TO EXTEND EXISTING CIRCUITS AS REQUIRED.
 - CONTRACTOR IS RESPONSIBLE FOR MOVING, REMOVING AND REINSTALLING ITEMS AGAINST AND ON WALLS.
 - NO PORTION OF THE WORK REQUIRING A SHOP DRAWING OR SAMPLE SUBMISSION SHALL BE COMMENCED UNTIL THE SUBMISSION HAS BEEN APPROVED BY THE OWNER'S REPRESENTATIVE. ALL SUCH PORTIONS OF THE WORK SHALL BE IN ACCORDANCE WITH APPROVED SHOP DRAWINGS AND SAMPLE.
 - THE AREA NEARBY THE CONSTRUCTION SITE WILL REMAIN IN OPERATION. COORDINATE WITH THE COR TO SCHEDULE THE WORK. DEMOLITION WORK, AND NOISY WORK MAY NEED TO BE DONE AFTER NORMAL BUSINESS HOURS. THE SAFETY OF THE PUBLIC MUST BE GUARDED CAREFULLY AT ALL PHASES OF CONSTRUCTION.
 - SPRINKLER SYSTEM TO REMAIN ACTIVE IN CONSTRUCTION AREA DURING CONSTRUCTION OR CONTRACTOR TO MEET NFPA 241 BY OTHER METHODS.
 - IT IS THE CONTRACTORS RESPONSIBILITY TO MOVE FURNITURE FROM OFFICES FOR WORK TO BE ACCOMPLISHED AND TO MOVE FURNITURE BACK AFTER WORK IS COMPLETE.
 - CONTRACTOR SHALL SUBMIT A PHASING PLAN TO BE APPROVED BY THE COR PRIOR TO STARTING WORK.
 - REFER TO SPECIFICATIONS AND A-05 FOR ROOM FINISH SCHEDULE.


KEYED NOTES

- NO NEW FLOORING IN E124 - CORRIDOR. PROVIDE NEW RESILIENT BASE.
- PATTERN MATCH FLOORING AT NEW/EXISTING FLOORING TRANSITION.
- FLOORING SEAM SHALL LAND IN THE MIDDLE OF THE DOOR IN THE CLOSED POSITION.



Legend

	PROVIDE NEW FLOORING AND BASE IN THESE LOCATIONS. SEE A05 AND SPECIFICATIONS FOR FINISH SCHEDULE.
--	---

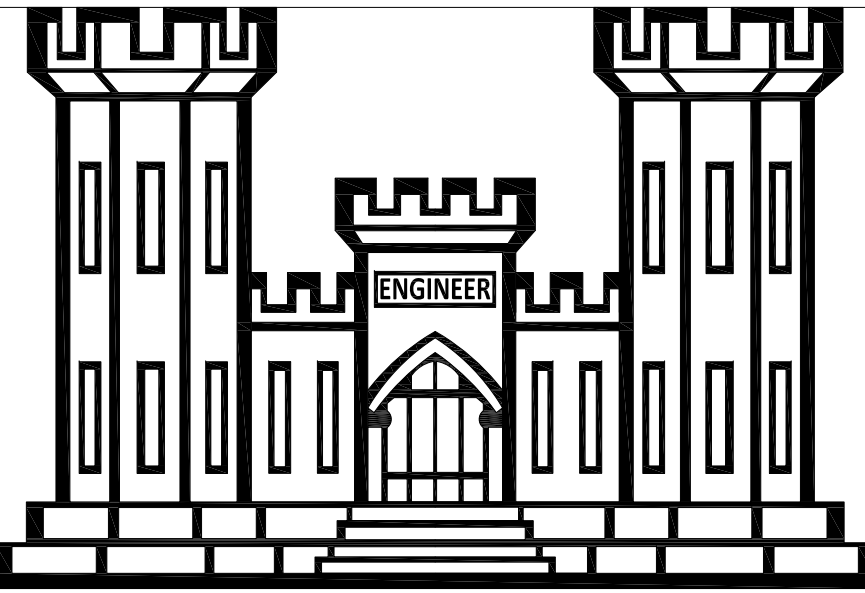	V.A. ROSEBURG HEALTHCARE SYSTEM VA VISN20	U.S. DEPARTMENT OF VETERANS AFFAIRS VA ROSEBURG HEALTHCARE SYSTEM 913 NW GARDEN VALLEY BLVD. ROSEBURG, OR. 97471 (541) 440-1000	PROFESSIONAL SEAL	BUILDING NAME: AM. CARE CLINIC - "D-WING"		PROJECT TITLE: REPLACE FINISHES B1AC "D-WING"				DRAWING TITLE: FLOOR PLAN AREA C		PROJECT NO: 653-24-103		OFFICE OF FACILITIES
				DRAWING SCALE: SCALE: NTS	LOCATION: ROSEBURG, OR	DESIGNED: MWR	CHECKED: -	REVIEWED: -	DRAFTED: MWR	BUILDING NO: 1AC	FLOOR NO: 1	SHEET NO: A-03c		

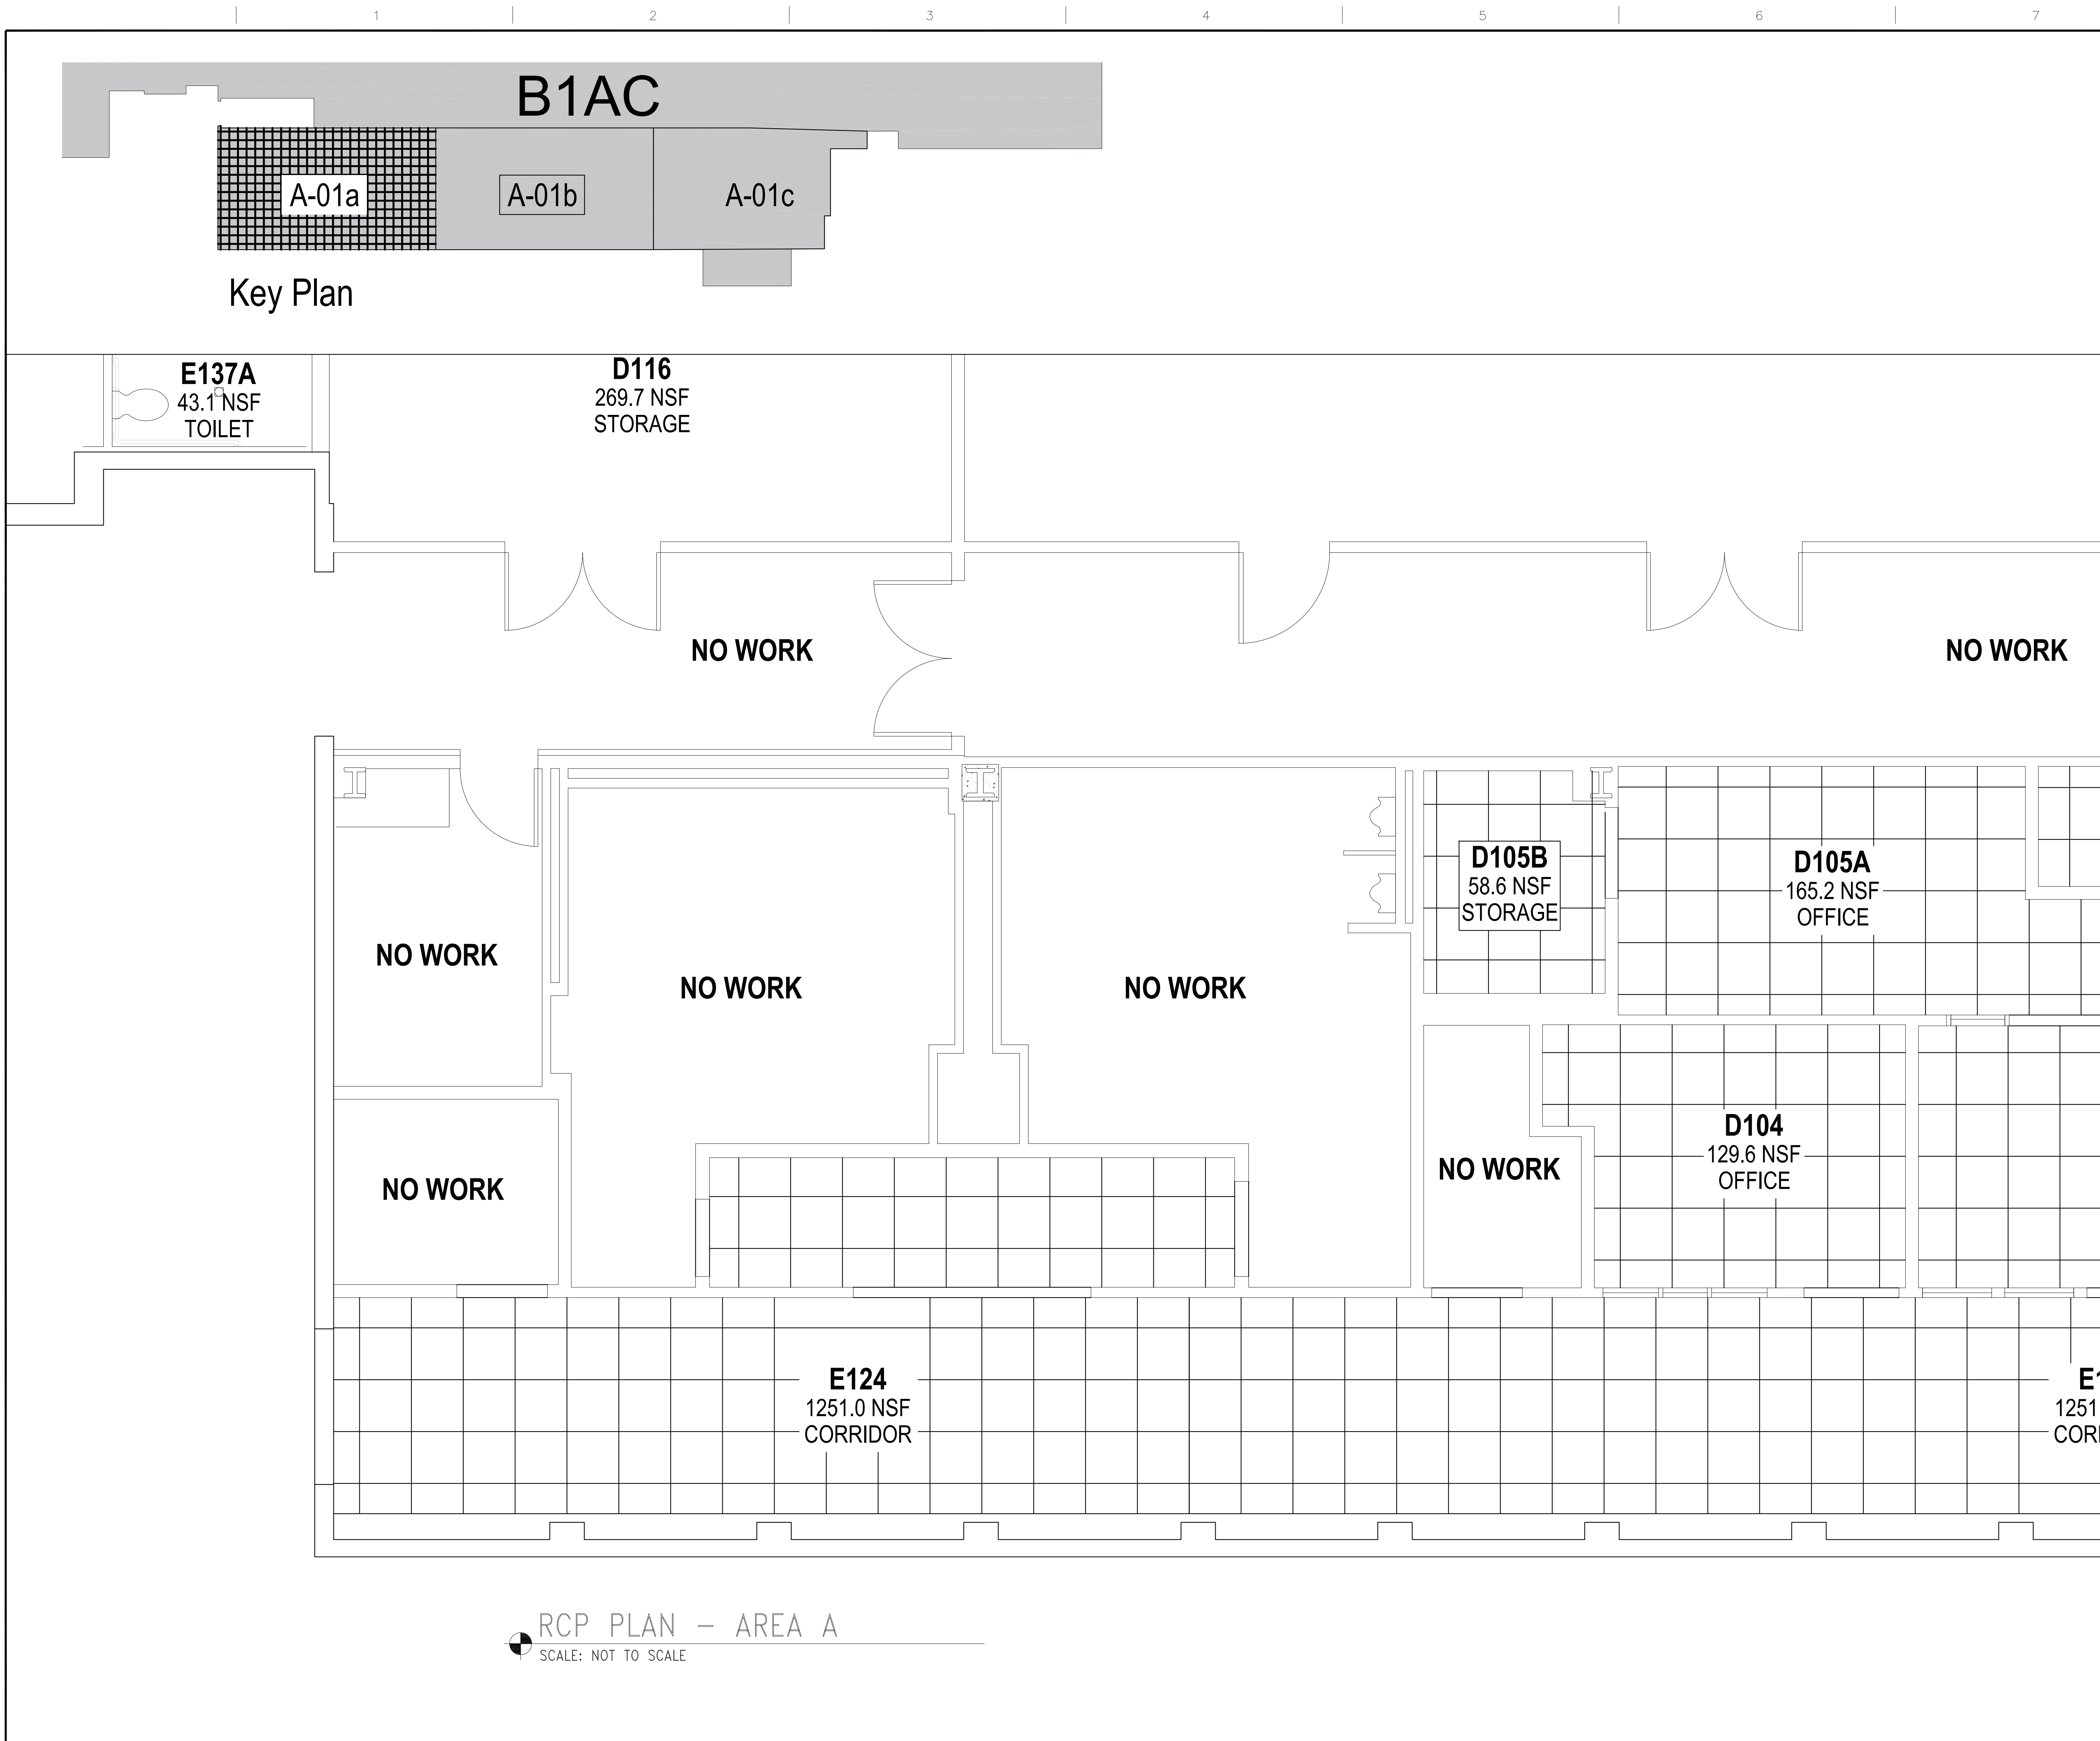

- ## Legend

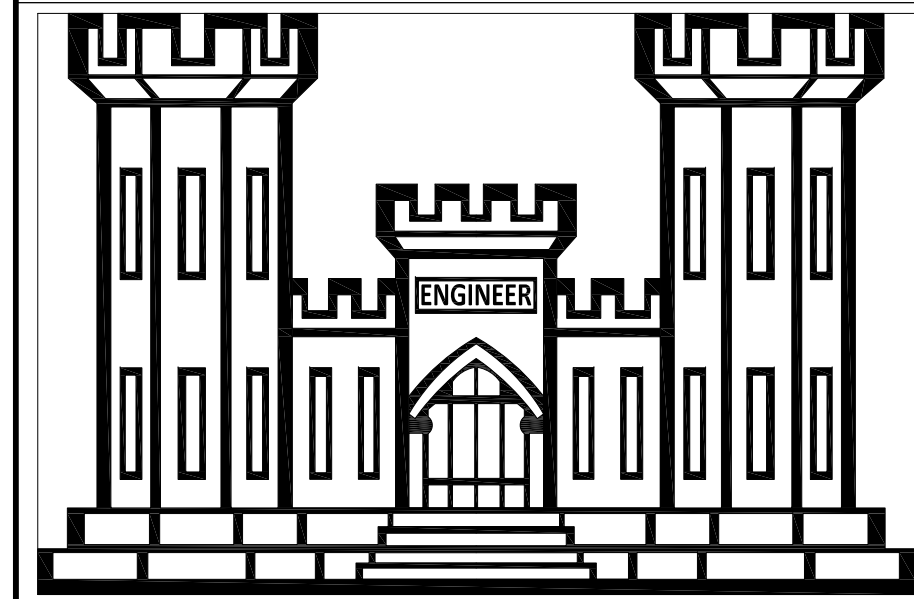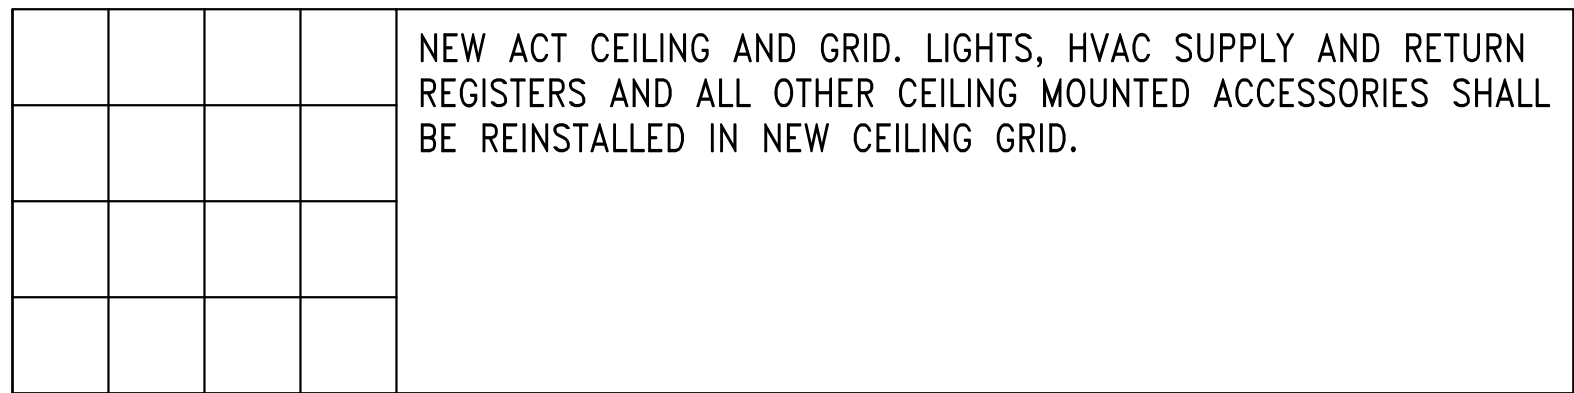

VA
VISN20

U.S. DEPARTMENT OF VETERANS AFFAIRS
VA ROSEBURG HEALTHCARE SYSTEM
913 NW GARDEN VALLEY BLVD.
ROSEBURG, OR. 97471
(541) 440-1000

PROFESSIONAL SEAL

BUILDING NAME:
AM. CARE CLINIC - "D-WING"

DRAWING SCALE:
SCALE: NTS

LOCATION:
ROSEBURG, OR

PROJECT TITLE:
REPLACE FINISHES B1AC
"D-WING"

DESIG
MWR

CHECKED:

REVIEWED

DRAFTED:
MWR

DRAWING TITLE:
RCP PLAN
AREA A

BUILDING NO:
1AC

FLOOR NO:
1


PROJECT NO:
653-24-103

DATE:
5/18/2023

SHEET NO:
A-04a

OFFICE OF
FACILITIES


three inches = one foot
one and one half inches = one foot
one inch = one foot
three quarters inch = one foot
one half inch = one foot
three eighths inch = one foot
one quarter inch = one foot
one eighth inch = one foot

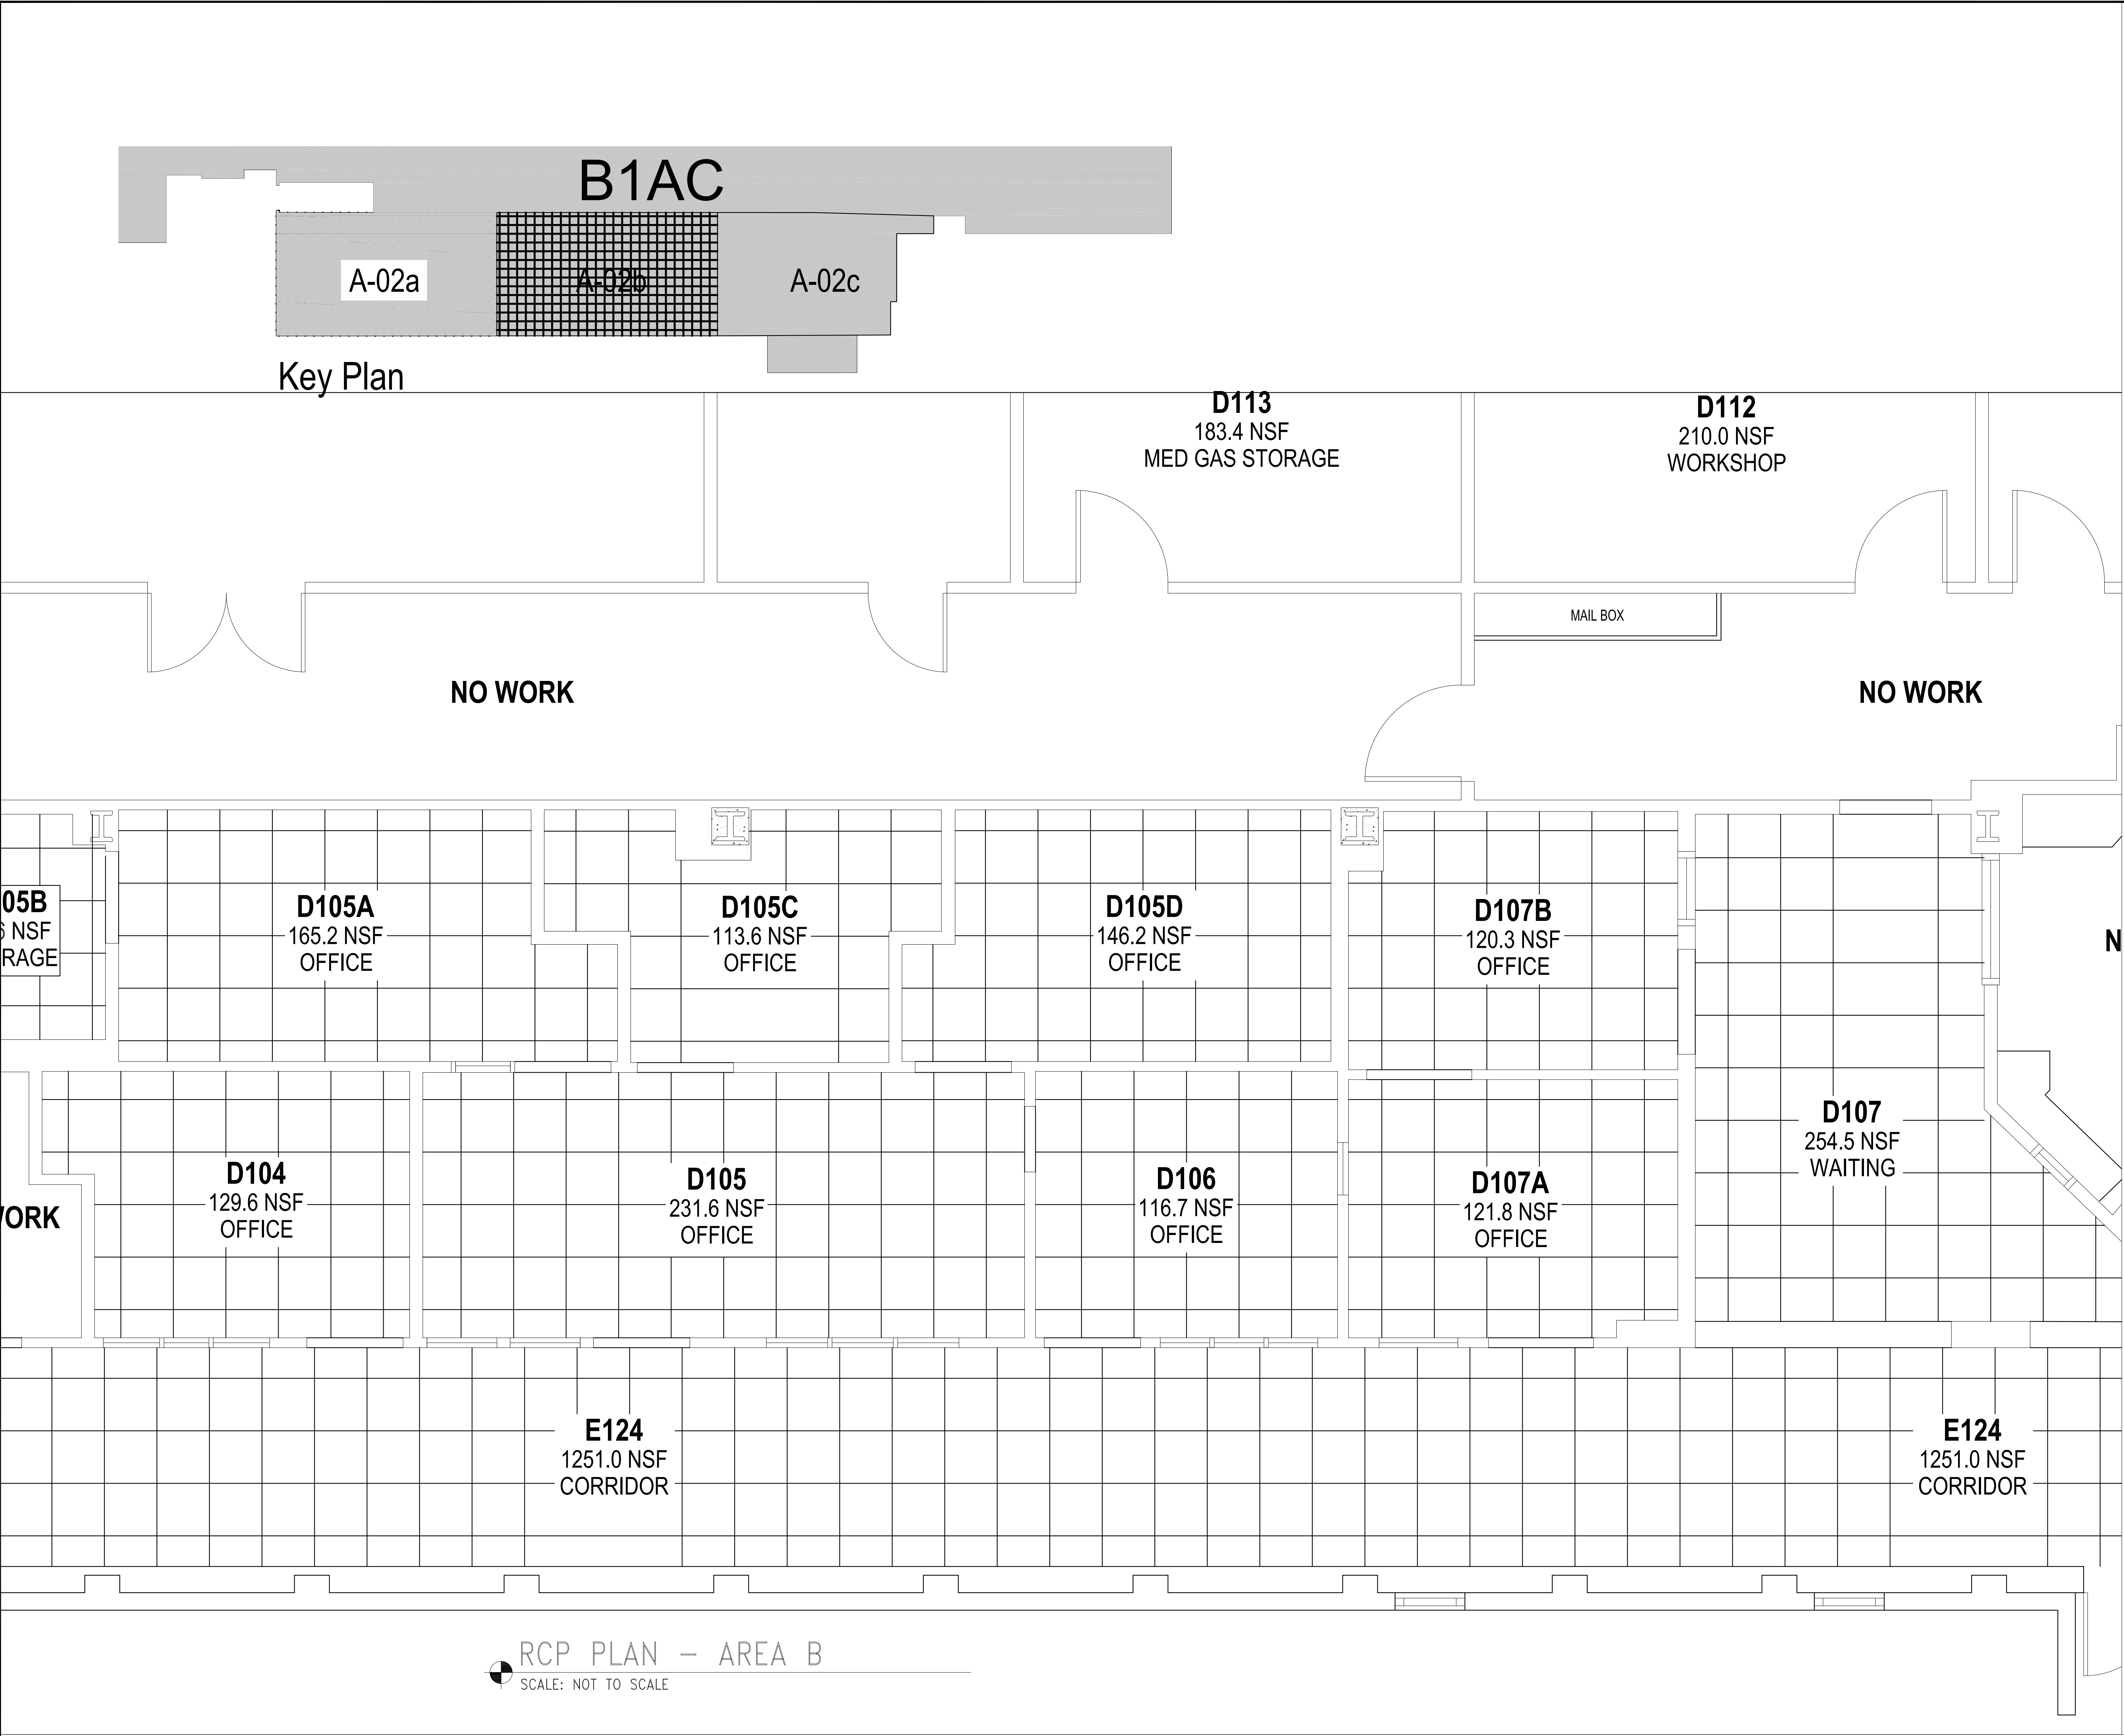

- GENERAL NOTES:
- THESE PLANS DELINEATE THE BASIC SCOPE OF WORK FOR THE REMOVAL OF EXISTING MATERIAL. THE DRAWINGS AND NOTES ARE PROVIDED WITH THE INTENT TO GENERALLY DESCRIBE AREAS AND LIMITS OF WORK. THE CONTRACTOR SHALL BE FAMILIAR WITH THE SITE AND CONDITIONS THERE ON; AND SHALL NOT RELY SOLELY ON REVIEW OF THE BIDDING DOCUMENTS IN DETERMINING THE EXTENT OF WORK REQUIRED. COORDINATION OF THESE DRAWINGS WITH REQUIREMENTS FOR CONTRACT WORK IS THE RESPONSIBILITY OF THE CONTRACTOR. DISCREPANCIES BETWEEN OR WITHIN THE CONTRACT DOCUMENTS SHALL BE REPORTED TO THE CONTRACTING OFFICER IMMEDIATELY. THE CONTRACTOR SHALL PROVIDE CLARITY SKETCHES, DIAGRAMS, AND FIELD DIMENSIONS OF EXISTING CONDITIONS AT THE REQUEST OF THE CONTRACTING OFFICER IF/WHEN CONFLICTS ARE IDENTIFIED.
 - REMOVE ALL PIPES, VALVES, CONTROLS, WIRES, AND CABLES AND APPURTENANCES WHICH SERVE DEVICES BEING REMOVED BACK TO THEIR SOURCE
 - CONTRACTOR SHALL REVIEW ALL CONTRACT DOCUMENTS AND COORDINATE FOR ALL CUTTING, PATCHING AND FINISH WORK.
 - IT IS THE CONTRACTORS RESPONSIBILITY TO FIELD VERIFY ALL EXISTING CONDITIONS.
 - CONTRACTOR TO PATCH AND CAULK ALL PENETRATIONS FROM DEMOLITION WORK WITHIN THE PROJECT SCOPE.
 - UNO, DISCONNECT AND REMOVE ALL EXISTING DEVICES, MAINTAIN CONTINUITY OF ALL REMAINING DEVICES AND EQUIPMENT. PROVIDE JUNCTION BOXES, CONDUIT AND WIRE TO EXTEND EXISTING CIRCUITS AS REQUIRED.
 - CONTRACTOR IS RESPONSIBLE FOR MOVING, REMOVING AND REINSTALLING ITEMS AGAINST AND ON WALLS.
 - NO PORTION OF THE WORK REQUIRING A SHOP DRAWING OR SAMPLE SUBMISSION SHALL BE COMMENCED UNTIL THE SUBMISSION HAS BEEN APPROVED BY THE OWNER'S REPRESENTATIVE. ALL SUCH PORTIONS OF THE WORK SHALL BE IN ACCORDANCE WITH APPROVED SHOP DRAWINGS AND SAMPLE.
 - THE AREA NEARBY THE CONSTRUCTION SITE WILL REMAIN IN OPERATION. COORDINATE WITH THE COR TO SCHEDULE THE WORK. DEMOLITION WORK, AND NOISY WORK MAY NEED TO BE DONE AFTER NORMAL BUSINESS HOURS. THE SAFETY OF THE PUBLIC MUST BE GUARDED CAREFULLY AT ALL PHASES OF CONSTRUCTION.
 - SPRINKLER SYSTEM TO REMAIN ACTIVE IN CONSTRUCTION AREA DURING CONSTRUCTION OR CONTRACTOR TO MEET NFPA 241 BY OTHER METHODS.
 - REFER TO SPECIFICATIONS AND A-05 FOR ROOM FINISH SCHEDULE.

Legend

	NEW CEILING AND GRID. LIGHTS, HVAC SUPPLY AND RETURN REGISTERS AND ALL OTHER CEILING MOUNTED ACCESSORIES SHALL BE REINSTALLED IN NEW CEILING GRID.
--	--

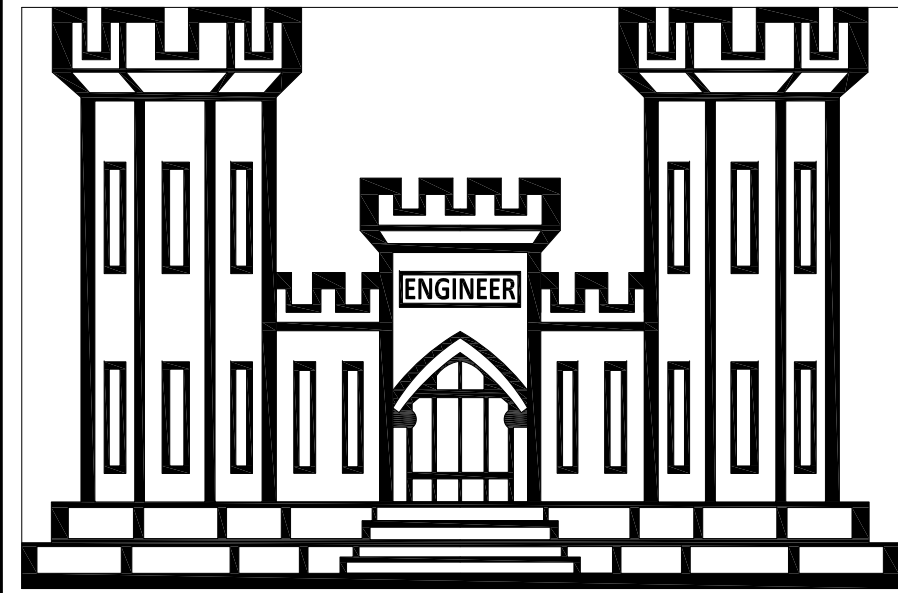

V.A. ROSEBURG
HEALTHCARE SYSTEM
VA
VISN20

U.S. DEPARTMENT OF VETERANS AFFAIRS
VA ROSEBURG HEALTHCARE SYSTEM
913 NW GARDEN VALLEY BLVD.
ROSEBURG, OR. 97471
(541) 440-1000

PROFESSIONAL SEAL

BUILDING NAME:
AM. CARE CLINIC - "D-WING"

DRAWING SCALE:
SCALE: NTS

LOCATION:
ROSEBURG, OR

PROJECT TITLE:
REPLACE FINISHES B1AC
"D-WING"

DESIGNED: MWR
CHECKED: -
REVIEWED: -
DRAFTED: MWR


DRAWING TITLE:
RCP PLAN
AREA B

BUILDING NO: 1AC
FLOOR NO: 1

PROJECT NO:
653-24-103
DATE:
5/18/2023
SHEET NO:
A-04b

OFFICE OF
FACILITIES


three inches = one foot
one and one half inches = one foot
one inch = one foot
three quarters inch = one foot
one half inch = one foot
three eighths inch = one foot
one quarter inch = one foot
one eighth inch = one foot

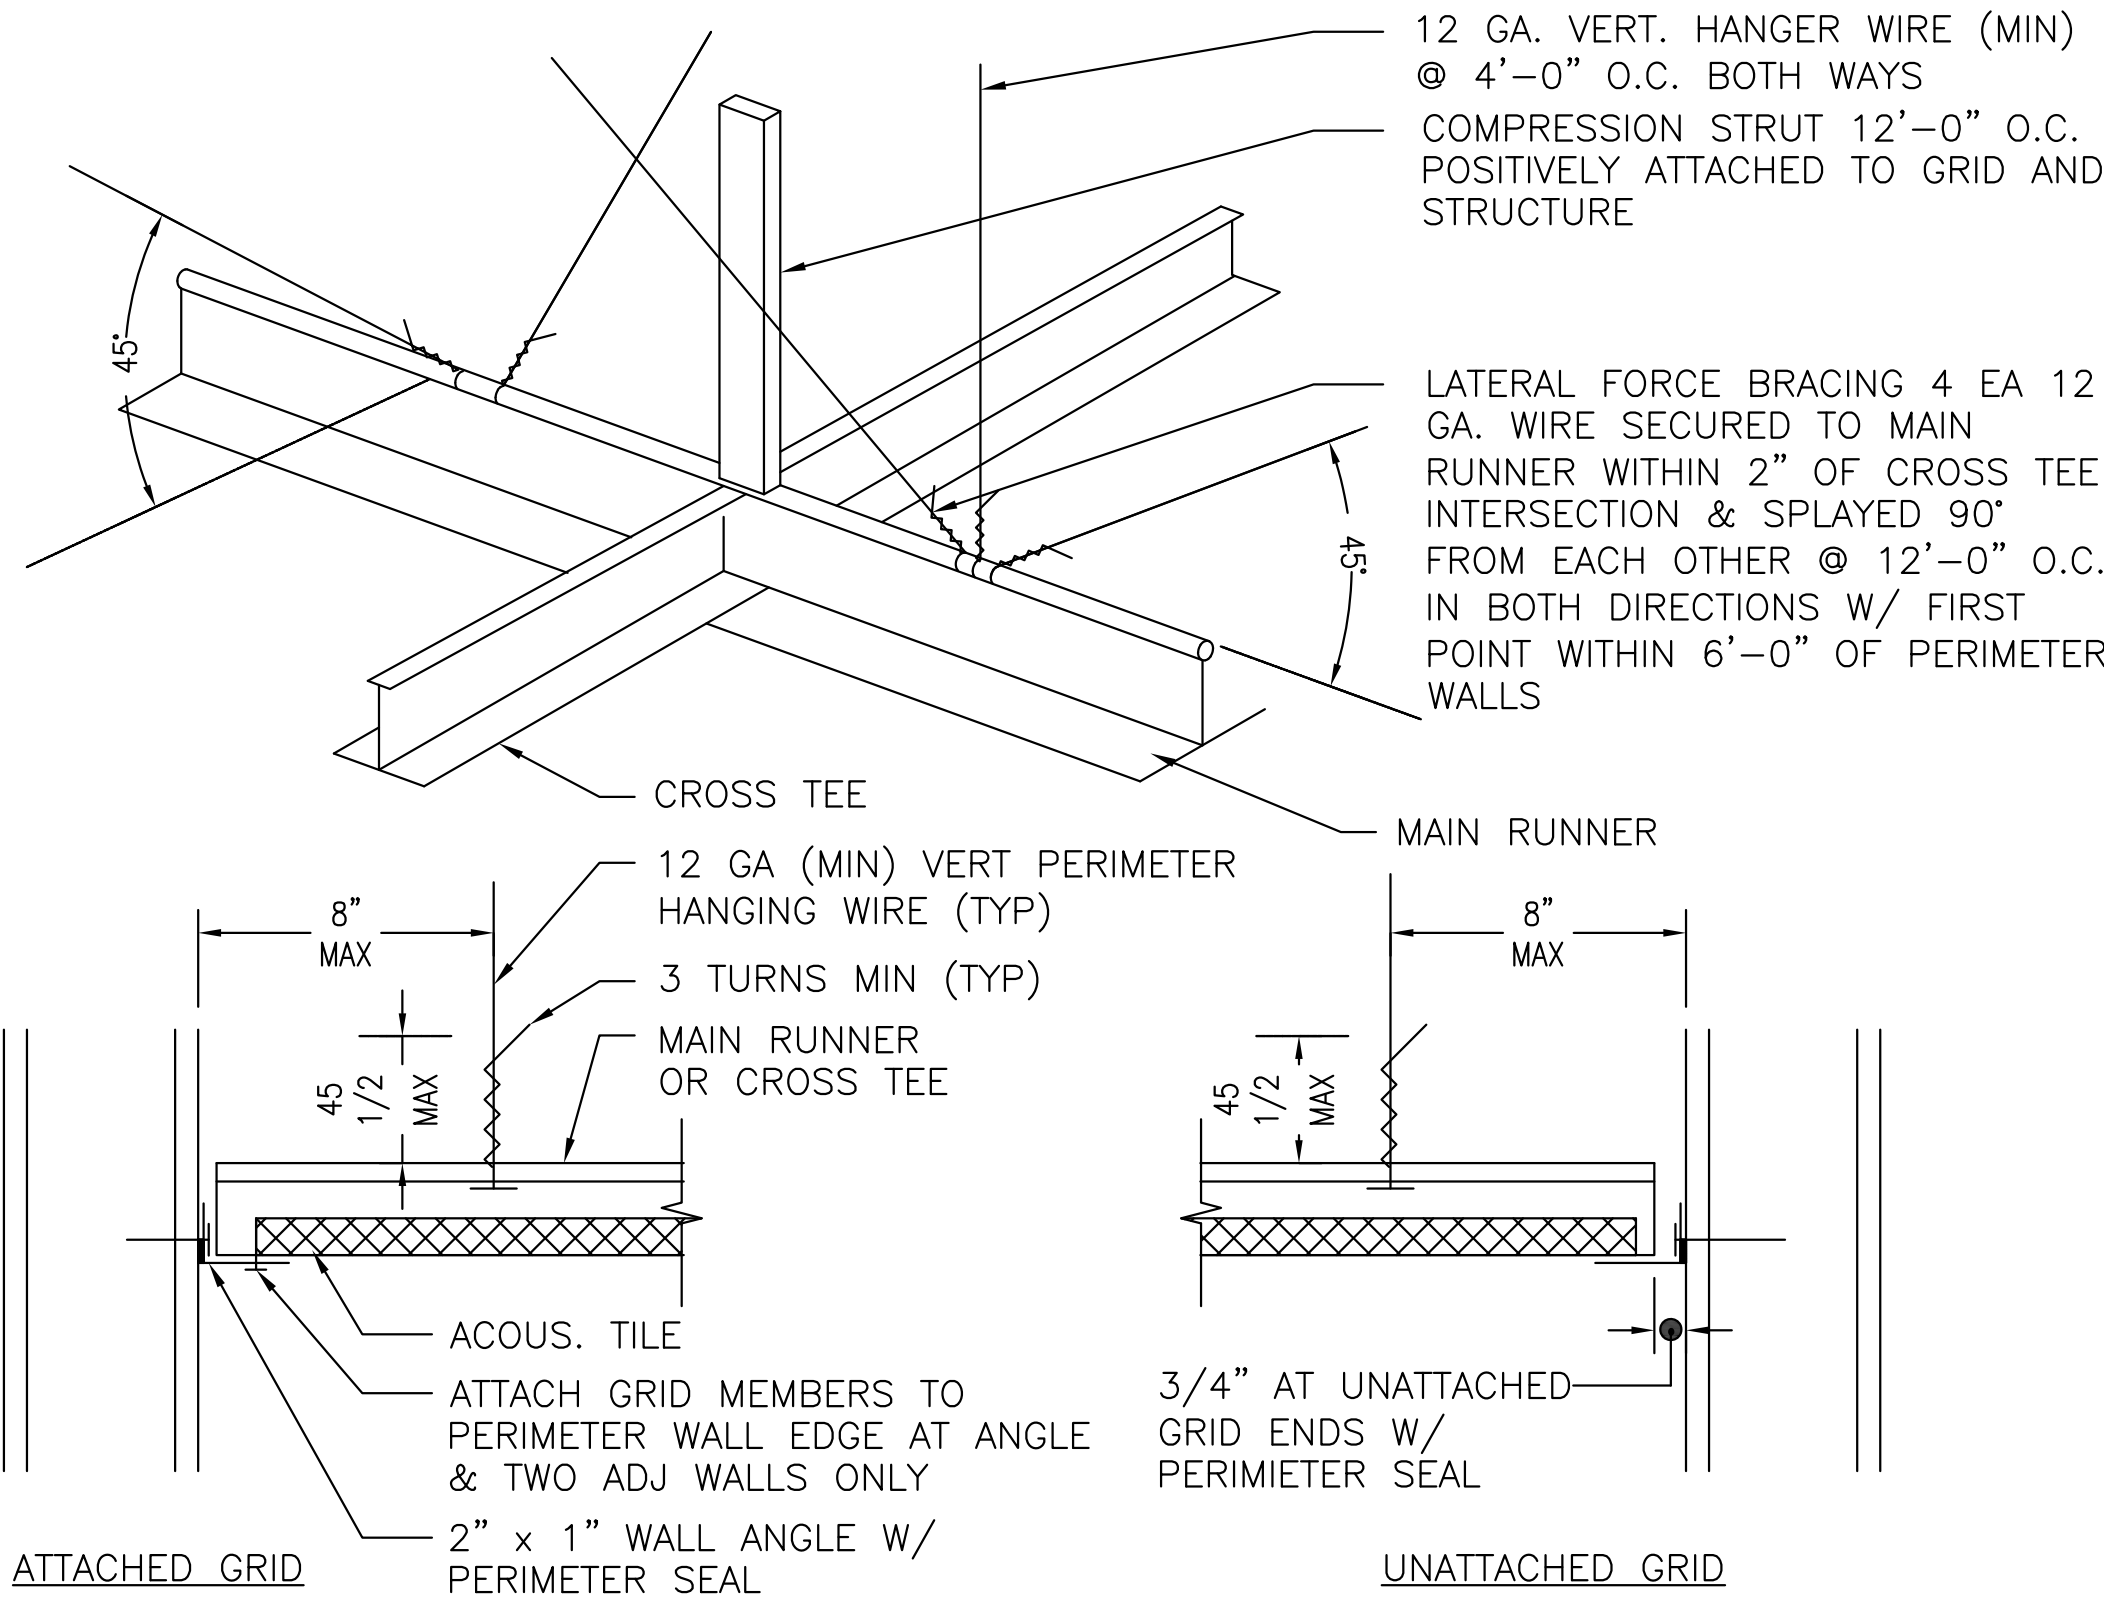

- NOTES:
1. INSTALL SYSTEM IN ACCORDANCE W/ THE LATEST EDITION OF THE INTERNATIONAL BUILDING CODE.
 2. SUPPLY COMPRESSION STRUTS AT GRID INTERSECTION ADJACENT TO LATERAL BRACING POINTS
 3. SUPPLY ADDITIONAL 12 GA WIRES FOR LIGHT FIXTURES AND MECHANICAL SERVICE INDEPENDENT OF GRID SUSPENSION SYSTEM
 4. ACOUSTICAL MATERIALS SHALL COMPLY W/ INTERIOR FINISH REQUIREMENTS OF THE LATEST EDITION OF THE INTERNATIONAL BUILDING CODE.
 5. INSTALL PERIMETER SEAL AS PER SPECIFICATIONS.

CEILING GRID DETAIL


SCALE: NOT TO SCALE

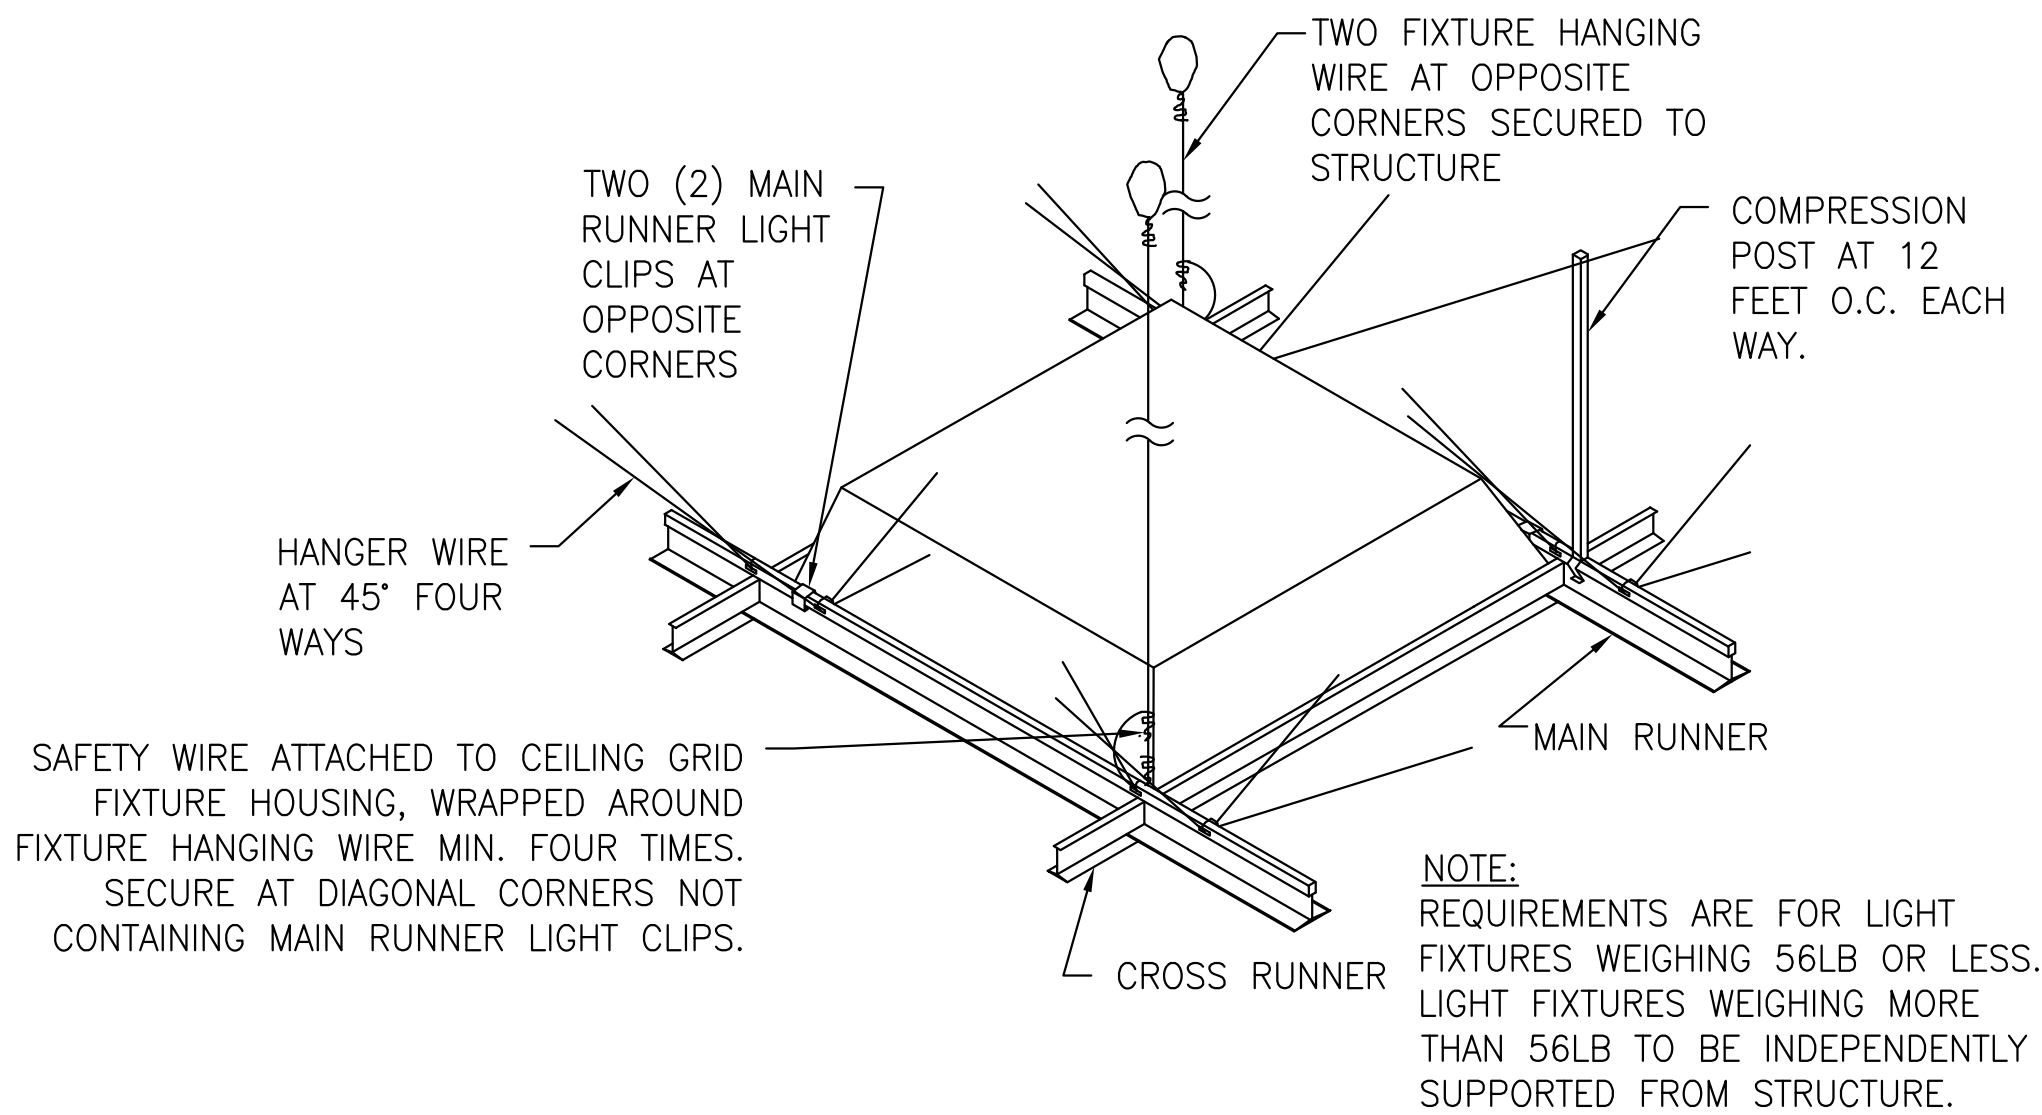

CEILING GRID LIGHT FIXTURE DETAIL (2'-0"x2'-0")

SCALE: NOT TO SCALE

DEMO FLOOR PLAN - AREA A

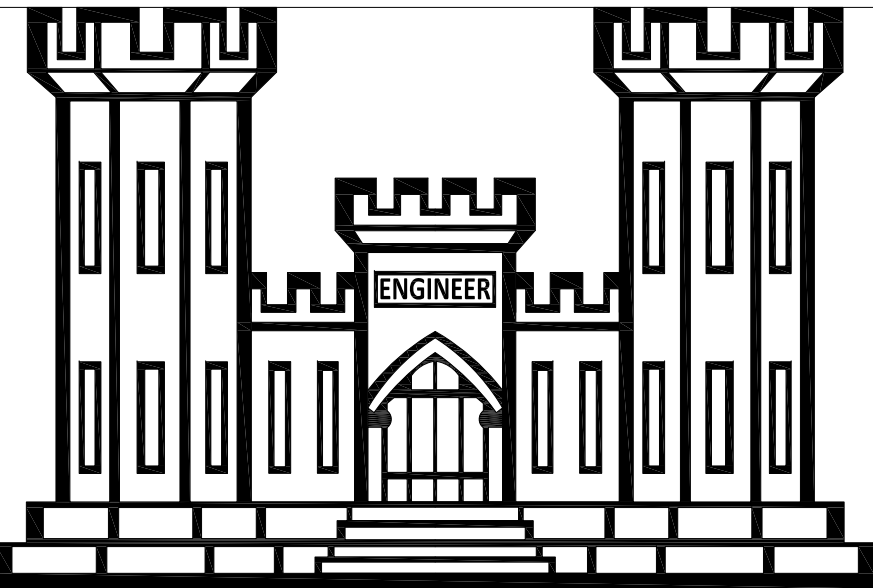

V.A. ROSEBURG
HEALTHCARE SYSTEM

VA

VISN20

U.S. DEPARTMENT OF VETERANS AFFAIRS
VA ROSEBURG HEALTHCARE SYSTEM
913 NW GARDEN VALLEY BLVD.
ROSEBURG, OR. 97471
(541) 440-1000

PROFESSIONAL SEAL

BUILDING NAME:
AM. CARE CLINIC - "D-WING"

PROJECT TITLE:
REPLACE FINISHES B1AC
"D-WING"

DRAWING TITLE:
DETAILS AND FINISH
SCHEDULE

PROJECT NO:
653-24-103

DATE:
5/18/2022

DRAWING SCALE:
SCALE: NTS

LOCATION:
ROSEBURG, OR

DESIGNED:
MWR

CHECKED:
-

REVIEWED:
-

DRAFTED:
MWR

BUILDING NO:
1AC

FLOOR NO:
1

SHEET NO:
A-05

OFFICE OF
FACILITIES