


PHASE I - ROOM FINISH SCHEDULE												
ROOM #	ROOM NAME	CEILING FINISH	FLOOR FINISH	BASE		WAINSCOT		WALL FINISH				COMMENTS
				MAT	HT	MAT	HT	EAST	NORTH	SOUTH	WEST	


100	TR	--	EXP	RB-1	4"	--	--	PT-2	PT-2	PT-2	PT-2	APPLY ANTI-STATIC COATING TO EXPOSED CONCRETE FLOORING
101	MECHANICAL	--	EXP	RB-1	4"	--	--	PT-2	PT-2	PT-2	PT-2	
102	HAC	ACT-1	EP-1	RB-1	4"	--	--	PT-2	PT-2	PT-2	PT-2	
103	IV TESTING	ACT-1	CPT-1	RB-1	4"	--	--	PT-2	PT-2	PT-3	PT-2	PT-3 (ACCENT) ON SOUTH WALL
103A	STG											
104	IV SUPPORT	ACT-1	CPT-1	RB-1	4"	--	--	PT-2	PT-2	PT-3	PT-2	PT-3 (ACCENT) ON SOUTH WALL
105	WAITING ALCOVE	GYP	LVT-1	RB-1	4"	--	--	PT-1	PT-1	PT-1	PT-1	
106	IV TESTING	ACT-1	CPT-1	RB-1	4"	--	--	PT-2	PT-2	PT-3	PT-2	PT-3 (ACCENT) ON SOUTH WALL
107	STAFF BREAK	ACT-1	LVT-2	RB-1	4"	--	--	PT-3	PT-1	PT-1	PT-1	PLAM-1, SDSF-1, PT-3 (ACCENT) ON EAST WALL
108	CHANGE MGMT USER	ACT-1	CPT-1	RB-1	4"	--	--	PT-2	PT-2	PT-3	PT-2	PT-3, (ACCENT) ON SOUTH WALL
109	MECHANICAL	--	EXP	RB-1	4"	--	--	PT-2	PT-2	PT-2	PT-2	
110	RESTROOM	ACT-1	CFT-1	CTB-1	4"	CWT-1	4' - 0"	WC-1	WC-1	WC-1	WC-1	REFERENCE AE424 FOR TILE ELEVATIONS
111	RESTROOM	ACT-1	CFT-1	CTB-1	4"	CWT-1	4' - 0"	WC-1	WC-1	WC-1	WC-1	REFERENCE AE424 FOR TILE ELEVATIONS
112	RESTROOM	ACT-1	CFT-1	CTB-1	4"	CWT-1	4' - 0"	WC-1	WC-1	WC-1	WC-1	REFERENCE AE424 FOR TILE ELEVATIONS
113	RESTROOM	ACT-1	CFT-1	CTB-1	4"	CWT-1	4' - 0"	WC-1	WC-1	WC-1	WC-1	REFERENCE AE424 FOR TILE ELEVATIONS
114	STORAGE	ACT-1	EP-1	RB-1	4"	--	--	PT-2	PT-2	PT-2	PT-2	
115	ELECTRICAL CLOSET	--	EP-1	RB-1	4"	--	--	PT-2	PT-2	PT-2	PT-2	
116	ELECTRICAL ROOM	--	EP-1	RB-1	4"	--	--	PT-2	PT-2	PT-2	PT-2	
CR11-9	CORRIDOR	ACT-1	LVT-1 / LVT-2	PRB-1	4"	--	--	PT-1	PT-1	PT-1	PT-1	
CR11-10	CORRIDOR	ACT-1	LVT-1 / LVT-2	PRB-1	4"	--	--	PT-1	PT-1	PT-1	PT-1	

FINISH ABBREVIATIONS	
ACT	ACOUSTICAL CEILING TILE
CBT	CERAMIC BASE TILE
CFT	CERAMIC FLOOR TILE
CPT	CARPET TILE
CWT	CERAMIC WALL TILE
GYP	GYPSUM BOARD
LVT	LUXURY VINYL TILE
PT	PAINT
EP	EPOXY
EXP	EXPOSED
RB	RUBBER BASE
PRB	PREMIUM RUBBER BASE
WC	WALL COVERING
FLAM	PLASTIC LAMINATE
SDSF	SOLID SURFACE

FINISH PLAN LEGEND	
	LVT-1
	LVT-2

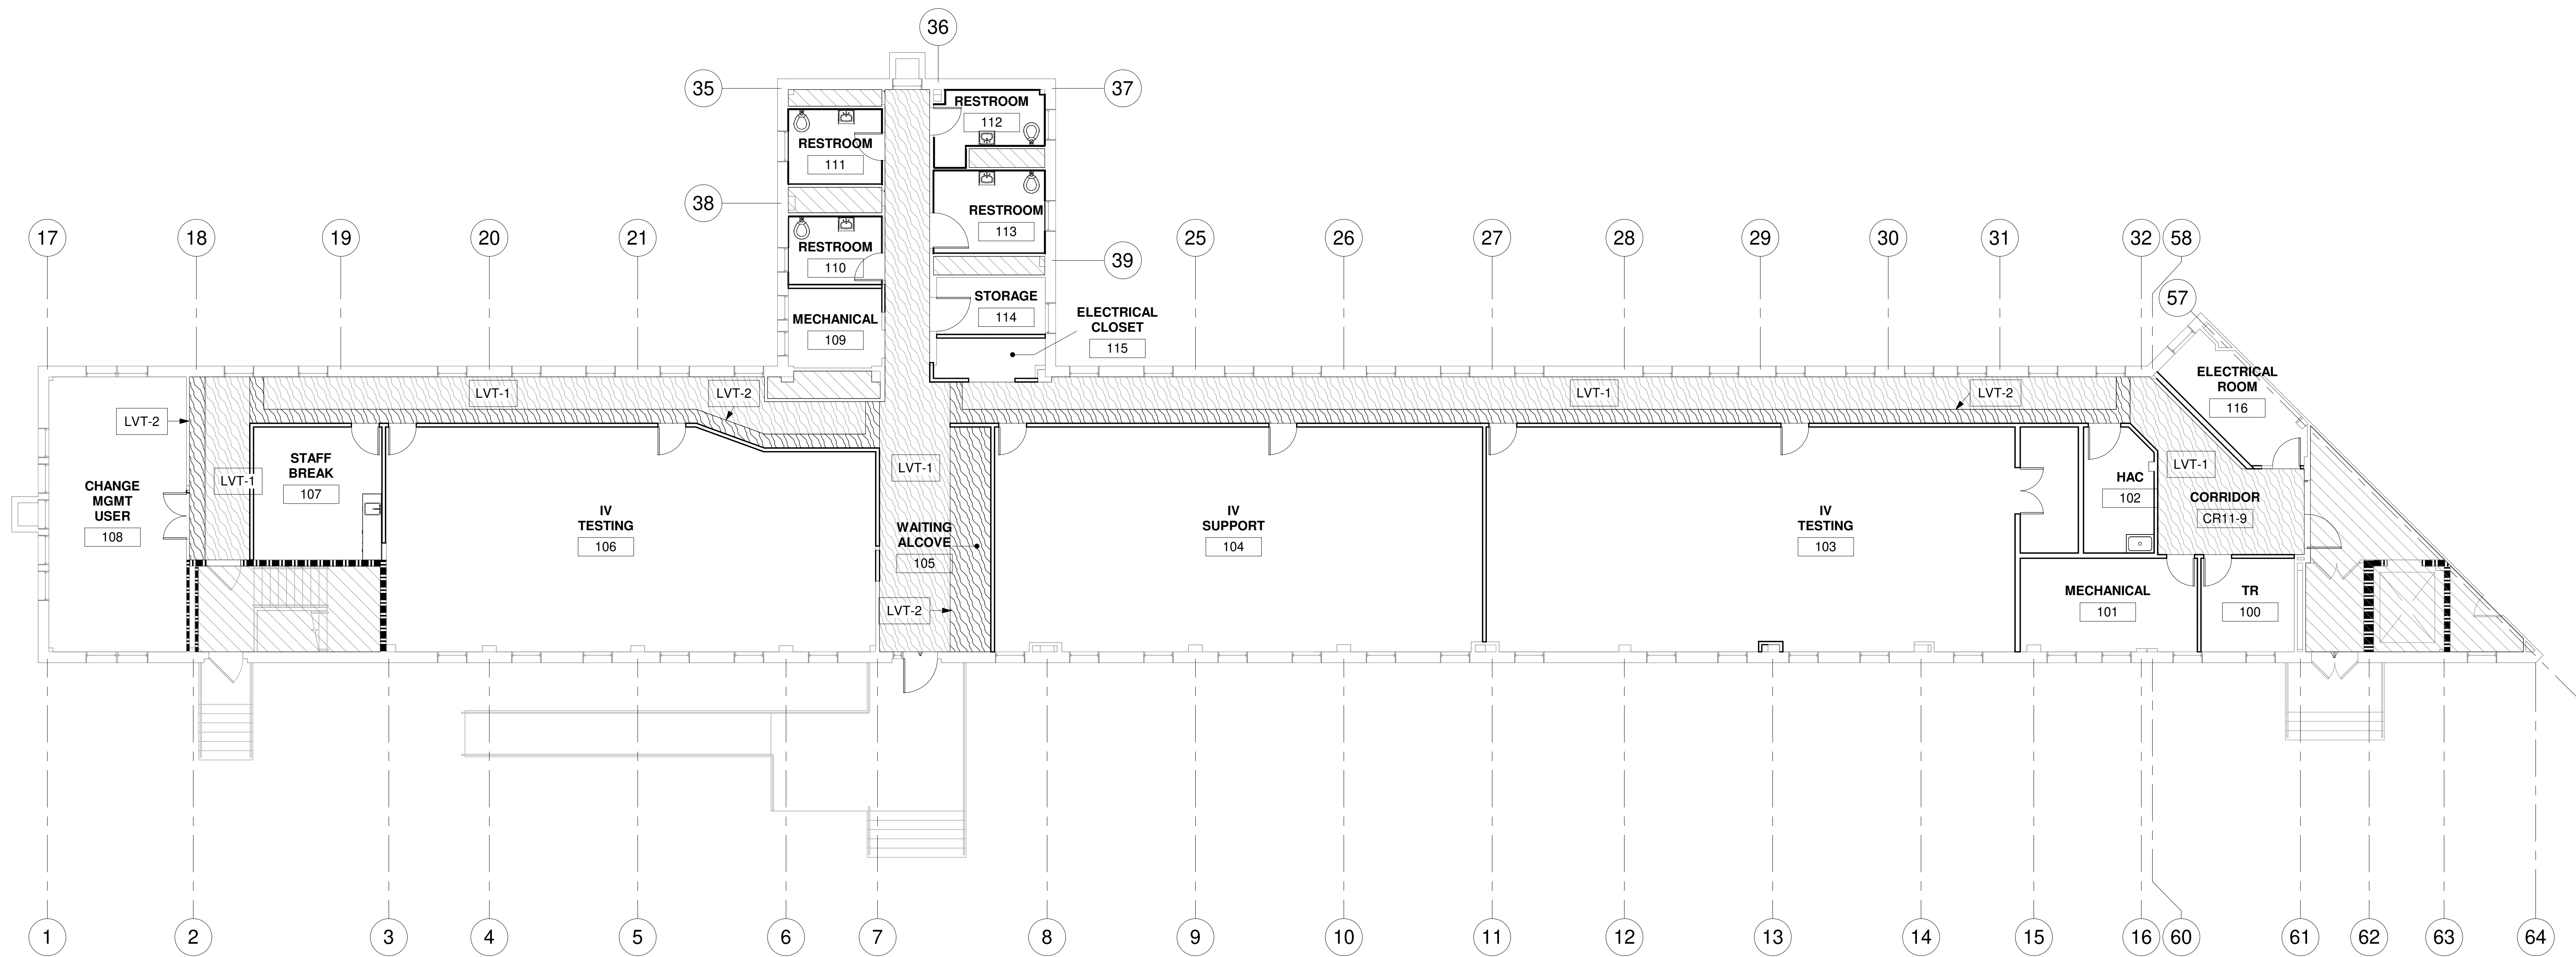

1 FLOOR PLAN - PHASE I - FINISH PLAN
1/8" = 1'-0"

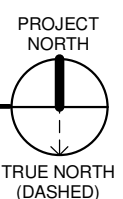[illegible]